Общество с ограниченной ответственностью «Газпром Линде Инжиниринг» /
Gazprom Linde Engineering Limited Liability Company

Заказчик - ООО "РусХимАльянс" / Owner - RusChemAlliance LLC

Gas processing complex within Ust-Luga ethane-rich Gas Processing Cluster. Gas processing plant and utilities, infrastructure and Offsite Process Facilities

Газоперерабатывающий комплекс в составе Комплекса переработки этансодержащего газа в районе поселка Усть-Луга. Газоперерабатывающий завод и Технологические объекты общезаводского хозяйства

Резервуары противопожарного запаса воды
Fire Water Storage Tanks

Насосная станция противопожарного водоснабжения
Fire Water Pump Station

РАБОЧАЯ ДОКУМЕНТАЦИЯ
DETAIL DESIGN DOCUMENTATION

Проектирование электрической части
Electrical Engineering

Опросный лист.
Групповой щит рабочего освещения
Data Sheet.
Local Normal Lighting Panel

GLE-(G0-D8810BX0)-EL-DS-EPNUC-001

2024

Общество с ограниченной ответственностью «Газпром Линде Инжиниринг» /
Gazprom Linde Engineering Limited Liability Company

Заказчик - ООО "РусХимАльянс" / Owner - RusChemAlliance LLC

Gas processing complex within Ust-Luga ethane-rich Gas Processing Cluster. Gas processing plant and utilities, infrastructure and Offsite Process Facilities

Газоперерабатывающий комплекс в составе Комплекса переработки этансодержащего газа в районе поселка Усть-Луга. Газоперерабатывающий завод и Технологические объекты общезаводского хозяйства

Резервуары противопожарного запаса воды
Fire Water Storage Tanks

Насосная станция противопожарного водоснабжения
Fire Water Pump Station

РАБОЧАЯ ДОКУМЕНТАЦИЯ
DETAIL DESIGN DOCUMENTATION

Проектирование электрической части
Electrical Engineering

Опросный лист.
Групповой щит рабочего освещения
Data Sheet.
Local Normal Lighting Panel

GLE-(G0-D8810BX0)-EL-DS-EPNUC-001

Главный инженер проекта
Chief Project Engineer

И.В. Трофимов
I.V. Trofimov

2024

Взам. инв. №
Подпись и дата
Инв. № подл

СОДЕРЖАНИЕ / CONTENTS

1. Общие положения 2
1. General 2
2. Лист технических данных на Групповой щит рабочего освещения/ 2
2. Technical data sheet for Local Normal Lighting Panel 2
3. Приложение А Схема принципиальная электрическая / 4
3. Appendix A Electrical schematic diagram 4
Лист регистрации изменений / Revision Change Details 5

Статус Status	Рев. Rev.	Дата Date	Назначение выпуска / Reason for Issue	Разраб. Drawn	Проверил Checked	Утвердил Approved
IFP	02	31.08.24	Выпущено для заказа на закупку / Issued for purchase order	Зубаиров	Любимова	Трофимов
IFR	01	31.07.24	Выпущено для рассмотрения / Issued for review	Зубаиров	Любимова	Трофимов

	Stage	Sheet №	Total sheets
GAS PROCESSING COMPLEX WITHIN UST-LUGA ETHANE-RICH GAS PROCESSING CLUSTER. GAS PROCESSING PLANT AND UTILITIES, INFRASTRUCTURE AND OFFSITE PROCESS FACILITIES	G0-D8810BX0 Fire Water Pump Station	DDD	1	5
	Data Sheet. Local Normal Lighting Panel	РУСХИМАЛЬЯНС		

GLE-(G0-D8810BX0)-EL-DS-EPNUC-001

Газоперерабатывающий комплекс в составе Комплекса переработки этансодержащего газа в районе поселка Усть-Луга. Газоперерабатывающий завод и Технологические объекты общезаводского хозяйства

Изм.	Кол.уч	Лист	№док	Подп.	Дата		Стадия	Лист	Листов
Разраб.		Зубаиров			31.08.24	G0-D8810BX0 Насосная станция противопожарного водоснабжения	Р	1	5
Проверил		Любимова			31.08.24				
Нач. сек.		Оловянишников			31.08.24	Опросный лист. Групповой щит рабочего освещения	ГЛИнжиниринг ПРОЕКТИРУЕМ БУДУЩЕЕ ОТРАСЛИ		
Н. контр.		Конев			31.08.24				
ГИП		Трофимов			31.08.24				

Согласовано | Взам. инв. № | Подпись и дата | Инв. № подл

1. Общие положения

1. General

Статус / Status	Ответ (да / нет) / Answer (yes / no)	
Замена существующего оборудования / Replacement of existing equipment	Нет / no	
Вновь вводимое оборудование / Newly introduced equipment	Да / yes	
Предприятие Заказчик / Enterprise Owner	ООО «РусХимАльянс» / RusChemAlliance LLC	
Наименование объекта / Name of object	Gas processing complex within Ust-Luga ethane-rich Gas Processing Cluster.Gas processing plant and utilities, infrastructure and Offsite Process Facilities / Газоперерабатывающий комплекс в составе Комплекса переработки этансодержащего газа в районе поселка Усть-Луга. Газоперерабатывающий завод и Технологические объекты общезаводского хозяйства хозяйства	
Наименование титула / Name of title	Насосная станция противопожарного водоснабжения / Fire Water Pump Station	
№ технологической позиции (№ Тега) / № of technological position (№ of Tag)	G0-EPNUC-D88-01	

2. Лист технических данных на Групповой щит рабочего освещения/

2. Technical data sheet for Local Normal Lighting Panel

№ п/п / № p/p	Технические характеристики (наименование параметра) / Technical characteristics (parameter name)	Требуемые значения параметров / Required values parameters	Предлагаемое участником конкурса / Proposed by the bidder
1 Общие характеристики / General characteristics			
2	Количество шкафов, шт. / Quantity of cabinets, pcs.	1	
3	Номинальное напряжение, кВ / Nominal voltage, kV	400	
4	Вид системы заземления щита по ГОСТ Р 50571.2 / Type of shield grounding system according to GOST R 50571.2	TN-S	
5	Наличие УЗИП / Availability SPD	Приложение А / Appendix A	
6	Номинальная мощность (10 % запас), кВА / Nominal power of transformer (10% reserve), kVA	Приложение А / Appendix A	
7	T°C окружающей среды / T°C environment	+10 °C / +35 °C	
8	Влажность / Humidity	60% при +35°C 90% при +20°C / 60% at +35°C 90% at +20°C	
9	Размещение / Placement	Внутреннее / Internal	
10	Допустимая высота установки над уровнем моря, м / Permissible installation height above sea level, m	До 1000 / To 1000	
11	Сейсмостойкость по шкале MSK, баллы / Earthquake resistance on MSK scale, points	5	

№ п/п / № p/p	Технические характеристики (наименование параметра) / Technical characteristics (parameter name)	Требуемые значения параметров / Required values parameters	Предлагаемое участником конкурса / Proposed by the bidder
12	Степень защиты / Degree of protection	IP31*	
13	Цвет корпуса / Color of enclosure	RAL 7004	
14	Климатическое исполнение (У, ХЛ) и категория размещения по ГОСТ 15150-69 / Climatic execution (U, HL) and placement category according to GOST 15150-69	УХЛ4 / UHL4	
15	Исполнение шкафное настенной установки по ГОСТ Р 51321.1-2007 / Cabinet version of wall mounting according to GOST R 51321.1-2007	Да / Yes	
16	Условия обслуживания – одностороннее / Service conditions - one-sided	Да / Yes	
17	Обслуживание переднее / Service front	Да / Yes	
18	Ввод кабелей сверху через кабельные вводы / Cable entry from below via cable glands	Да / Yes	
19	Наличие в шкафах выдвижных элементов (да, нет) / Presence of sliding elements in cabinets (yes, no)	Нет / No	
20	Количество и параметры отходящих и вводных линий согласно схеме / Number and parameters of outgoing and incoming lines according to the scheme	Приложение А / Appendix A	


Примечания:

1. Характеристики, отмеченные «*» уточняются заводом-изготовителем оборудования.
2. Все параметры группового щита рабочего освещения должны соответствовать документам GLE-(G0-Z00300X0)-EL-PB-002 «Основные принципы проектирования освещения и розеточной цепи», GLE-(G0-Z00300X0)-EL-FD-005 «Типовые схемы подключения распределительных щитов», GLE-(G0-Z00300X0)-EL-SD-006 «Технические требования на распределительное устройство низкого напряжения».
3. В части рисков, связанных с возможным изменением величины нагрузок и количества потребителей, Поставщик должен учесть 25 % по оборудованному резерву (ошиновка, выключатели, пускозащитная аппаратура, УПП и проч.). Резерв следует применять в процентном отношении к задействованным рабочим фидерам.
4. Поставщик обязан представить в составе РКД опросный лист, выполненный в соответствии с фактическими данными по уточненным техническим характеристикам электропотребителей, полученными от Заказчика.

Notes:

1. Specifications marked with «*» are specified by the equipment manufacturer.
2. All parameters of the group panel of working lighting must comply with the documents GLE-(G0-Z00300X0)-EL-PB-002 «Basic Principles of Lighting and Socket Circuit Design», GLE-(G0-Z00300X0)-EL-FD-005 «Typical Connection Diagrams. Distribution Boards», GLE-(G0-Z00300X0)-EL-SD-006 «Specification for LV Switchgear».
3. In terms of risks related to possible changes in the magnitude of loads and number of consumers, the Supplier shall take into account 25% for the equipped reserve (busbar, circuit breakers, starting and protection equipment, SS etc.). The reserve shall be applied as a percentage of the working feeders involved.
4. The Supplier is obliged to submit as part of the Vendor Documents a questionnaire made in accordance with the actual data on the specified technical characteristics of electrical consumers received from the Customer.

Приложение А. Схема принципиальная электрическая / Appendix A. Electrical schematic diagram

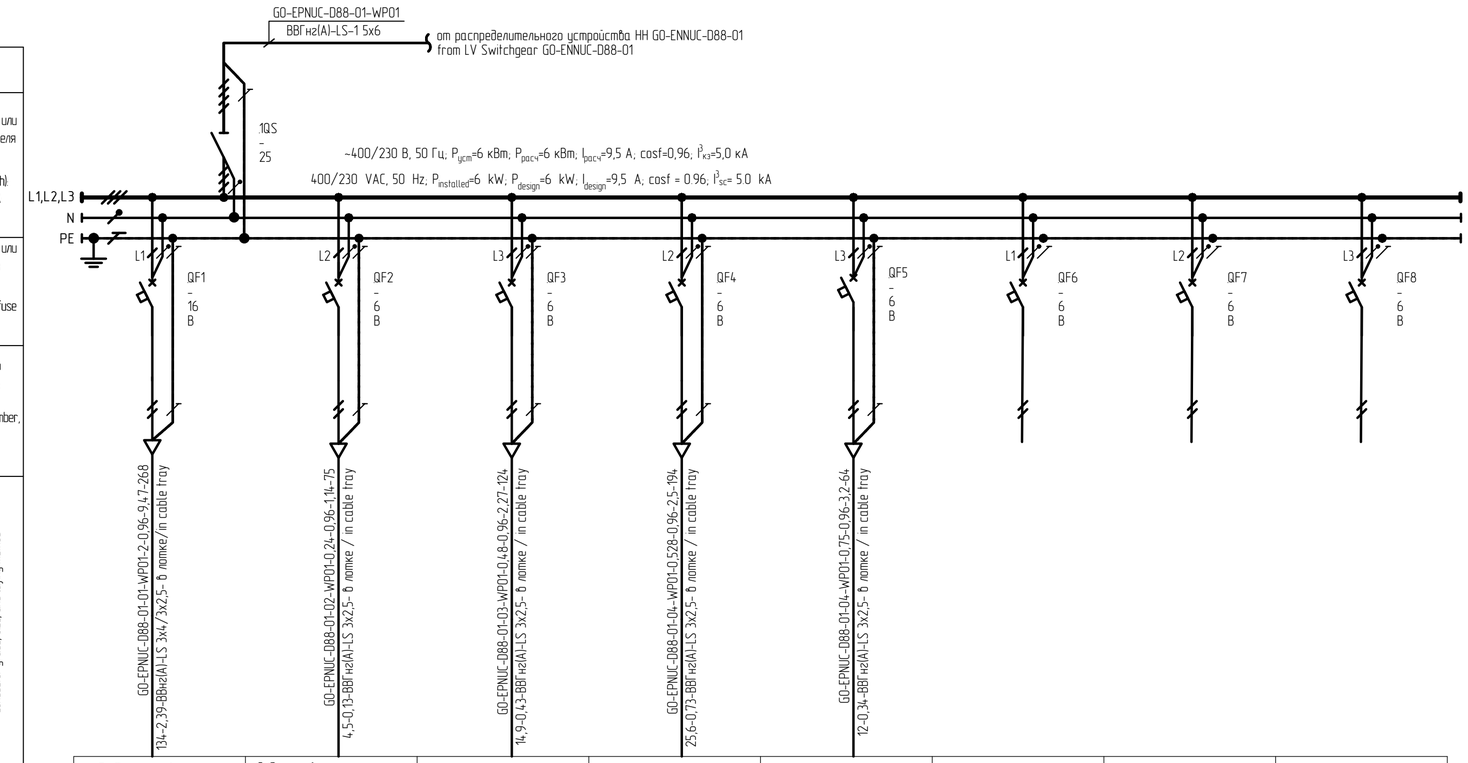

Источник питания Power supply	Рабочее освещение машинного зала пом.1 на отм. -3.000 / Working lighting of the engine room room.1 at l. -3.000	Рабочее освещение машинного зала пом.1 на отм. -3.000 под площадкой разгрузки и пом. 6/ Working lighting of the engine room room.1 at l. -3.000 under the unloading area and room. 6	Рабочее освещение электрощитовой / Working lighting of switchgear room	Рабочее освещение помещений 2-5, 7-10 / Working lighting rooms 2-5, 7-10	ЯТП 230/12 В / Step-down substation 230/12 V box	Резерв / Spare	Резерв / Spare	Резерв / Spare
Аппарат на вводе (выключатель автоматический или выключатель нагрузки) номер, тип, ток расцепителя или номинальный ток, А Incomer device (circuit breaker or load break switch) number, type, tripping current or rated current, A	2	0,24	0,48	0,528	0,75	-	-	-
Аппарат на линии (выключатель автоматический или предохранитель) номер, тип, ток расцепителя или плавкой вставки, А Line device (circuit breaker or fuse) number, type or fuse current, A	9,47/5*In	1,14/5*In	2,27/5*In	2,5/5*In	3,2/-	-	-	-
Пускатель магнитный (устройство защитного отключения или другие аппараты) номер, тип, номинальный ток, А Magnetic starter (tripping device or other devices) number, type, rated current, A	0,288	0,232	0,197	0,330	0,15	-	-	-
Маркировка - расчетная нагрузка, кВт - коэффициент мощности - расчетный ток, А - длина участка, м Marking rated power, kW power factor design current, A - section length, m	Момент нагрузки, кВт·м - потеря напряжения, % - марка, сечение проводника, способ прокладки Load torque, kW·m voltage loss, % conductor grade, size, and laying method							
Наименование потребителя, назначение линии Consumer name, line purpose								
Установленная мощность, кВт Installed power, kW								
Расчетный / пусковой ток, А Design / starting current, A								
Однофазный ток КЗ, кА Single phase short-circuit current, kA								

Поз. Item	Обозначение Ident. no.	Наименование Description	Кол. Qty	Масса ед., кг Weight per item,kg	Примечание Note
GO-EPNUC-		Щиток навесной модульный, металлическй /	1		
-D88-01		Modular hinged panel, metal			
1QS		Выключатель нагрузки четырёхполюсный/	1		
		Four-pole load switch - 4 p In =25A			
		Выключатель автоматический, характеристика			
		срабатывания B (6кА)./Automatic switch			
		response characteristic V (6kA).			
QF1		-однополюсный / single-pole 1 p B In =16A	1		
QF2-QF8		-однополюсный / single-pole 1 p B In =6A	7		

Взам. инв. N

Подп. и дата

Инв. N подл.

Изм.	Кол. уч.	Лист	N док.	Подп.	Дата	GLE-(GO-D8810BX0)-EL-DS-EPNUC-001	Лист 4

GLE-(GO-D8810BX0)-EL-DS-EPNUC-001_02_AL.DWG

Формат А4х3

Лист регистрации изменений / Revision Change Details

Статус / Status	Рев. / Rev.	Место изменения / Location of Changes	Краткое описание изменения / Brief description of the change
IFP	02	Все / All	Откорректировано по замечаниям Заказчика GLE-(G0-D8810BX0)-EL-DS-EPNUC-001_01_AL_CRS / Corrected according to the Customer's comments GLE-(G0-D8810BX0)-EL-DS-EPNUC-001_01_AL_CRS

Взам. инв. №

Подпись и дата

Инв. № подл

Изм.	Кол.уч	Лист	№док	Подп.	Дата	GLE-(G0-D8810BX0)-EL-DS-EPNUC-001	Лист 5