Ведомость рабочих чертежей основного комплекта
List of Detail Drawings of Main Package

Лист Sheet	Наименование	Description	Примечание Note
1-6	**Общие данные** GLE-(G0-D8810BX0)-EL-ELOV-ZA-001_04_AL.pdf GLE-(G0-D8810BX0)-EL-ELOV - ZA-001_04_AL.docx	**General Data** 04.3-1 GLE-(G0-D8810BX0)-EL-ELOV-ZA-001_04_AL.pdf GLE-(G0-D8810BX0)-EL-ELOV - ZA-001_04_AL.docx	Рев.04.1 Rev.04.1 Рев.04.3 Rev.04.3 Рев.04.4 Rev.04.4
7	**Структурная схема щита рабочего освещения** GLE-(G0-D8810BX0)-EL-ELOV-ZA-001_04_AL.pdf GLE-(G0-D8810BX0)-EL-ELOV - ZA-001_04_AL.dwg	**Block Diagram. Normal Lighting Panel** GLE-(G0-D8810BX0)-EL-ELOV-ZA-001_04_AL.pdf GLE-(G0-D8810BX0)-EL-ELOV - ZA-001_04_AL.dwg	Рев.04.5 Rev.04.5
8	**Структурная схема щита аварийного освещения** GLE-(G0-D8810BX0)-EL-ELOV-ZA-001_04_AL.pdf GLE-(G0-D8810BX0)-EL-ELOV - ZA-001_04_AL.dwg	**Block Diagram. Emergency Lighting Panel** GLE-(G0-D8810BX0)-EL-ELOV-ZA-001_04_AL.pdf GLE-(G0-D8810BX0)-EL-ELOV - ZA-001_04_AL.dwg	Рев.04.6 Rev.04.6

ООО «РусХимАльянс»
Документ согласован
Управлением
проектирования ГПЗ и ОЗХ

Изменение 04.6 выполнено ООО "ГЛ ИНЖИНИРИНГ" / Revision 04.6 issued by GL Engeeniring TQS-GPP-RHI-GSP-EL-06238_R00
Изменение 04.5 выполнено ООО "ГЛ ИНЖИНИРИНГ" / Revision 04.5 issued by GL Engeeniring TQS-GPP-RHI-GSP-EL-05944_R00
Изменение 04.4 выполнено ООО "ГЛ ИНЖИНИРИНГ" / Revision 04.3 issued by GL Engeeniring TQS-GPP-RHI-GSP-EL-05227_R00
Изменение 04.3 выполнено ООО "ГЛ ИНЖИНИРИНГ" / Revision 04.3 issued by GL Engineering TQS-GPP-RHI-GSP-EL-05148_R00
Изменение 04.2 выполнено ООО "ГЛ ИНЖИНИРИНГ" / Revision 04.2 issued by GL Engeeniring TQS-GPP-RHI-GSP-EL-04362_R01
Изменение 04.1 выполнено ООО "НЕФТЕГАЗИНЖИНИРИНГ" / Revision 04.1 issued by NGE TQS-GPP-RHI-GSP-EL-04059_R00

Статус Status	Рев. Rev.	Дата Date	Назначение выпуска / Reason for Issue	Разраб. Prepared	Проверил Reviewed	Утвердил Approved
IFC	04	02.12.25	Выпущено для строительства / Issued for Construction	Матвеева	Шилкин	Шилкин
IFC	03H	25.11.24	Выпущено для строительства / Issued for Construction	Матвеева	Шилкин	Мингалеев
IFR	02	30.09.24	Выпущено для рассмотрения / Issued for Review	Матвеева	Шилкин	Мингалеев

ГЛ Инжиниринг
СОГЛАСОВАНО
ГРУППОЙ АВТОРСКОГО НАДЗОРА

ООО «РусХимАльянс»
«В производство работ»
Начальник управления, Управление проектирования ГПЗ и ОЗХ
т/и. Ергалиев

	Stage	Sheet No.	Total sheets
	DDD	1	13

GAS PROCESSING COMPLEX WITHIN UST-LUGA ETHANE-RICH GAS PROCESSING CLUSTER
GAS PROCESSING PLANT AND UTILITIES, INFRASTALCTURE AND OFFSITE PROCESS FACILITIES

G0-D8810BX0
Fire Water Pump Station

General Data

РУСХИМАЛЬЯНС

Изм.	Кол.уч	Лист	№док.	Подп.	Дата
04.6	1	-	06238		27.10.26
04.5	70	-	05944		15.09.26
04.4	1	-	05227		30.06.26
04.3	7	1	05148		01.07.26

GLE-(G0-D8810BX0)-EL-ELOV-ZA-001

Газоперерабатывающий комплекс в составе Комплекса переработки этансодержащего газа в районе поселка Усть-Луга. Газоперерабатывающий завод и Технологические объекты общезаводского хозяйства

Разраб.	Матвеева		02.12.25
Проверил	Шилкин		02.12.25
Нач. сек.	Шилкин		02.12.25
Н. контр.	Старостюк		02.12.25
ГИП	Шилкин		02.12.25


G0-D8810BX0
Насосная станция противопожарного водоснабжения

Стадия	Лист	Листов
P	1	13

Общие данные

НЕФТЕГАЗИНЖИНИРИНГ

Согласовано
Взам. инв. №
Подпись и дата
Инв. № подл

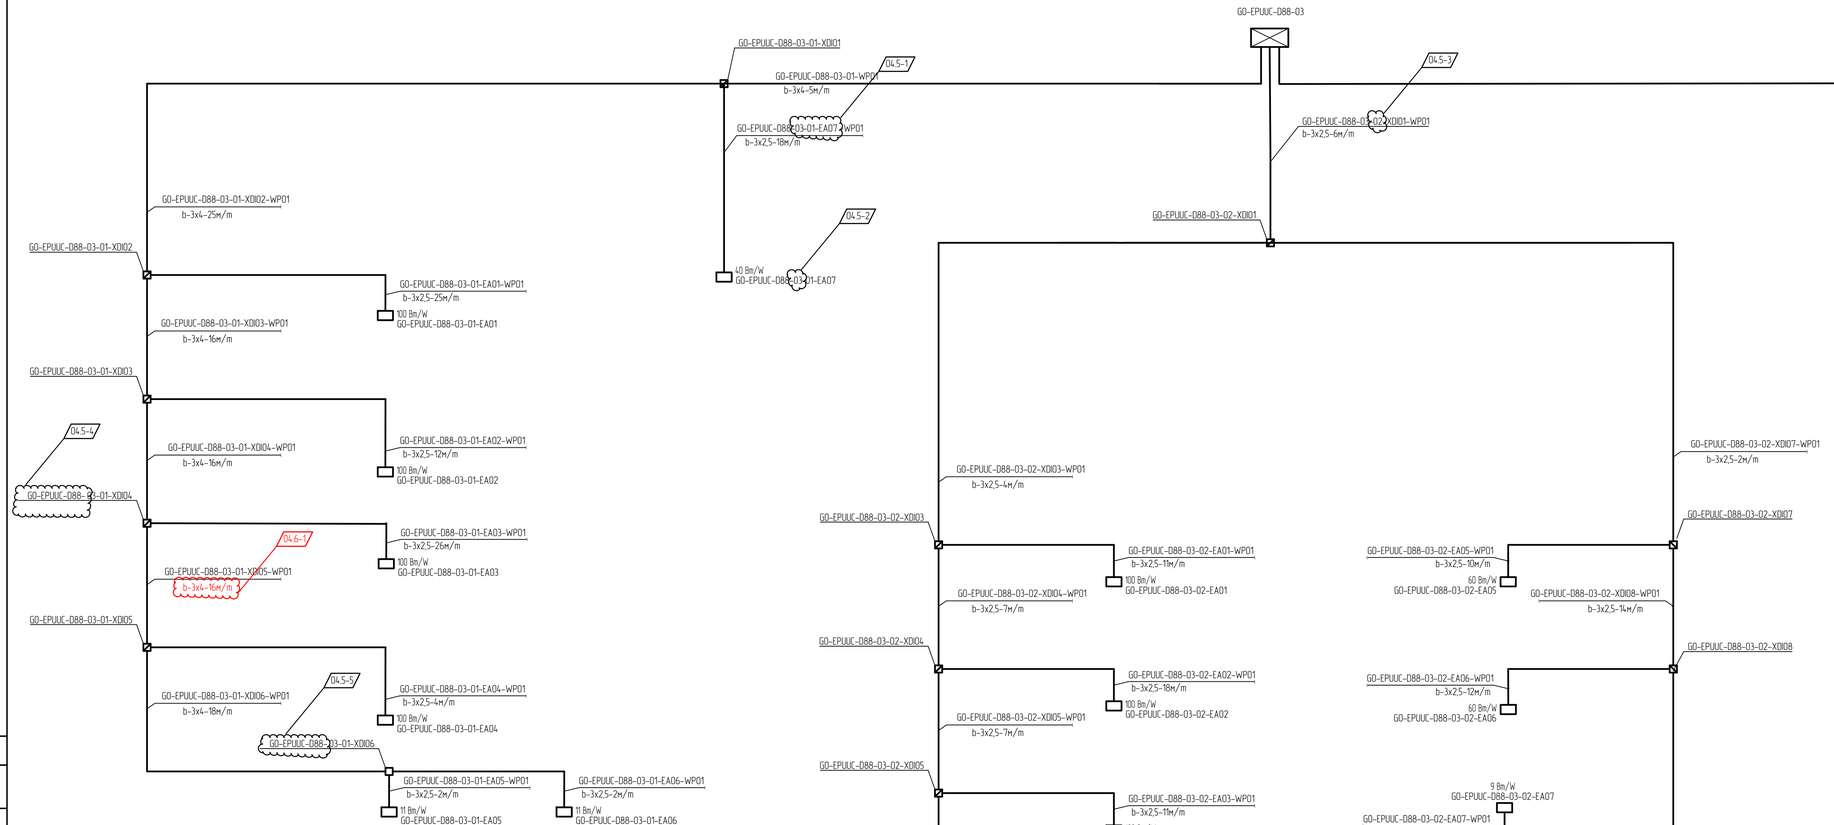

Условные обозначения / Symbols

	Промежуточная соединительная коробка -XDI Intermediate junction box -XDI
	Соединительная коробка светильника -XDE Lighting junction box -XDE
	Светильник светодиодный -EA LED lighting fixture -EA

	код оборудования EA- светильник Equipment code EA- lighting fixture
	XDI- промежуточная коробка XDI- intermediate junction box XDE- соединительная коробка светильника XDE- lighting junction box
	порядковый номер оборудования Equipment sequence number
GO-EPNUC-D88-01-01-XX01	
	номер tmzt оборудования Equipment number (tag)
	номер группы Lighting circuit number
	щит питания Power distribution board
c-3x2,5-6м/m	длина кабельной линии Cable length
	сечение кабеля Cable cross-section
	тип кабеля: c-ВБШВнг(A)-FRLS Cable type: c-ВБШВнг(A)-FRLS
	тип кабеля: d-ВВГнг(A)-FRLS Cable type: d-ВВГнг(A)-FRLS

ООО «РусХимАльянс»

Документ согласован Управлением проектирования ГПЗ и ОЗХ

Изменение 04.6 выполнено ООО "Г/Л ИНЖИНИРИНГ" / Revision 04.6 issued by GL Engineering TQS-GPP-RHI-GSP-EL-06238_R00
Изменение 04.5 выполнено ООО "Г/Л ИНЖИНИРИНГ" / Revision 04.5 issued by GL Engineering TQS-GPP-RHI-GSP-EL-05944_R00

Статус Status	Рев. Rev.	Дата Date	Назначение выпуска / Reason for Issue	Разраб. Drawn	Провер. Checked	Утвердил Approved
IFC	04	02.12.25	Выпущено для строительства / Issued for Construction	Матвеева	Шилкин	Шилкин
IFC	03Н	25.11.24	Выпущено для строительства / Issued for Construction	Матвеева	Шилкин	Мингалеев
IFR	02	30.09.24	Выпущено для рассмотрения / Issued for Review	Матвеева	Шилкин	Мингалеев

04.6	1	-	06238		27.10.26
04.5	5	Зам	05944		15.09.26
Изм.	Колич.	Лист	№док.	Подпись	Дата

Разраб.	Матвеева		02.12.25
Проверил	Шилкин		02.12.25
Нач. сек.	Шилкин		02.12.25
Н. контр.	Старостюк		02.12.25
ГИП	Шилкин		02.12.25

GAS PROCESSING COMPLEX WITHIN UST-LUGA ETHANE-RICH GAS PROCESSING CLUSTER. GAS PROCESSING PLANT AND UTILITIES, INFRASTRUCTURE AND OFFSITE PROCESS FACILITIES

GO-D8810BXO
Fire Water Pump Station

Стадия: DOO | Лист: 8 | Листов:

Block Diagram. Emergency Lighting Panel

РУСХИМАЛЬЯНС

GLE-(GO-D8810BXO)-EL-ELOV-ZA-001

ГАЗОПЕРЕРАБАТЫВАЮЩИЙ КОМПЛЕКС В СОСТАВЕ КОМПЛЕКСА ПЕРЕРАБОТКИ ЭТАНСОДЕРЖАЩЕГО ГАЗА В РАЙОНЕ ПОС. ЛУГА, ГАЗОПЕРЕРАБАТЫВАЮЩИЙ ЗАВОД И ТЕХНОЛОГИЧЕСКИЕ ОБЪЕКТЫ ОБЩЕЗАВОДСКОГО ХОЗЯЙСТВА

GO-D8810BXO
Насосная станция противопожарного водоснабжения

Стадия: P | Лист: 8 | Листов:

Структурная схема щита аварийного освещения

НЕФТЕГАЗИНЖИНИРИНГ

ГЛИ ИНЖИНИРИНГ ПРОЕКТИРУЕМ БУДУЩЕЕ ОТРАСЛИ

СОГЛАСОВАНО

ГРУППОЙ АВТОРСКОГО НАДЗОРА

GLE-(GO-D8810BXO)-EL-ELOV-ZA-001_04_ALDWG

Формат A3x3

Согласовано | Взам. инв. № | Подп. и дата | Инв. № подл.