Общество с ограниченной ответственностью «Газпром Линде Инжиниринг»/
Gazprom Linde Engineering Limited Liability Company

Заказчик – ООО «РусХимАльянс» / Owner - RusChemAlliance LLC

Gas Processing Complex within Ust-Luga Ethane-Rich Gas Processing Cluster. Gas Processing Plant and Utilities, Infrastructure and Offsite Process Facilities

Газоперерабатывающий комплекс в составе Комплекса переработки этансодержащего газа в районе поселка Усть-Луга. Газоперерабатывающий завод и Технологические объекты общезаводского хозяйства

Резервуары противопожарного запаса воды
Fire Water Storage Tanks

Насосная станция противопожарного водоснабжения
Fire Water Pump Station

РАБОЧАЯ ДОКУМЕНТАЦИЯ
DETAIL DESIGN DOCUMENTATION

Проектирование электрической части
Electrical engineering

Электроснабжение. Подстанции.
Схема электрическая принципиальная
Power Supply. Substations. Single Line Diagram

Основной комплект рабочей документации
Main Package of Detail Design Documentation

GLE-(G0-D8810BX0)-EL-ESPS-ZM-001

2026

Общество с ограниченной ответственностью «Газпром Линде Инжиниринг»/
Gazprom Linde Engineering Limited Liability Company

Заказчик – ООО «РусХимАльянс» / Owner - RusChemAlliance LLC

Gas Processing Complex within Ust-Luga Ethane-Rich Gas Processing Cluster. Gas Processing Plant and Utilities, Infrastructure and Offsite Process Facilities

Газоперерабатывающий комплекс в составе Комплекса переработки этансодержащего газа в районе поселка Усть-Луга. Газоперерабатывающий завод и Технологические объекты общезаводского хозяйства

Резервуары противопожарного запаса воды
Fire Water Storage Tanks

Насосная станция противопожарного водоснабжения
Fire Water Pump Station

РАБОЧАЯ ДОКУМЕНТАЦИЯ
DETAIL DESIGN DOCUMENTATION

Проектирование электрической части
Electrical engineering

Электроснабжение. Подстанции.
Схема электрическая принципиальная
Power Supply. Substations. Single Line Diagram

Основной комплект рабочей документации
Main Package of Detail Design Documentation

GLE-(G0-D8810BX0)-EL-ESPS-ZM-001

Главный инженер проекта
Chief Project Engineer

И.В.Трофимов
I.V. Trofimov

2026

Взам. инв. №

Подпись и дата

Инв. № подл

Ведомость рабочих чертежей основного комплекта
List of Detail Drawings of Main Package

Лист Sheet	Наименование	Description	Примечание Note
1-4	**Общие данные** GLE-(G0-D8810BX0)-EL-ESPS-ZM-001_05_AL.pdf GLE-(G0-D8810BX0)-EL-ESPS-ZM-001_05_AL.docx	**General Data** GLE-(G0-D8810BX0)-EL-ESPS-ZM-001_05_AL.pdf GLE-(G0-D8810BX0)-EL-ESPS-ZM-001_05_AL.docx	Рев.05 Rev.05
5	**G0-ENKUC-D88. Схема электрическая однолинейная** GLE-(G0-D8810BX0)-EL-ESPS-ZM-001_05_AL.pdf GLE-(G0-D8810BX0)-EL-ESPS-ZM-001_05_AL.docx	**G0-ENKUC-D88. Single line diagram** GLE-(G0-D8810BX0)-EL-ESPS-ZM-001_05_AL.pdf GLE-(G0-D8810BX0)-EL-ESPS-ZM-001_05_AL.docx	Рев.05 Rev.05
6	**Однолинейная схема электроснабжения 10 кВ** GLE-(G0-D8810BX0)-EL-ESPS-ZM-001_05_AL.pdf GLE-(G0-D8810BX0)-EL-ESPS-ZM-001_05_AL.docx	**Single line diagram power supply 10 kV** GLE-(G0-D8810BX0)-EL-ESPS-ZM-001_05_AL.pdf GLE-(G0-D8810BX0)-EL-ESPS-ZM-001_05_AL.docx	Рев.05 Rev.05
7	**G0-ENNUC-D88-01. Схема электрическая однолинейная** GLE-(G0-D8810BX0)-EL-ESPS-ZM-001_05_AL.pdf GLE-(G0-D8810BX0)-EL-ESPS-ZM-001_05_AL.docx	**G0-ENNUC-D88-01. Single line diagram** GLE-(G0-D8810BX0)-EL-ESPS-ZM-001_05_AL.pdf GLE-(G0-D8810BX0)-EL-ESPS-ZM-001_05_AL.docx	Рев.05 Rev.05

IFC	05	07.07.26	Выпущено для строительства / Issued for Construction	Жалнин	Мамин	Трофимов
IFC	04	10.04.25	Выпущено для строительства / Issued for Construction	Шилкин	Саляхутдинов	Мингалеев
IFC	03	13.12.24	Выпущено для строительства / Issued for Construction	Шилкин	Саляхутдинов	Мингалеев
Статус Status	Рев. Rev.	Дата Date	Назначение выпуска/Reason for Issue	Разраб. Prepared	Проверил Reviewed	Утвердил Approved

Согласовано

Взам. инв. №

Подпись и дата

Инв. № подл

GAS PROCESSING COMPLEX WITHIN UST-LUGA ETHANE-RICH GAS PROCESSING CLUSTER
GAS PROCESSING PLANT AND UTILITIES, INFRASTRUCTURE AND OFFSITE PROCESS FACILITIES

G0-D8810BX0
Fire Water Pump Station

Stage	Sheet No	Total sheets
DDD	1	12

General Data

РУСХИМАЛЬЯНС

GLE-(G0-D8810BX0)-EL-ESPS-ZM-001

Газоперерабатывающий комплекс в составе Комплекса переработки этансодержащего газа в районе поселка Усть-Луга.
Газоперерабатывающий завод и Технологические объекты общезаводского хозяйства

Изм.	Кол.уч	Лист	№ док.	Подп.	Дата
Разраб.		Жалнин			07.07.26
Проверил		Мамин			07.07.26
Нач.сек.		Кругликов			07.07.26
Н. контр.		Любушин			07.07.26
ГИП		Трофимов			07.07.26

G0-D8810BX0 Насосная станция противопожарного водоснабжения

Стадия	Лист	Листов
Р	1	12

Общие данные

ГЛИнжиниринг
ПРОЕКТИРУЕМ БУДУЩЕЕ ОТРАСЛИ

Лист Sheet	Наименование	Description	Примечание Note
8	**G0-EEURB-D88-01. Схема электрическая однолинейная** GLE-(G0-D8810BX0)-EL-ESPS-ZM-001_05_AL.pdf GLE-(G0-D8810BX0)-EL-ESPS-ZM-001_05_AL.docx	**G0-EEURB-D88-01. Single line diagram** GLE-(G0-D8810BX0)-EL-ESPS-ZM-001_05_AL.pdf GLE-(G0-D8810BX0)-EL-ESPS-ZM-001_05_AL.docx	Рев.05 Rev.05
9	**G0-ESNUC-D88-03. Схема электрическая однолинейная** GLE-(G0-D8810BX0)-EL-ESPS-ZM-001_05_AL.pdf GLE-(G0-D8810BX0)-EL-ESPS-ZM-001_05_AL.docx	**G0-ESNUC-D88-03. Single line diagram** GLE-(G0-D8810BX0)-EL-ESPS-ZM-001_05_AL.pdf GLE-(G0-D8810BX0)-EL-ESPS-ZM-001_05_AL.docx	Рев.05 Rev.05
10	**G0-ESNUC-D88-01, G0-ESNUC-D88-02. Принципиальная схема питания сварочного поста** GLE-(G0-D8810BX0)-EL-ESPS-ZM-001_05_AL.pdf GLE-(G0-D8810BX0)-EL-ESPS-ZM-001_05_AL.docx	**G0-ESNUC-D88-01, G0-ESNUC-D88-02. Power Supply Diagram Welding Station** GLE-(G0-D8810BX0)-EL-ESPS-ZM-001_05_AL.pdf GLE-(G0-D8810BX0)-EL-ESPS-ZM-001_05_AL.docx	Рев.05 Rev.05
11	**G0-ENNUC-D88-01. Расчет сечения кабельных линий** GLE-(G0-D8810BX0)-EL-ESPS-ZM-001_05_AL.pdf GLE-(G0-D8810BX0)-EL-ESPS-ZM-001_05_AL.docx	**G0-ENNUC-D88-01. The calculation of the cable lines cross-section** GLE-(G0-D8810BX0)-EL-ESPS-ZM-001_05_AL.pdf GLE-(G0-D8810BX0)-EL-ESPS-ZM-001_05_AL.docx	Рев.05 Rev.05

Взам. инв. №

Подпись и дата

Инв. № подл

Изм.	Кол.уч	Лист	№док	Подпись	Дата

GLE-(G0-D8810BX0)-EL-ESPS-ZM-001

Инв. № подл.	Подп. и дата	Взам. инв. №

GLE-(G0-D8810BX0)-EL-ESPS-ZM-001_05_AL.docx

Изм.		
Кол.уч		
Лист		
№док		
Подпись		
Дата		

GLE-(G0-D8810BX0)-EL-ESPS-ZM-001

Лист	
3	

Ведомость ссылочных и прилагаемых документов
List of Reference and Attached Documents

Обозначение Ident. No.	Наименование	Description	Примечание Note
	Ссылочные документы	Reference documents	
GLE-(G0-Z00300X0)-EL-CU-001	Перечень электрических потребителей	List of electrical consumers	
GLE-(G0-Z00300X0)-EL-ZQ-001	Однолинейная схема	Single line diagram	
GLE-(G0-Z00300X0)-EL-SD-010	Технические требования на источники бесперебойного электропитания (ИБП, СОПТ)	Specification for Uninterruptible Power Supply (UPS, ODCS)	
GSP-(G0-Z00000X0)-DC-PR-004	Процедура тегирования оборудования	Equipment Tagging Procedure	
GLE-(G0-D8810BX0)-EL-ESPS-ZK-001	Насосная станция противопожарного водоснабжения. Электроснабжение. Подстанции. Схемы релейной защиты и автоматики 10 кВ	Fire Water Pump Station. Power Supply Systems. Substations. Protective Diagrams 10 kV	
GLE-(G0-D8810BX0)-EL-ESPS-ZA-001	Насосная станция противопожарного водоснабжения. Электроснабжение. Подстанции. План расположения электрооборудования и кабельных трасс	Fire Water Pump Station. Power Supply Systems. Substations. Equipment Layout and Cable Routing Plan	
GLE-(G0-D8810BX0)-EL-EMSV-ZA-001	Насосная станция противопожарного водоснабжения. Силовое электрооборудование. План расположения электрооборудования и кабельных трасс	Fire Water Pump Station. Power Supply Systems. Substations. Power Installation. Equipment Layout and Cable Routing Plan	

Формат А4

Общие указания

1 Основание для проектирования:

- задание на разработку рабочей документации по объекту строительства «Газоперерабатывающий комплекс в составе Комплекса переработки этансодержащего газа в районе поселка Усть-Луга. Газоперерабатывающий завод и технологические объекты общезаводского хозяйства».

2 Технические решения, принятые в рабочих чертежах, соответствуют требованиям экологических, санитарно-гигиенических, противопожарных, промышленной безопасности и других норм, действующих на территории Российской Федерации, и обеспечивают безопасную для жизни и здоровья людей эксплуатацию объекта при соблюдении предусмотренных рабочими чертежами мероприятий.

3 Рабочая документация разработана в соответствии с требованиями нормативных документов:

- ГОСТ Р 21.101-2020. Национальный стандарт Российской Федерации. Система проектной документации для строительства. Основные требования к проектной и рабочей документации;
- ПУЭ, изд.6,7 – Правила устройства электроустановок;
- ГОСТ 21.210-2014 – Условные графические изображения электрооборудования и проводок на планах;

General Notes

1 Basis of Design:

- Assignment for Detail Design of the construction facility: Gas Processing Complex within Ust-Luga Ethane-Rich Gas Processing Cluster. Gas Processing Plant and Utilities, Infrastructure and Offsite Process Facilities.

2 The design principles in the detail drawings comply with the requirements of environmental, sanitary and hygienic, fire safety, industrial safety, and other standards of the Russian Federation. It also provides that operation of the facility is safe for life and health subject to the measures provided in the detail drawings.

3 Details drawings are developed in accordance with the following regulations:

- GOST R 21.101-2020 National Standard of the Russian Federation. System of Design Documentation for Construction. Main Requirements for Design and Working Documentation;
- Electrical Installations Code (PUE, Edition 6, 7);
- GOST 21.210-2014 Symbols of Electrical Equipment and Wiring on Plans.

Номер ячейки / Cell number	111	110	109	108	107	106	105	104	101	102	103
Обозначение монтажной единицы/ Designation of the mounting unit	W111K	W110K	W109K	W108K	W107K	W106K	-	W104K	Q1	Q3	TW1K
Наименование присоединения / Name of the connection	Насос водяной пожаротушения GO-93PM02A (основной ввод)/ Fire Water Pump GO-93PM02A (Basic input)	Насос водяной пожаротушения GO-93PM02B (основной ввод)/ Fire Water Pump GO-93PM02B (Basic input)	Насос водяной пожаротушения GO-93PM02C (основной ввод)/ Fire Water Pump GO-93PM02C (Basic input)	Устройство плавного пуска GO-93PM-TA01 (основной ввод) / Soft starter GO-93PM-TA01 (Basic input)	Насос водяной пожаротушения GO-93PM02D (основной ввод)/ Fire Water Pump GO-93PM02D (Basic input)	Насос водяной пожаротушения GO-93PM02E (основной ввод)/ Fire Water Pump GO-93PM02E (Basic input)	Резерв/Reserve	Устройство плавного пуска GO-93PM-TA02 (основной ввод) / Soft starter GO-93PM-TA02 (Basic input)	Кабельный ввод №1 /Cable entry №1	Кабельный ввод №3 /Cable entry №3	Трансформатор напряжения TV-01A / Voltage Transformer TV-01A
Пиковая расчетная мощность электроприемников, кВт / Peak rated power of electric receivers, kW	581,0	581,0	581,0	-	581,0	581,0	-	-	2324.00	2324.00	-
Коэффициент мощности cos f /Power factor cos f	0,86	0,86	0,86	-	0,86	0,86	-	-	0,86	0,86	-
Расчетный ток, А / Rated current, A	39,01	39,01	39,01	-	39,01	39,01	-	-	156,02	156,02	-

Номер ячейки / Cell number	-	203	201	202	204	205	206	207	208	209	210	211
Обозначение монтажной единицы/ Designation of the mounting unit	-	TW2K	Q2	Q4	W204K	-	W206K	W207K	W208K	W209K	W210K	W211K
Наименование присоединения / Name of the connection	-	Трансформатор напряжения TV-02A / Voltage Transformer TV-02A	Кабельный ввод №2 /Cable entry №2	Кабельный ввод №4 /Cable entry №4	Устройство плавного пуска GO-93PM-TA02 (резервный ввод) / Soft starter GO-93PM-TA02 (Backup input)	Резерв/Reserve	Насос водяной пожаротушения GO-93PM02E (резервный ввод)/ Fire Water Pump GO-93PM02E (Backup input)	Насос водяной пожаротушения GO-93PM02D (резервный ввод)/ Fire Water Pump GO-93PM02D (Backup input)	Устройство плавного пуска GO-93PM-TA01 (резервный ввод) / Soft starter GO-93PM-TA01 (Backup input)	Насос водяной пожаротушения GO-93PM02C (резервный ввод)/ Fire Water Pump GO-93PM02C (Backup input)	Насос водяной пожаротушения GO-93PM02B (резервный ввод)/ Fire Water Pump GO-93PM02B (Backup input)	Насос водяной пожаротушения GO-93PM02A (резервный ввод)/ Fire Water Pump GO-93PM02A (Backup input)
Пиковая расчетная мощность электроприемников, кВт / Peak rated power of electric receivers, kW	-	-	2324.00	2324.00	-	-	581,0	581,0	-	581,0	581,0	581,0
Коэффициент мощности cos f /Power factor cos f	-	-	0,86	0,86	-	-	0,86	0,86	-	0,86	0,86	0,86
Расчетный ток, А / Rated current, A	-	-	156,02	156,02	-	-	39,01	39,01	-	39,01	39,01	39,01

Тип оборудования указан в качестве аналога. Допускается замена оборудования на аналогичное, с сохранением технических характеристик

The type of equipment is indicated as an analog. It is allowed to replace the equipment with a similar one, while maintaining the technical characteristics

* - см. комплект GLE-(GO-D8810BXO)-ESPS-ZK-001

* - see kit GLE-(GO-D8810BXO)-ESPS-ZK-001

Статус Status	Рев. Rev.	Дата Date	Назначение выпуска / Reason for Issue	Разраб. Drawn	Провер. Checked	Утверд. Approved
IFC	05	07.07.26	Выпущено для строительства / Issued for Construction	Жалнин	Мамин	Трофимов
IFC	04	10.04.25	Выпущено для строительства / Issued for Construction	Шилкин	Саляхутдинов	Мингалеев
IFC	03	13.12.24	Выпущено для строительства / Issued for Construction	Шилкин	Саляхутдинов	Мингалеев

GAS PROCESSING COMPLEX WITHIN UST-LUGA ETHANE-RICH GAS PROCESSING CLUSTER. GAS PROCESSING PLANT AND UTILITIES, INFRASTRUCTURE AND OFFSITE PROCESS FACILITIES

GO-D8810BXO Fire Water Pump Station

GO-ENKUC-D88. Single line diagram

Stage	Sheet	Total Sheets
DDD	5	

РУСХИМАЛЬЯНС

GLE-(GO-D8810BXO)-EL-ESPS-ZM-001

Газоперерабатывающий комплекс в составе Комплекса переработки этансодержащего газа в районе поселка Усть-Луга. Газоперерабатывающий завод и Технологические объекты общезаводского хозяйства

Изм.	Кол.уч.	Лист	№док.	Подпись	Дата
Разраб.		Жалнин			07.07.26
Проверил		Мамин			07.07.26
Нач. сек.		Кругликов			07.07.26
Н. контр.		Любушин			07.07.26
ГИП		Трофимов			07.07.26

GO-D8810BXO Насосная станция противопожарного водоснабжения

Стадия	Лист	Листов
Р	5	

GO-ENKUC-D88. Схема электрическая однолинейная

ГЛИнжиниринг ПРОЕКТИРУЕМ БУДУЩЕЕ ОТРАСЛИ

GLE-(GO-D8810BXO)-EL-ESPS-ZM-001_05_AL.DWG

Формат А2х4

Насосная станция
противопожарного водоснабжения/
Fire Water Pump Station
GO-D8810BX0

Ввод 1 от GO-ENKUC-D48-01A, яч. 114 / Input 1 GO-ENKUC-D48-01A, cell 114 — 05.1

Ввод 3 от GO-EESGA-D88-01-KUC / Input 3 GO-EESGA-D88-01-KUC — 05.2

GO-ENKUC-D88-01A

630 A N.C. — АВР / ATS — 630 A N.O.

TVinc-01C

10 кВ, 50 Гц, 3ф, 1250 А, 50 кА/1с, I секция/
10 kV, 50 Hz, 3ph, 1250 A, 50 kA/1sec, I section

Ввод 2 от GO-ENKUC-D48-01B, яч. 213 / Input 2 GO-ENKUC-D48-01B, cell 213 — 05.3

Ввод 4 от GO-EESGA-D88-01-KUC / Input 4 GO-EESGA-D88-01-KUC — 05.4

GO-ENKUC-D88-01B

10 кВ, 50 Гц, 3ф, 1250 А, 50 кА/1с, II секция/
10 kV, 50 Hz, 3ph, 1250 A, 50 kA/1sec, II section

101 111 110 109 108 102 107 106 105 104 103 — 203 201 204 205 206 207 202 208 209 210 211

630 A

TV-01A — TV-01B

Резерв — Резерв

GO-93PM02A-WP01 Вз-РэБВнг(А)-FRLS-10 3X70/25 — GO-93PO2A Насос водяной пожаротушения/ Fire Water Pump 630 кВт*/kW*

GO-93PM02B-WP01 Вз-РэБВнг(А)-FRLS-10 3X70/25 — GO-93PO2B Насос водяной пожаротушения/ Fire Water Pump 630 кВт*/kW*

GO-93PM02C-WP01 Вз-РэБВнг(А)-FRLS-10 3X70/25 — GO-93PO2C Насос водяной пожаротушения/ Fire Water Pump 630 кВт*/kW*

GO-93PM02D-WP01 Вз-РэБВнг(А)-FRLS-10 3X70/25 — GO-93PO2D Насос водяной пожаротушения/ Fire Water Pump 630 кВт*/kW*

GO-93PM02E-WP01 Вз-РэБВнг(А)-FRLS-10 3X70/25 — GO-93PO2E Насос водяной пожаротушения/ Fire Water Pump 630 кВт*/kW*

GO-93PM-TA01-WP02 – Вз-РэБВнг(А)-FRLS-10 3X70/25
GO-93PM02E-WP02 – Вз-РэБВнг(А)-FRLS-10 3X70/25
GO-93PM02D-WP02 – Вз-РэБВнг(А)-FRLS-10 3X70/25
GO-93PM-TA01-WP02 – Вз-РэБВнг(А)-FRLS-10 3X70/25
GO-93PM02C-WP02 – Вз-РэБВнг(А)-FRLS-10 3X70/25
GO-93PM02B-WP02 – Вз-РэБВнг(А)-FRLS-10 3X70/25
GO-93PM02A-WP02 – Вз-РэБВнг(А)-FRLS-10 3X70/25

GO-93PM02A-TA01-WP01 Вз-РэБВнг(А)-FRLS-10 3X70/25
GO-93PM02B-TA01-WP01 Вз-РэБВнг(А)-FRLS-10 3X70/25
GO-93PM02C-TA01-WP01 Вз-РэБВнг(А)-FRLS-10 3X70/25
GO-93PM-TA01-WP01 Вз-РэБВнг(А)-FRLS-10 3X70/25
GO-93PM02D-TA02-WP01 Вз-РэБВнг(А)-FRLS-10 3X70/25
GO-93PM02E-TA02-WP01 Вз-РэБВнг(А)-FRLS-10 3X70/25
GO-93PM-TA02-WP01 Вз-РэБВнг(А)-FRLS-10 3X70/25

05.5 GO-93PO-TA01 (SS) — Устройство плавного пуска 10 кВ — ШКА2 — ШКА3 — УБПВД — Пусковая шина

05.6 GO-93PO-TA02 (SS) — Устройство плавного пуска 10 кВ — ШКА5 — УБПВД — Пусковая шина

Кабельный журнал см. комплект GLE-(GO-D8810BX0)-EL-EMSV-LC-001
Cable schedule see GLE-(GO-D8810BX0)-EL-EMSV-LC-001

IFC	05	07.07.26	Выпущено для строительства / Issued for Construction	Жалнин	Мамин	Трофимов
IFC	04	10.04.25	Выпущено для строительства / Issued for Construction	Шилкин	Саляхутдинов	Мингалеев
IFC	03	13.12.24	Выпущено для строительства / Issued for Construction	Шилкин	Саляхутдинов	Мингалеев
Статус Status	Рев. Rev.	Дата Date	Назначение выпуска / Reason for Issue	Разраб. Drawn	Провер. Checked	Утвердил. Approved

GAS PROCESSING COMPLEX WITHIN UST-LUGA ETHANE-RICH GAS PROCESSING CLUSTER. GAS PROCESSING PLANT AND UTILITIES, INFRASTRUCTURE AND OFFSITE PROCESS FACILITIES

GO-D8810BX0 Fire Water Pump Station — Stage: DDD — Sheet: 6 — Total Sheets:

Single line diagram power supply 10 kV

РУСХИМАЛЬЯНС

GLE-(GO-D8810BX0)-EL-ESPS-ZM-001

Газоперерабатывающий комплекс в составе Комплекса переработки этансодержащего газа в районе поселка Усть-Луга. Газоперерабатывающий завод и Технологические объекты общезаводского хозяйства

Изм.	Колич.	Лист	№док.	Подпись	Дата
Разраб.		Жалнин			07.07.26
Проверил		Мамин			07.07.26
Нач. сек.		Кругликов			07.07.26
Н. контр.		Любушин			07.07.26
ГИП		Трофимов			07.07.26

GO-D8810BX0 Насосная станция противопожарного водоснабжения — Стадия: P — Лист: 6 — Листов:

Однолинейная схема электроснабжения 10 кВ

ГЛИнжиниринг — ПРОЕКТИРУЕМ БУДУЩЕЕ ОТРАСЛИ

GLE-(GO-D8810BX0)-EL-ESPS-ZM-001_05_AL.DWG

Формат A2

Согласовано | Взам. инв. № | Подп. и дата | Инв. № подл.

Шины сборные 0,4 кВ / Power buses 0,4 kV

Схема силовых частей / Power circuit diagram

Ш1 Ш2

Ш3 Ш4

Ш5 Ш6

Ш7 Ш8

Ш9 Ш10

Ш11 Ш12

Ш13 Ш14

Ш15 Ш16

Ш17 Ш18

Ш19 Ш20

Ш21 Ш22

Ш23 Ш24

Ш25 Ш26

Ш27 Ш28

Ш29 Ш30

Ш31 Ш32

Ш33 Ш34

Ш35 Ш36

Ш37 Ш38

Ш39 Ш40

СИСТЕМА ОПЕРАТИВНОГО ПОСТОЯННОГО ТОКА GO-EEURB-D88-01/ OPERATING DC SYSTEM GO-EEURB-D88-01

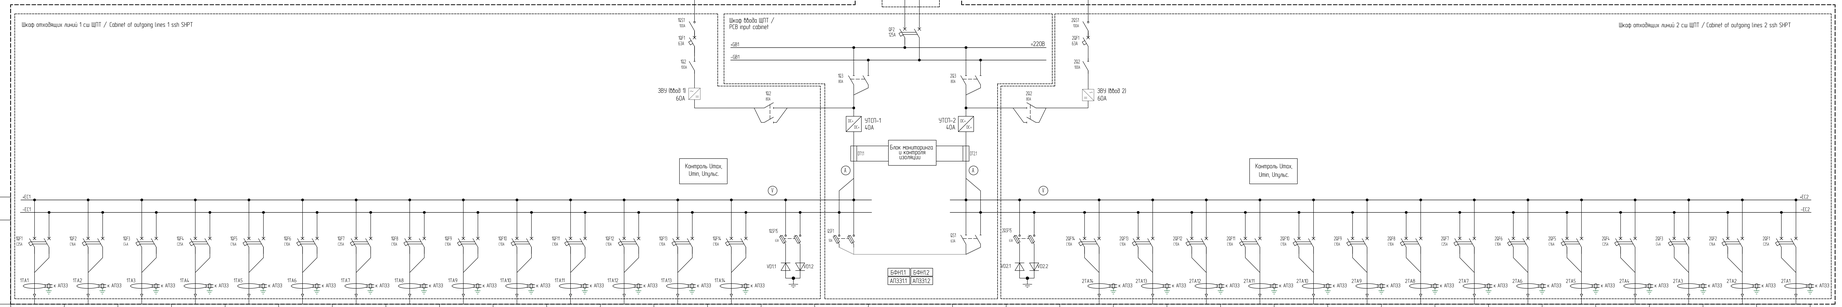

| | | |

GO-ESNUC-D88-03

400 В, 50 Гц, 3ф+N+PE, Iн=100 А, 10кА/1с /400V, 50Hz, 3ph+N+PE, In=100A, 10kA/1sec

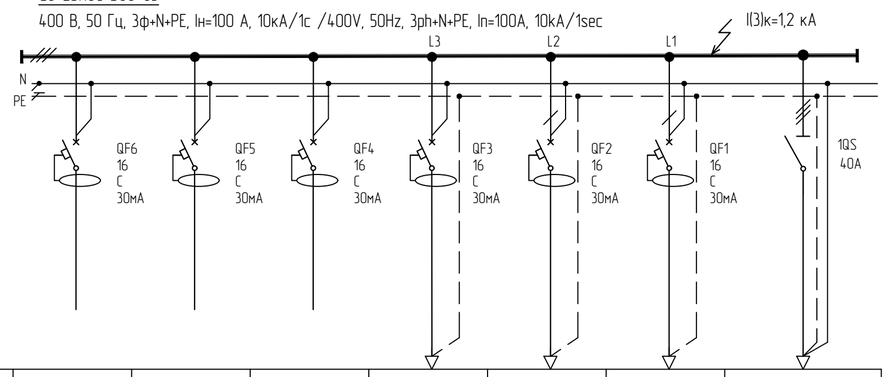

Обозначение коммутационного аппарата / Designation of switching device		QF6	QF5	QF4	QF3	QF2	QF1	1QF
Максимальный ток линии,А / Maximum line current,A		–	–	–	9.62	9.62	9.62	28.87
Расчетный ток линии,А / Rated line current, A		–	–	–	6.80	6.80	6.80	20.40
Расчетная мощность присоединения, кВт / Estimated connection power, kW		–	–	–	4,24	4,24	4,24	12.72
Коэффициент мощности / Power factor		–	–	–	0,9	0,9	0,9	0,9
Установленная мощность присоединения, кВт / Installed connection power, kW		–	–	–	6,0	6,0	6,0	18.00
Тип пускового устройства фидера / Feeder starter type		–	–	–	SF	SF	SF	–
Коммутационный аппарат / Switching device	Тип коммутационного аппарата / Switching device type	АВДТ32	АВДТ32	АВДТ32	АВДТ32	АВДТ32	АВДТ32	ВН-63
	Тип,характеристика расцепителя / Type, characteristics of the release	C	C	C	C	C	C	–
	In, A	10	10	10	10	10	10	63
	Ir, A	–	–	–	–	–	–	–
	Isd, A	–	–	–	–	–	–	–
	tsd, c	–	–	–	–	–	–	–
	Ii, A	–	–	–	–	–	–	–
	Icu, кА	5	5	5	5	5	5	10
	Uн. привода,В / drive,V	–	–	–	–	–	–	–
Присоединение / Connection	Наименование / Name	Резерв/ Reserve	Резерв/ Reserve	Резерв/ Reserve	Розеточная группа 3 Помещение персонала временного пребывания/ Socket group 3 Temporary stay room	Розеточная группа 2 Маш. зал/ Socket group 2 Engine room	Розеточная группа 1 электро-щитовая/ Socket group 1 Switchgear room	Ввод/Input
	Идентификац. номер / Identification number	–	–	–	–	–	–	GO-ENNUC-D88-01A
Кабель / Cable	Марка / Brand	–	–	–	ВБШвнг(А)-LS-1	ВБШвнг(А)-LS-1	ВБШвнг(А)-LS-1	ВВГнг(А)-LS-1
	Сечение /cross-section	–	–	–	3x4	3x4	3x4	5x16
	Маркировка / Marking	–	–	–	GO-ESNUC-D88-03-WP04-L3	GO-ESNUC-D88-03-WP03-L2	GO-ESNUC-D88-03-WP02-L1	GO-ESNUC-D88-03-WP01
Условное графическое обозначение / Conventional graphic symbol								

Тип пускового устройства фидера:
SF – неуправляемый блок субфидеров.

1. Применяются коммутационные аппараты: на вводе 3-х полюсный, на отходящих линиях – 2-х полюсные.
2. Тип оборудования указан в качестве аналога. Допускается замена оборудования на аналогичное, с сохранением технических характеристик.
3. Кабель электроснабжения панели розеток GO-ESNUC-D88-03 учтен в комплекте GLE-(GO-D8810BXO)-EL-EMSV-ZA-001.

Starter feeder type:
SF – Subfeeder Unit, Non-Controlled.

1. Switching devices are used: on incoming feeder – 3-pole, on feeder lines – 2-pole.
2. The type of equipment is indicated as an analog. It is allowed to replace the equipment with a similar one, while maintaining the technical characteristics.
3. The power supply cable for the socket panel GO-ESNUC-D88-03 is included in the GLE-(GO-D8810BXO)-EL-EMSV-ZA-001 kit.

Согласовано

Взам. инв. №

Подп. и дата

Инв. № подл.

IFC	05	07.07.26	Выпущено для строительства / Issued for Construction	Жалнин	Мамин	Трофимов
IFC	04	10.04.25	Выпущено для строительства / Issued for Construction	Шилкин	Саляхутдинов	Мингалеев
IFC	03	13.12.24	Выпущено для строительства / Issued for Construction	Шилкин	Саляхутдинов	Мингалеев
Статус Status	Рев. Rev.	Дата Date	Назначение выпуска / Reason for Issue	Разраб. Drawn	Провер. Checked	Утверд. Approved

GAS PROCESSING COMPLEX WITHIN UST-LUGA ETHANE-RICH GAS PROCESSING CLUSTER. GAS PROCESSING PLANT AND UTILITIES, INFRASTRUCTURE AND OFFSITE PROCESS FACILITIES

GO-D8810BXO
Fire Water Pump Station

GO-ESNUC-D88-03.
Single line diagram

Stage	Sheet	Total Sheets
DDD	9	

РУСХИМАЛЬЯНС

GLE-(GO-D8810BXO)-EL-ESPS-ZM-001

Газоперерабатывающий комплекс в составе Комплекса переработки этансодержащего газа в районе поселка Усть-Луга. Газоперерабатывающий завод и Технологические объекты общезаводского хозяйства

Изм.	Кол.уч.	Лист	№док.	Подпись	Дата
Разраб.		Жалнин			07.07.26
Проверил		Мамин			07.07.26
Нач. сек.		Кругликов			07.07.26
Н. контр.		Любушин			07.07.26
ГИП		Трофимов			07.07.26

GO-D8810BXO Насосная станция противопожарного водоснабжения

Стадия	Лист	Листов
P	9	

GO-ESNUC-D88-03.
Схема электрическая однолинейная

ГЛИнжиниринг
ПРОЕКТИРУЕМ БУДУЩЕЕ ОТРАСЛИ

GLE-(GO-D8810BXO)-EL-ESPS-ZM-001_05_AL.DWG

Формат А2

Источник питания/
Power supply

Ящик силовой / Power box

Аппарат:
выключатель нагрузки:
номер; номинальный ток, А/
Device:
load switch:
number; rated current, A

Предохранитель
номер; номинальный ток, А;
характеристика /
Fuse
number; rated current, A;
characteristic

Проводник / Conductor

Маркировка-расчетная нагрузка, кВт-коэффициент мощности-расчетный ток, А- длина участка, м/
Marking - design load, kW - power factor - design current, A - section length, m

Момент нагрузки, кВт м - потеря напряжения, %- марка,сечение проводника-способ прокладки/
Load moment, kW m - voltage loss, % - brand, conductor cross-section - installation method

Электроприемник / Power receiver

Разъем
для подключения сварочного аппарата
номинальный ток, А /
Connector for connecting a welding machine rated current, A

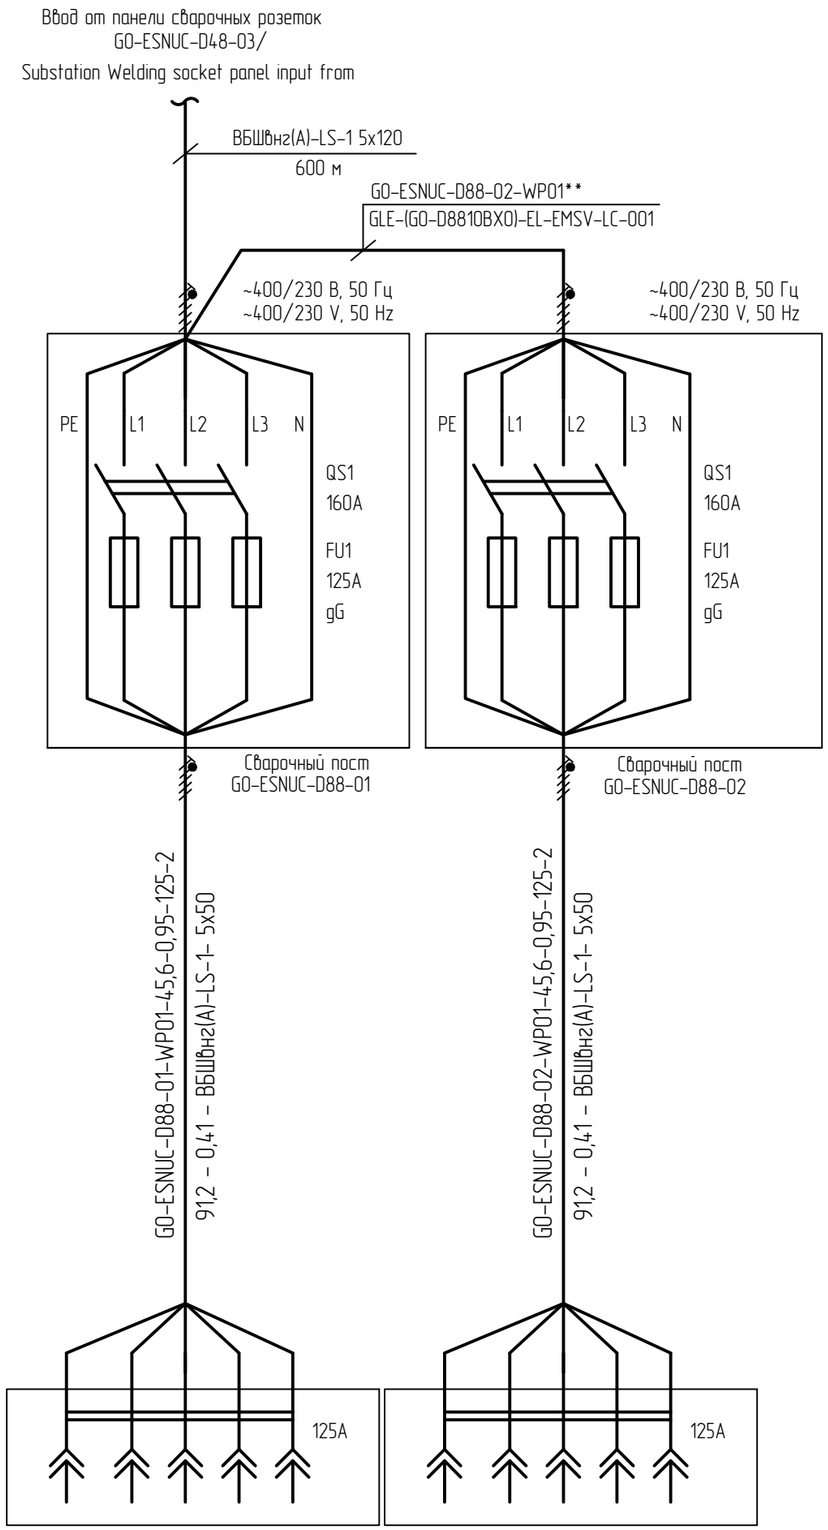

Поз.	Обозначение	Наименование	Кол.	Масса ед., кг	Примечание
		Ящик силовой 600х300х250 (В х Ш х Г),	1		
		металлический, степень защиты IP65, УХЛ1,			
		с клеммами PE, N и замком, оснащен:			
QS1		Выключателем нагрузки трехполюсным,	1		
		номинальный ток 160А			
FU1		Предохранитель с номинальным током 125 А, gG	1		
		Power box 600x300x250 (H x W x D),			
		metal, degree of protection IP65, УХЛ1,			
		with PE and N terminals and lock, equipped with:			
		Three-pole load switch, rated current 160A			
		Fuse with rated current 125 A, gG			

1 Кабель электроснабжения учтен в комплекте GLE-(GO-D4810BX0)-EL-ESPS-ZM-001.
2 Способ прокладки кабеля и монтаж сварочного поста на стойке в соответствии с узлом GLE-(GO-Z000000X0)-EL-ZX-006.022 учтены в комплекте GLE-(GO-D8810BX0)-EL-EMSV-ZA-001.

1 Power supply cable is included in the GLE-(GO-D4810BX0)-EL-ESPS-ZM-001 kit.
2 The method of laying cable and installation of the welding station as per detail shown GLE-(GO-Z000000X0)-EL-ZX-006.022 are taken into account in the set GLE-(GO-D8810BX0)-EL-EMSV-ZA-001.

IFC	05	07.07.26	Выпущено для строительства / Issued for Construction	Жалнин	Мамин	Трофимов
IFC	04	10.04.25	Выпущено для строительства / Issued for Construction	Шилкин	Саляхутдинов	Мингалеев
IFC	03	13.12.24	Выпущено для строительства / Issued for Construction	Шилкин	Саляхутдинов	Мингалеев
Статус Status	Рев. Rev.	Дата Date	Назначение выпуска / Reason for Issue	Разраб. Drawn	Провер. Checked	Утверд. Approved

GAS PROCESSING COMPLEX WITHIN UST-LUGA ETHANE-RICH GAS PROCESSING CLUSTER. GAS PROCESSING PLANT AND UTILITIES, INFRASTRUCTURE AND OFFSITE PROCESS FACILITIES

GO-D8810BX0
Fire Water Pump Station

Stage	Sheet	Total Sheets
DDD	10	

GO-ESNUC-D88-01, GO-ESNUC-D88-02.
Power Supply Diagram Welding Station

РУСХИМАЛЬЯНС

GLE-(GO-D8810BX0)-EL-ESPS-ZM-001

Газоперерабатывающий комплекс в составе Комплекса переработки этансодержащего газа в районе поселка Усть-Луга. Газоперерабатывающий завод и Технологические объекты общезаводского хозяйства

Изм.	Кол.уч.	Лист	№док.	Подпись	Дата
Разраб.		Жалнин			07.07.26
Проверил		Мамин			07.07.26
Нач. сек.		Кругликов			07.07.26
Н. контр.		Любушин			07.07.26
ГИП		Трофимов			07.07.26

GO-D8810BX0 Насосная станция противопожарного водоснабжения

Стадия	Лист	Листов
Р	10	

GO-ESNUC-D88-01, GO-ESNUC-D88-02.
Принципиальная схема питания сварочного поста

ГЛИнжиниринг
ПРОЕКТИРУЕМ БУДУЩЕЕ ОТРАСЛИ

Согласовано

Взам. инв. №

Подп. и дата

Инв. № подл.

GLE-(GO-D8810BX0)-EL-ESPS-ZM-001_05_AL.DWG

Формат А3

Обозначение / Description	Наименование электропотребителей / Electrical Consumer	Рном, кВт	Iрасч, А	Iпуск, А	Iном, А	Kr, A	Ir, A	Ksd, A	Isd, A	I(3)кз, за аппаратом	Тип кабеля	Iдоп, А	Кп	IдопхКп, А	L, м	dU, %	dUn, %	Т нк, °С	Ikmin1, кА	Ikmin2, кА	Ikmin3, кА	Кч1	Кч2	Кч3	Провер. кабеля по Iдоп>Iрасч.	Провер. кабеля по dU и dUp	Провер. кабеля по Тнк<150 °С	Провер. отключ. способн. по Кч
1	2	3	4	5	6	7	8	9	10	11	12	13	14	15	16	17	18	19	20	21	22	23	24	25	26	27	28	29
	G0-ENNUC-D88-01A				**160**	**0,7**	**112**	**3**	**336**																			
G0-97PM10A-MCC-01	Станция управления насосом	4,8	6,42	48,2	40			C	299,2	4,03	5x10	52	0,602	48,2	97	-3,4	-6,8	36,4	0,691	1,05	1,22	2,31	3,51	4,08	Да	Да	Да	Да
G0-97PM10C-MCC-01	Станция управления насосом	11	17,64	132	40			C	299,2	4,03	5x10	52	0,602	60,8	95	-3,68	-12,03	35,5	0,938	1,43	1,65	3,14	4,78	5,51	Да	Да	Да	Да
G0-ESLEB-D88-01	Водонагреватель проточный	2	2,89	-	16			C	119,68	3,42	5x4	34	0,602	20,5	26	-3,21	-3,21	38,5	0,666	1,05	1,21	5,56	8,77	10,11	Да	Да	Да	Да
G0-EPNUC-D88-01	Щит рабочего освещения	2	3,04	-	32			C	239,36	3,42	5x6	43	0,602	25,9	16	-3,12	-3,12	37,5	1,1	1,62	1,86	4,60	6,77	7,77	Да	Да	Да	Да
G0-ESNUC-D88-03	Панель розеток	18	28,9	-	100	0,8	80	5	400	4,03	5x16	80	0,602	48,2	16	-3,33	-3,33	36,6	1,69	2,56	2,96	4,23	6,40	7,40	Да	Да	Да	Да
G0-D8810BX0-SISX-001	Щит распределительный КИТСО	2,5	12,03	-	20			C	149,6	2,08	3x4	34	0,602	20,5	10	-3,85	-3,85	37,2	1,16	1,75	2,02	7,75	11,70	13,50	Да	Да	Да	Да
G0-D8810BX0-CP-1001	УУТЭ узел учета тепловой энергии	1,33	6,4	-	16			C	119,68	2,03	3x2,5	25	0,602	15,06	35	-4,77	-4,77	36,4	0,362	0,581	0,669	3,02	4,85	5,59	Да	Да	Да	Да
G0-ENKUC-D88-01A-BW01	Шинки питания счетчиков в РУ-10 кВ, секция А	0,05	0,241	-	10			C	74,8	1,88	3x2,5	25	0,602	15,06	10	-3,12	-3,12	38,2	0,866	1,27	1,46	11,58	16,98	19,52	Да	Да	Да	Да
G0-ENKUC-D88-01B-BW01-	Шинки питания счетчиков в РУ-10 кВ, секция В	0,05	0,241	-	10			C	74,8	1,88	3x2,5	25	0,602	15,06	10	-3,12	-3,12	38,2	0,866	1,27	1,46	11,58	16,98	19,52	Да	Да	Да	Да
G0-ENKUC-D88-01A-EB01	Шинки антиконденсатного обогрева двигателей 10кВ, секция А	1	4,33	-	10			C	74,8	1,88	3x2,5	25	0,602	15,06	10	-3,16	-3,16	38,2	0,866	1,27	1,46	11,58	16,98	19,52	Да	Да	Да	Да
G0-ENKUC-D88-01A-EB02	Шинки сбогрева ячеек РУ-10 кВ, секция А	1	4,33	-	10			C	74,8	1,88	3x2,5	25	0,602	15,06	10	-3,57	-3,57	38,2	0,866	1,27	1,46	11,58	16,98	19,52	Да	Да	Да	Да
G0-ENKUC-D88-01A-EA01	Освещение ячеек РУ -10 кВ, секция А	0,5	2,41	-	10			C	74,8	1,88	3x2,5	25	0,602	15,06	10	-3,37	-3,37	38,2	0,866	1,27	1,46	11,58	16,98	19,52	Да	Да	Да	Да
G0-93MOV1001	Затвор водопроводный с электроприводом	1,5	2,71	-	10			C	74,8	2,91	4x2,5	25	0,602	15,06	102	-3,85	-3,85	39,2	0,138	0,226	0,261	1,84	3,02	3,49	Да	Да	Да	Да
G0-93MOV1002	Затвор водопроводный с электроприводом	1,5	2,71	-	10			C	74,8	2,91	4x2,5	25	0,602	15,06	94	-3,79	-3,79	39,2	0,149	0,243	0,281	1,99	3,25	3,76	Да	Да	Да	Да
G0-93MOV1003	Затвор водопроводный с электроприводом	1,5	2,71	-	10			C	74,8	2,91	4x2,5	25	0,602	15,06	71	-3,61	-3,61	39,2	0,193	0,313	0,362	2,58	4,18	4,84	Да	Да	Да	Да
G0-93MOV1004	Затвор водопроводный с электроприводом	1,5	2,71	-	10			C	74,8	2,91	4x2,5	25	0,602	15,06	82	-3,7	-3,7	39,2	0,169	0,275	0,318	2,26	3,68	4,25	Да	Да	Да	Да
G0-93MOV1016	Затвор водопроводный с электроприводом	1,5	2,71	-	10			C	74,8	2,91	4x2,5	25	0,602	15,06	71	-3,61	-3,61	39,2	0,193	0,313	0,362	2,58	4,18	4,84	Да	Да	Да	Да
G0-93MOV1017	Затвор водопроводный с электроприводом	1,5	2,71	-	10			C	74,8	2,91	4x2,5	25	0,602	15,06	65	-3,56	-3,56	39,2	0,209	0,339	0,391	2,79	4,53	5,23	Да	Да	Да	Да
G0-93MOV1019	Затвор водопроводный с электроприводом	1,5	2,71	-	10			C	74,8	2,91	4x2,5	25	0,602	15,06	118	-3,98	-3,98	39,2	0,12	0,197	0,228	1,60	2,63	3,05	Да	Да	Да	Да
G0-93MOV1020	Затвор водопроводный с электроприводом	1,5	2,71	-	10			C	74,8	2,91	4x2,5	25	0,602	15,06	100	-3,84	-3,84	39,2	0,141	0,23	0,266	1,89	3,07	3,56	Да	Да	Да	Да
G0-93MOV1021	Затвор водопроводный с электроприводом	1,5	2,71	-	10			C	74,8	2,91	4x2,5	25	0,602	15,06	94	-3,79	-3,79	39,2	0,149	0,243	0,281	1,99	3,25	3,76	Да	Да	Да	Да
G0-93MOV1022	Затвор водопроводный с электроприводом	1,5	2,71	-	10			C	74,8	2,91	4x2,5	25	0,602	15,06	94	-3,79	-3,79	39,2	0,149	0,243	0,281	1,99	3,25	3,76	Да	Да	Да	Да
G0-93MOV1028	Затвор водопроводный с электроприводом	1,2	2,17	-	10			C	74,8	2,91	4x2,5	25	0,602	15,06	62	-3,44	-3,44	39,2	0,218	0,353	0,407	2,91	4,72	5,44	Да	Да	Да	Да
G0-93MOV1029	Затвор водопроводный с электроприводом	1,2	2,17	-	10			C	74,8	2,91	4x2,5	25	0,602	15,06	56	-3,4	-3,4	39,2	0,239	0,385	0,445	3,20	5,15	5,95	Да	Да	Да	Да
G0-96MOV1010	Затвор водопроводный с электроприводом	1	1,8	-	10			C	74,8	2,91	4x2,5	25	0,602	15,06	76	-3,44	-3,44	39,2	0,181	0,295	0,34	2,42	3,94	4,55	Да	Да	Да	Да
G0-96MOV1003	Затвор водопроводный с электроприводом	1	1,8	-	10			C	74,8	2,91	4x2,5	25	0,602	15,06	88	-3,51	-3,51	39,2	0,158	0,258	0,298	2,11	3,45	3,98	Да	Да	Да	Да
G0-D88BX0-NE-01A	Электроконвектор	3	14,43	-	25			C	187	2,13	3x2,5	25	0,602	15,06	13	-4,26	-4,26	36,9	1,03	1,59	1,83	5,51	8,50	9,79	Да	Да	Да	Да
G0-97MOV1009	Затвор водопроводный с электроприводом	1,4	2,53	-	10			C	74,8	2,91	4x2,5	25	0,602	20,5	175	-3,13	-3,13	39,1	0,903	1,34	1,55	12,07	17,91	20,72	Да	Да	Да	Да
G0-97MOV1001	Затвор водопроводный с электроприводом	0,16	0,289	-	10			C	74,8	2,91	4x2,5	25	0,602	20,5	175	-3,04	-3,04	39,1	0,903	1,34	1,55	12,07	17,91	20,72	Да	Да	Да	Да
G0-97PM10A-MCC-01	Блок управления погружным насосом	5,5	8,82	69,9	40			C	299,2	3,42	5x10	52	0,602	20,5	175	-3,34	-7,69	39,9	0,945	1,45	1,67	3,16	4,85	5,58	Да	Да	Да	Да
G0-97PM10C-MCC-01	Блок управления погружным насосом	5,5	8,82	69,9	40			C	299,2	3,42	5x10	52	0,602	20,5	175	-3,34	-7,69	39,9	0,945	1,45	1,67	3,16	4,85	5,58	Да	Да	Да	Да
ИТОГО по G0-ENNUC-D88-01A		**79,19**																										
	G0-ENNUC-D88-01B				**160**	**0,6**	**96**	**3**	**288**																			
G0-97P16B	Станция управления насосом	4,8	6,42	48,2	100	0,4	40	5	200	4,2	5x10	52	0,602	48,2	95	-2,91	-5,75	36,4	0,7	1,07	1,24	3,50	5,35	6,20	Да	Да	Да	Да
G0-97P17A	Станция управления насосом	11	17,64	132	100	0,4	40	5	200	4,2	5x10	52	0,602	60,8	97	-3,2	-10,9	35,6	0,924	1,41	1,63	4,62	7,05	8,15	Да	Да	Да	Да
G0-D8810BX0-JIB	Электрический мостовой кран	12	21,7	-	100	0,4	40	5	200	**4,2**	5x16	80	0,602	48,2	32	-2,94	-2,94	36,4	1,32	2	2,31	6,60	10,00	11,55	Да	Да	Да	Да
G0-D8810BX0-SISX-001	Щит распределительный КИТСО ввод 2	2,5	12,03	-	20			C	149,6	2,18	3x4	34	0,602	20,5	10	-3,19	-3,19	37,4	1,16	1,75	2,01	7,75	11,70	13,44	Да	Да	Да	Да
G0-ENKUC-D88-01A-BW01	Шинки питания счетчиков в РУ-10 кВ, секция А	0,05	0,241	-	10			C	74,8	1,97	3x2,5	25	0,602	15,06	10	-3,02	-3,02	38,6	0,864	1,27	1,46	11,55	16,98	19,52	Да	Да	Да	Да
G0-ENKUC-D88-01B-BW01-	Шинки питания счетчиков в РУ-10 кВ, секция В	0,05	0,241	-	10			C	74,8	1,97	3x2,5	25	0,602	15,06	10	-3,02	-3,02	38,6	0,864	1,27	1,46	11,55	16,98	19,52	Да	Да	Да	Да
G0-ENKUC-D88-01A-EB01	Шинки антиконденсатного обогрева двигателей 10кВ, секция А	1	4,33	-	10			C	74,8	1,97	3x2,5	25	0,602	15,06	10	-2,54	-2,59	38,6	0,864	1,27	1,46	11,55	16,98	19,52	Да	Да	Да	Да
G0-ENKUC-D88-01A-EB02	Шинки сбогрева ячеек РУ-10 кВ, секция А	1	4,33	-	10			C	74,8	1,97	3x2,5	25	0,602	15,06	10	-2,54	-2,59	38,6	0,864	1,27	1,46	11,55	16,98	19,52	Да	Да	Да	Да
G0-ENKUC-D88-01A-EA01	Освещение ячеек РУ -10 кВ, секция А	0,05	2,41	-	10			C	74,8	1,97	3x2,5	25	0,602	15,06	10	-3,23	-3,23	38,6	0,864	1,27	1,46	11,55	16,98	19,52	Да	Да	Да	Да
G0-93MOV1005	Затвор водопроводный с электроприводом	1,5	2,71	-	10			C	74,8	3,04	4x2,5	25	0,602	15,06	79	-3,18	-3,18	39,7	0,175	0,285	0,329	2,34	3,81	4,40	Да	Да	Да	Да
G0-93MOV1006	Затвор водопроводный с электроприводом	1,5	2,71	-	10			C	74,8	3,04	4x2,5	25	0,602	15,06	87	-3,24	-3,24	39,7	0,16	0,261	0,301	2,14	3,49	4,02	Да	Да	Да	Да
G0-93MOV1007	Затвор водопроводный с электроприводом	1,5	2,71	-	10			C	74,8	3,04	4x2,5	25	0,602	15,06	100	-3,33	-3,33	39,7	0,141	0,23	0,265	1,89	3,07	3,54	Да	Да	Да	Да
G0-93MOV1012	Затвор водопроводный с электроприводом	1,5	2,71	-	10			C	74,8	3,04	4x2,5	25	0,602	15,06	118	-3,47	-3,47	39,7	0,12	0,197	0,228	1,60	2,63	3,05	Да	Да	Да	Да
G0-93MOV1013	Затвор водопроводный с электроприводом	1,5	2,71	-	10			C	74,8	3,04	4x2,5	25	0,602	15,06	85	-3,22	-3,22	39,7	0,164	0,267	0,308	2,19	3,57	4,12	Да	Да	Да	Да
G0-93MOV1014	Затвор водопроводный с электроприводом	1,5	2,71	-	10			C	74,8	3,04	4x2,5	25	0,602	15,06	85	-3,22	-3,22	39,7	0,164	0,267	0,308	2,19	3,57	4,12	Да	Да	Да	Да
G0-93MOV1015	Затвор водопроводный с электроприводом	1,5	2,71	-	10			C	74,8	3,04	4x2,5	25	0,602	15,06	77	-3,17	-3,17	39,7	0,179	0,291	0,336	2,39	3,89	4,49	Да	Да	Да	Да
G0-93MOV1023	Затвор водопроводный с электроприводом	1,5	2,71	-	10			C	74,8	3,04	4x2,5	25	0,602	15,06	82	-3,2	-3,2	39,7	0,169	0,275	0,318	2,26	3,68	4,25	Да	Да	Да	Да
G0-93MOV1024	Затвор водопроводный с электроприводом	1,5	2,71	-	10			C	74,8	3,04	4x2,5	25	0,602	15,06	76	-3,16	-3,16	39,7	0,181	0,295	0,34	2,42	3,94	4,55	Да	Да	Да	Да
G0-93MOV1025	Затвор водопроводный с электроприводом	1,2	2,17	-	10			C	74,8	3,04	4x2,5	25	0,602	15,06	74	-3,03	-3,03	39,7	0,186	0,302	0,348	2,49	4,04	4,65	Да	Да	Да	Да
G0-93MOV1026	Затвор водопроводный с электроприводом	1,2	2,17	-	10			C	74,8	3,04	4x2,5	25	0,602	15,06	80	-3,06	-3,06	39,7	0,173	0,282	0,325	2,31	3,77	4,34	Да	Да	Да	Да
G0-93MOV1027	Затвор водопроводный с электроприводом	1,2	2,17	-	10			C	74,8	3,04	4x2,5	25	0,602	15,06	68	-2,99	-2,99	39,7	0,201	0,325	0,375	2,69	4,34	5,01	Да	Да	Да	Да
G0-96MOV1011	Затвор водопроводный с электроприводом	1	1,8	-	10			C	74,8	3,04	4x2,5	25	0,602	15,06	76	-2,96	-2,96	39,7	0,181	0,295	0,34	2,42	3,94	4,55	Да	Да	Да	Да
G0-96MOV1004	Затвор водопроводный с электроприводом	1	1,8	-	10			C	74,8	3,04	4x2,5	25	0,602	15,06	71	-2,94	-2,94	39,7	0,193	0,313	0,361	2,58	4,18	4,83	Да	Да	Да	Да
G0-D88BX0-NE-01B	Электроконвектор	3	14,43	-	25			C	187	2,22	3x2,5	25	0,602	15,06	15	-4,94	-4,94	37,9	0,703	1,09	1,26	3,76	5,83	6,74	Да	Да	Да	Да
G0-97MOV1010	Затвор водопроводный с электроприводом	1,4	2,53	-	10			C	74,8	3,04	4x2,5	25	0,602	20,5	175	-2,66	-2,66	39,6	0,9	1,34	1,54	12,03	17,91	20,59	Да	Да	Да	Да
G0-97MOV1002	Затвор водопроводный с электроприводом	0,16	0,289	-	10			C	74,8	3,04	4x2,5	25	0,602	20,5	175	-2,58	-2,58	39,6	0,9	1,34	1,54	12,03	17,91	20,59	Да	Да	Да	Да
G0-97PM10B-MCC-01	Блок управления погружным насосом	5,5	8,82	69,9	40			C	299,2	3,57	5x10	52	0,602	20,5	175	-2,86	-6,65	40,4	0,943	1,45	1,67	3,15	4,85	5,58	Да	Да	Да	Да
G0-97PM10D-MCC-01	Блок управления погружным насосом	5,5	8,82	69,9	40			C	299,2	3,57	5x10	52	0,602	20,5	175	-2,86	-6,65	40,4	0,943	1,45	1,67	3,15	4,85	5,58	Да	Да	Да	Да
ИТОГО по G0-ENNUC-D88-01B		**67,11**																										
Общая мощность G0-ENNUC-D88-01A/B																												

Согласовано

Взам. инв. №

Подп. и дата

Инв. № подл.

IFC	05	07.07.26	Выпущено для строительства / Issued for Construction	Халлин	Мамин	Трофимов
IFC	04	10.04.25	Выпущено для строительства / Issued for Construction	Шилкин	Саляхутдинов	Мингалеев
IFC	03	13.12.24	Выпущено для строительства / Issued for Construction	Шилкин	Саляхутдинов	Мингалеев
Статус Status	Рев. Rev.	Дата Date	Назначение выпуска / Reason for Issue	Разраб. Drawn	Провер. Checked	Утверд. Approved

GAS PROCESSING COMPLEX WITHIN UST-LUGA ETHANE-RICH GAS PROCESSING CLUSTER. GAS PROCESSING PLANT AND UTILITIES, INFRASTRUCTURE AND OFFSITE PROCESS FACILITIES

G0-D8810BX0
Fire Water Pump Station

Stage	Sheet	Total Sheets
DDD	11	

G0-ENNUC-D88-01.
The calculation of the cable lines cross-section

РУСХИМАЛЬЯНС

GLE-(G0-D8810BX0)-EL-ESPS-ZM-001

Газоперерабатывающий комплекс в составе Комплекса переработки этансодержащего газа в районе поселка Усть-Луга. Газоперерабатывающий завод и Технологические объекты общезаводского хозяйства

Изм.	Колуч.	Лист	№док.	Подпись	Дата
Разраб.		Халлин			07.07.26
Проверил		Мамин			07.07.26
Нач. сек.		Кругликов			07.07.26
Н. контр.		Любушин			07.07.26
ГИП		Трофимов			07.07.26

G0-D8810BX0 Насосная станция противопожарного водоснабжения

Стадия	Лист	Листов
Р	11	

G0-ENNUC-D88-01.
Расчет сечения кабельных линий

ГЛИнжиниринг
ПРОЕКТИРУЕМ БУДУЩЕЕ ОТРАСЛИ

GLE-(G0-D8810BX0)-EL-ESPS-ZM-001_05_AL.DWG

Формат А2

Лист регистрации изменений

Статус	Рев.	Место изменения	Краткое описание изменений
IFC	05	Лист 8	Изменение внесено на основании DCR-GPP-GLE-GSP-EL-01057-REV00
IFC	05	Листы 5, 6	Изменение внесено на основании TQS-GPP-GSP-RCA-EL-02810_R00
IFC	05	Лист 7	Изменение внесено на основании TQS-GPP-GSP-RCA-EL-02810_R00, TQS-GPP-RHI-GSP-EL-04438_R00

Revision Change Details

Status	Rev.	Location of Changes	Brief Description of Changes
IFC	05	Sheet 8	Corrected according to the DCR-GPP-GLE-GSP-EL-01057-REV00
IFC	05	Sheets 5, 6	Corrected according to the TQS-GPP-GSP-RCA-EL-02810_R00
IFC	05	Sheet 7	Corrected according to the TQS-GPP-GSP-RCA-EL-02810_R00, TQS-GPP-RHI-GSP-EL-04438_R00