Общество с ограниченной ответственностью «Газпром Линде Инжиниринг»/
Gazprom Linde Engineering Limited Liability Company

Заказчик – ООО «РусХимАльянс»/ Owner - RusChemAlliance LLC

Gas Processing Complex within Ust-Luga Ethane-Rich Gas Processing Cluster.
Gas Processing Plant and Utilities, Infrastructure and Offsite Process Facilities

Газоперерабатывающий комплекс в составе Комплекса переработки этансодержащего газа в районе поселка Усть-Луга.
Газоперерабатывающий завод и Технологические объекты общезаводского хозяйства

Резервуары противопожарного запаса воды
Fire Water Storage Tanks

Насосная станция противопожарного водоснабжения
Fire Water Pump Station

РАБОЧАЯ ДОКУМЕНТАЦИЯ
DETAIL DESIGN DOCUMENTATION

Проектирование КИПиА
Instrumentation Engineering

Система контроля загазованности (СКЗ)
Automatic Gas detection system

Основной комплект рабочей документации
Main Package of Detail Design Documentation

GLE-(G0-D8810BX0)-IN-GDSS-001

2025

Общество с ограниченной ответственностью «Газпром Линде Инжиниринг»/
Gazprom Linde Engineering Limited Liability Company

ГЛИнжиниринг
ПРОЕКТИРУЕМ БУДУЩЕЕ ОТРАСЛИ

Заказчик – ООО «РусХимАльянс» / Owner - RusChemAlliance LLC

Gas Processing Complex within Ust-Luga Ethane-Rich Gas Processing Cluster. Gas Processing Plant and Utilities, Infrastructure and Offsite Process Facilities

Газоперерабатывающий комплекс в составе Комплекса переработки этансодержащего газа в районе поселка Усть-Луга. Газоперерабатывающий завод и Технологические объекты общезаводского хозяйства

Резервуары противопожарного запаса воды
Fire Water Storage Tanks

Насосная станция противопожарного водоснабжения
Fire Water Pump Station

РАБОЧАЯ ДОКУМЕНТАЦИЯ
DETAIL DESIGN DOCUMENTATION

Проектирование КИПиА
Instrumentation Engineering

Система контроля загазованности (СКЗ)
Automatic Gas detection system

Основной комплект рабочей документации
Main Package of Detail Design Documentation

GLE-(G0-D8810BX0)-IN-GDSS-001

Главный инженер проекта
Chief Project Engineer

ИНН 0266023912
ОГРН 1040203382845

И. В. Трофимов
I. V. Trofimov

2025

Взам. инв. №	
Подпись и дата	
Инв. № подл	

Ведомость рабочих чертежей основного комплекта
List of Detail Drawings of Main Package

Лист Sheet	Наименование	Description	Примечание Note
1-7	**Общие данные** GLE-(G0-D8810BX0)-IN-GDSS-001_03_AL.pdf GLE-(G0-D8810BX0)-IN-GDSS-001_03_AL.docx	**General Data** GLE-(G0-D8810BX0)-IN-GDSS-001_03_AL.pdf GLE-(G0-D8810BX0)-IN-GDSS-001_03_AL.docx	Рев.03 Rev.03
8-9	**Перечень материалов** GLE-(G0-D8810BX0)-IN-GDSS-001_03_AL.pdf GLE-(G0-D8810BX0)-IN-GDSS-001_03_AL.dwg	**List of Materials** GLE-(G0-D8810BX0)-IN-GDSS-001_03_AL.pdf GLE-(G0-D8810BX0)-IN-GDSS-001_03_AL.dwg	Рев.03 Rev.03
10-11	**Планы расположения КИПиА и прокладки кабельных трасс на отм. 0,000; -3,000** GLE-(G0-D8810BX0)-IN-GDSS-001_03_AL.pdf GLE-(G0-D8810BX0)-IN-GDSS-001_03_AL.dwg	**Instrument and Cable Routing Plans at el. 0,000; –3,000** GLE-(G0-D8810BX0)-IN-GDSS-001_03_AL.pdf GLE-(G0-D8810BX0)-IN-GDSS-001_03_AL.dwg	Рев.03 Rev.03
12-14	**Схемы внешних соединений** GLE-(G0-D8810BX0)-IN-GDSS-001_03_AL.pdf GLE-(G0-D8810BX0)-IN-GDSS-001_03_AL.dwg	**External Wiring Diagrams** GLE-(G0-D8810BX0)-IN-GDSS-001_03_AL.pdf GLE-(G0-D8810BX0)-IN-GDSS-001_03_AL.dwg	Рев.03 Rev.03

Согласовано

Взам. инв. №

Подпись и дата

Инв. № подл

Статус Status	Рев. Rev.	Дата Date	Назначение выпуска/Reason for Issue	Разраб. Prepared	Проверил Reviewed	Утвердил Approved
IFC	03	04.12.25	Выпущено для строительства / Issued for Construction	Поминова	Тулба	Трофимов
IFC	02H	21.03.25	Выпущено для строительства / Issued for Construction	Шевцова	Охота	Подземельнов
IFR	01H	23.08.24	Выпущено для рассмотрения / Issued for Review	Гайсина	Гильманова	Трофимов

GAS PROCESSING COMPLEX WITHIN UST-LUGA ETHANE-RICH GAS PROCESSING CLUSTER GAS PROCESSING PLANT AND UTILITIES, INFRASTRUCTURE AND OFFSITE PROCESS FACILITIES	G0-D8810BX0 Fire Water Pump Station	Stage	Sheet No	Total sheets
		DDD	1	17
	General Data	РУСХИМАЛЬЯНС		

GLE-(G0-D8810BX0)-IN-GDSS-001

Газоперерабатывающий комплекс в составе Комплекса переработки этансодержащего газа в районе поселка Усть-Луга.
Газоперерабатывающий завод и Технологические объекты общезаводского хозяйства

Изм.	Кол.уч	Лист	№ док.	Подп.	Дата
Разраб.		Поминова			04.12.25
Проверил		Тулба			04.12.25
Нач. сект.		Савчук			04.12.25
Н. контр.		Тулба			04.12.25
ГИП		Трофимов			04.12.25

	Стадия	Лист	Листов
G0-D8810BX0 Насосная станция противопожарного водоснабжения	П	1	17
Общие данные	ГЛИнжиниринг ПРОЕКТИРУЕМ БУДУЩЕЕ ОТРАСЛИ		

Лист Sheet	Наименование	Description	Примечание Note
15-16	**Кабельный журнал** GLE-(G0-D8810BX0)-IN-GDSS-001_03_AL.pdf GLE-(G0-D8810BX0)-IN-GDSS-001_03_AL.xlsx	**Cable Schedule** GLE-(G0-D8810BX0)-IN-GDSS-001_03_AL.pdf GLE-(G0-D8810BX0)-IN-GDSS-001_03_AL.xlsx	Рев.03 Rev.03

Взам. инв. №

Подпись и дата

Инв. № подл

						GLE-(G0-D8810BX0)-IN-GDSS-001	Лист
Изм.	Кол.уч	Лист	№док	Подпись	Дата		2

Ведомость ссылочных и прилагаемых документов
List of Reference and Attached Documents

Обозначение Ident. No.	Наименование	Description	Примечание Note
	Ссылочные документы	Reference Documents	
GLE-(G0-Z00000X0)-IN-ZX-001	Схемы электромонтажные КИПиА	Electrical Wiring Diagrams for Instrumentation	
GLE-(G0-Z00000X0)-IN-ZX-002	Схемы монтажа КИПиА механические	Mechanical Instrumentation Hook-Up Drawings	
GLE-(G0-D8810BX0)-IN-ATHP-ZA-001	Планы расположения КИПиА и прокладки кабельных трасс	Instrument and Cable Routing Plans	
GLE-(G0-D8810BX0)-IN-ATHP-SF-001	Спецификация оборудования, изделий и материалов	Material Take-Off (MTO)	
GLE-(G0-Z00000X0)-IN-SQ-004	Концепция заземления КИПиА	I&C Earthing Concept	
GLE-(G0-Z00000X0)-IN-SQ-001	Базовая концепция КИПиА	I&C Basic Concept	
GLE-(G0-Z00000X0)-IN-SD-030	Технические требования на КИПиА	Specification for Instrumentation	
GLE-(G0-Z00000X0)-IN-SD-022	Технические требования на кабели КИПиА	Specification for Instrument Cables	
GLE-(G0-Z00000X0)-IN-SD-025	Технические требования на клеммные коробки КИПиА	Specification for I&C Junction Boxes	
GLE-(G0-Z00000X0)-FA-SD-001	Технические требования к контролю загазованности	Specification for Gas Detection System (GDS)	
GLE-(G0-Z00000X0)-IN-SQ-003	Концепция монтажа КИПиА	I&C Installation Concept	

Инв. № подл.	Подп. и дата	Взам. инв. №

Обозначение Ident. No.	Наименование	Description	Примечание Note
ОБ ОПО Изм. 2 / Rev. 2	Обоснование безопасности опасного производственного объекта «Газоперерабатывающий завод» в рамках проектной документации «Газоперерабатывающий комплекс в составе Комплекса переработки этаносодержащего газа в районе поселка Усть-Луга. Этапы 2.1, 2.4,3.1,3.2,3.3,3.4. Газоперерабатывающий завод»	Hazardous Production Facility Safety Case for Gas Processing Plant as part of PD for Gas Processing Complex within Ust-Luga Ethane-Rich Gas Processing Cluster. Stages 2.1, 2.4, 3.1, 3.2, 3.3, 3.4. Gas Processing Plant	
	Прилагаемые документы	Attached documents	
GLE-(G0-D8810BX0)-IN-GDSS-SF-001 (21 листов / 21 sheets)	Спецификация оборудования, изделий и материалов GLE-(G0-D8810BX0)-IN-GDSS-SF-001_03_AL.pdf GLE-(G0-D8810BX0)-IN-GDSS-SF-001_03_AL.xlsx	Material Take-Off (MTO) GLE-(G0-D8810BX0)-IN-GDSS-SF-001_03_AL.pdf GLE-(G0-D8810BX0)-IN-GDSS-SF-001_03_AL.xlsx	Рев.03 Rev.03

Общие указания

1 Основание для проектирования:

– задание на разработку рабочей документации по объекту строительства «Газоперерабатывающий комплекс в составе Комплекса переработки этансодержащего газа в районе поселка Усть-Луга. Газоперерабатывающий завод и технологические объекты общезаводского хозяйства».

2 Технические решения, принятые в рабочих чертежах, соответствуют требованиям экологических, санитарно-гигиенических, противопожарных, промышленной безопасности и других норм, действующих на территории Российской Федерации, и обеспечивают безопасную для жизни и здоровья людей эксплуатацию объекта при соблюдении предусмотренных рабочими чертежами мероприятий.

3 Рабочая документация разработана в соответствии с требованиями нормативных документов:

– ГОСТ Р 21.101-2020. Национальный стандарт Российской Федерации. Система проектной документации для строительства. Основные требования к проектной и рабочей документации;

– ГОСТ Р 21.210-2014.Система проектной документации для строительства. Условные графические изображения электрооборудования и проводок на планах;

– ГОСТ Р 21.408-2013 Система проектной документации для строительства. Правила выполнения рабочей документации автоматизации технологических процессов;

– СТУ на проектирование и строительство в части обеспечения пожарной безопасности объекта защиты «Газоперерабатывающий комплекс в составе Комплекса переработки этансодержащего газа в районе поселка Усть-Луга»;

General Notes

1 Basis of Design:

– Assignment for detail design for Gas Processing Complex within Ust-Luga Ethane-Rich Gas Processing Cluster. Gas Processing Plant and Utilities, Infrastructure and Offsite Process Facilities.

2 The design principles in the detail drawings comply with the requirements of environmental, sanitary and hygienic, fire safety, industrial safety, and other standards valid over the territory of the Russian Federation. They ensure that the operation of the facility is safe for life and health of people provided the activities prescribed by the detail drawings are followed.

3 Detail drawings are developed in accordance with the following regulations:

– GOST R 21.101-2020 *National Standard of the Russian Federation. System of Design Documentation for Construction. Main Requirements for Design and Working Documentation*

– GOST R 21.210-2014 *System of Design Documents for Construction. Graphic Symbols of Electrical Equipment and Wiring on Plans*

– GOST R 21.408-2013 *System of Design Documents for Construction. Rules of Industrial Process Automation Working Documentation Execution*

– Fire Safety PSTS for Design and Construction of Gas Processing Complex within Ust-Luga Ethane-Rich Gas Processing Cluster

- ОБ ОПО Изм. 2 Обоснование безопасности опасного производственного объекта «Газоперерабатывающий завод» в рамках проектной документации «Газоперерабатывающий комплекс в составе Комплекса переработки этаносодержащего газа в районе поселка Усть-Луга. Этапы 2.1, 2.4,3.1,3.2,3.3,3.4. Газоперерабатывающий завод»
- GLE-(G0-Z00000X0)-IN-SQ-004. Концепция заземления КИПиА;
- GLE-(G0-Z00000X0)-IN-SQ-001. Базовая концепция КИПиА;
- GLE-(G0-Z00000X0)-IN-SD-030. Технические требования на КИПиА;
- GLE-(G0-Z00000X0)-IN-SD-022. Технические требования на кабели КИПиА;
- GLE-(G0-Z00000X0)-IN-SD-025 Технические требования на клеммные коробки КИПиА;
- GLE-(G0-Z00000X0)-IN-SQ-003 Концепция монтажа КИПиА;
- GLE-(G0-Z00000X0)-FA-SQ-003 Концепция обнаружения загазованности и пожара для комплектных установок.

4 Данным проектом предусматривается система контроля загазованности G0-D8810BX0 насосной станции противопожарного водоснабжения.

5 Монтаж приборов и средств автоматизации выполнить согласно строительным нормам и правилам СП 77.13330.2016, GLE-(G0-Z00000X0)-IN-SQ-003, GLE-(G0-Z00000X0)-IN-ZX-001, GLE-(G0-Z00000X0)-IN-ZX-002. Монтаж и разводку кабелей выполнить в соответствии с ПУЭ, СП 77.13330.2016, GLE-(G0-Z00000X0)-IN-SQ-003, GLE-(G0-Z00000X0)-EL-ZX-002 и другими действующими НТД. При монтаже приборов и средств автоматизации дополнительно руководствоваться паспортами и инструкциями (по эксплуатации и монтажу).

- Safety Case (Rev. 2): Hazardous Production Facility Safety Case for Gas Processing Plant as part of PD for Gas Processing Complex within Ust-Luga Ethane-Rich Gas Processing Cluster. Stages 2.1, 2.4, 3.1, 3.2, 3.3, 3.4. Gas Processing Plant
- GLE-(G0-Z00000X0)-IN-SQ-004 *I&C Earthing Concept*
- GLE-(G0-Z00000X0)-IN-SQ-001 *I&C Basic Concept*
- GLE-(G0-Z00000X0)-IN-SD-030 *Specification for Instrumentation*
- GLE-(G0-Z00000X0)-IN-SD-022 *Specification for Instrument Cables*
- GLE-(G0-Z00000X0)-IN-SD-025 *Specification I&C Junction Boxes*
- GLE-(G0-Z00000X0)-IN-SQ-003 *I&C Installation Concept*
- GLE-(G0-Z00000X0)-FA-SQ-003 *Gas and Fire Detection Concept for Package Units*

4 This document provides for Gas Detection System of G0-D8810BX0 Fire Water Pump Station.

5 Instrument and control installation shall be performed in accordance with SP 77.13330.2016, GLE-(G0-Z00000X0)-IN-SQ-003, GLE-(G0-Z00000X0)-IN-ZX-001, GLE-(G0-Z00000X0)-IN-ZX-002. Cables shall be installed and routed in accordance with PUE, SP 77.13330.2016, GLE-(G0-Z00000X0)-IN-SQ-003, GLE-(G0-Z00000X0)-EL-ZX-002 and other applicable codes and standards. Passports and manuals (for operation and installation) shall be followed when installing instruments and controls.

6 Все электромонтажные работы выполнять в соответствии с ПУЭ, изд.6,7, СП 76.13330.2016.

7 При выполнении работ по данному проекту должны быть составлены акты освидетельствования скрытых работ на антикоррозийную обработку сварных соединений.

6 All electrical installation works shall be performed in accordance with PUE (Edition 6, 7), SP 76.13330.2016.

7 Works under this project require the issuance of Hidden Works Certificates for anti-corrosion treatment of welded joints.

Перечень материалов

Поз.	Обозначение	Наименование	Кол.	Масса ед, кг	Примечание
1	EWIRE00055	Провод установочный с медной луженной жилой ПуГВнг(А)-LS 1х6 гибкий, с изоляцией из ПВХ пластиката, не распространяющий горение при групповой прокладке по категории А, с пониженным дымо- и газовыделением; стойкий к воздействию ультрафиолетового излучения; температура окружающей среды от минус 43,2 до плюс 34,7 °С при эксплуатации; минимальная температура прокладки кабеля без предварительного подогрева - минус 15 °С; желто-зеленый; ГОСТ 31947-2012; Срок службы не менее 25 лет.	110	м/m	
2	EWIRE00058	Провод установочный с медной луженной жилой ПуГВнг(А)-LS 1х25 гибкий, с изоляцией из ПВХ пластиката, не распространяющий горение при групповой прокладке по категории А, с пониженным дымо- и газовыделением; стойкий к воздействию ультрафиолетового излучения; температура окружающей среды от минус 43,2 до плюс 34,7 °С при эксплуатации; минимальная температура прокладки кабеля без предварительного подогрева - минус 15 °С; желто-зеленый; ГОСТ 31947-2012; Срок службы не менее 25 лет.	80	м/m	
3	ECHNN00078	Швеллер; перфорированный; 80х40 мм (ШхВ); 1800 мм (Д); сталь; толщина металла: 4,5 мм; горячее цинкование по ГОСТ 9.307-2021, УХЛ1 (толщина цинкового покрытия 85 мкм)	4	шт/psc	для КМ211-31
4	EEARL00001	Шина заземления медная луженая; на 3 подключения М6 под провод сечением 6 мм2; ширина 40 мм; минимальная толщина металла 4 мм; климатическое исполнение и категория размещения У1 по ГОСТ 15150-69, температура эксплуатации от -43,2 до +34,7 °С; в комплекте метизы (термодиффузионное цинкование 40-50 мкм по ГОСТ Р 9.316-2006 или аналог): крепеж шины (болты с шестигранной головкой М10х30, шайбы плоские и пружинные М10, гайки шестигранные М10), крепеж для подключений (болты с шестигранной головкой М6х20, шайбы плоские и пружинные М6, гайки шестигранные М6)	2	шт/psc	
5	EPPRC00001	Стойка трубная DN50; высота 1800 мм; материал: сталь; мин. толщина металла 3,5 мм; горячее цинкование по ГОСТ 9.307-2021; толщина цинкового покрытия 85 мкм; У1; температура эксплуатации от минус 43,2 до плюс 34,7 °С; в комплекте: основание 210х210 мм для крепления к полу (4 отв. диаметром 11 мм), пластина заземления (отв. диаметром 11 мм), защитный колпачок	4	шт/psc	для КМ112-22
6	EPROC00013	Профиль С-образный; перфорированный; длина 1200 мм; ширина 41 мм; высота 41 мм; материал: сталь; минимальная толщина металла: 2,5 мм; горячее цинкование по ГОСТ 9.307-2021, УХЛ1 (толщина цинкового покрытия 85 мкм)	2	шт/psc	для КМ211-31
7	EPROU00009	Профиль U-образный перфорированный; ширина 50 мм; высота 29 мм; длина 800 мм; материал: сталь; мин. толщина металла: 2,5 мм; горячее цинкование по ГОСТ 9.307-2021; толщина цинкового покрытия 85 мкм; УХЛ1	4	шт/psc	для КМ112-22
8	FSPFF00004	Опора для крепления к полу; перфорированного швеллера; габариты профиля / швеллера: ширина 80 мм; высота 40 мм; длина 1800 мм; материал: сталь; мин. толщина металла опоры: 6 мм; горячее цинкование по ГОСТ 9.307-2021; толщина цинкового покрытия 85 мкм; УХЛ1	4	шт/psc	
9	ETRAY00028	Лоток прямой; тип листовой неперфорированный; длина 3000 мм; ширина 100 мм; высота 100 мм; сталь; мин. толщина металла 1,5 мм; безопасная рабочая нагрузка ≥0,9 кН/м; при шаге крепления 1,5 м; горячее цинкование по ГОСТ 9.307-2021; толщина цинкового покрытия 85 мкм; УХЛ1; в комплекте: плоская крышка в комплекте с держателями; соединительные элементы лотков между собой (электропроводность обеспечивается без применения дополнительных проводников); метизы (термодиффузионное цинкование 40-50 мкм по ГОСТ Р 9.316-2006 или аналог)	34	компл.	
10	EPLGA00001	Полоса оцинкованная; ширина 50 мм; минимальная толщина металла 5 мм; горячее цинкование по ГОСТ 9.307-2021 (толщина цинкового покрытия 85 мкм); климатическое исполнение и категория размещения У1 по ГОСТ 15150-69, температура эксплуатации от минус 43,2 до плюс 34,7 °С	0,5	м/m	
11	ECBRT00030	Ответвление Т-образное горизонтальное; тип: листовой неперфорированный; ширина 100 мм; высота 100 мм; радиус поворота 150 мм; мин. толщина металла 1,5 мм; безопасная рабочая нагрузка ≥0,9 кН/м; горячее цинкование по ГОСТ 9.307-2021; толщина цинкового покрытия 85 мкм; УХЛ1; в комплекте: плоская крышка в комплекте с держателями; соединительные элементы лотков между собой (электропроводность обеспечивается без применения дополнительных проводников); метизы (термодиффузионное цинкование 40-50 мкм по ГОСТ Р 9.316-2006 или аналог)	2	компл.	
12	EANVE00158	Угол вертикальный внешний 90 гр.; тип: листовой неперфорированный; ширина 100 мм; высота 100 мм; радиус поворота 150 мм; сталь; мин. толщина металла 1,5 мм; безопасная рабочая нагрузка ≥0,9 кН/м; горячее цинкование по ГОСТ 9.307-2021; толщина цинкового покрытия 85 мкм; УХЛ1; в комплекте: плоская крышка в комплекте с держателями; соединительные элементы лотков между собой (электропроводность обеспечивается без применения дополнительных проводников); метизы (термодиффузионное цинкование 40-50 мкм по ГОСТ Р 9.316-2006 или аналог)	12	компл.	
13	EANVE00398	Угол вертикальный; внутренний; угол 90 гр; тип листовой неперфорированный; ширина 100 мм; высота 100 мм; радиус поворота 150 мм; сталь; минимальная толщина металла 1,5 мм; безопасная рабочая нагрузка ≥0,9 кН/м; горячее цинкование по ГОСТ 9.307-2021; толщина цинкового покрытия 85 мкм; -; УХЛ1; в комплекте: плоская крышка в комплекте с держателями; соединительные элементы лотков между собой (электропроводность обеспечивается без применения дополнительных проводников); метизы (термодиффузионное цинкование 40-50 мкм по ГОСТ Р 9.316-2006 или аналог); -	8	компл.	
14	EANHO00033	Угол горизонтальный 90 гр.; тип: листовой неперфорированный; ширина 100 мм; высота 100 мм; радиус поворота 150 мм; сталь; мин. толщина металла 1,5 мм; безопасная рабочая нагрузка ≥0,9 кН/м; горячее цинкование по ГОСТ 9.307-2021; толщина цинкового покрытия 85 мкм; УХЛ1; в комплекте: плоская крышка в комплекте с держателями; соединительные элементы лотков между собой (электропроводность обеспечивается без применения дополнительных проводников); метизы (термодиффузионное цинкование 40-50 мкм по ГОСТ Р 9.316-2006 или аналог)	11	компл.	
15	ETRAY00036	Лоток прямой; тип листовой неперфорированный; длина 3000 мм; ширина 300 мм; высота 100 мм; сталь; мин. толщина металла 1,5 мм; безопасная рабочая нагрузка ≥1,25 кН/м; при шаге крепления 1,5 м; горячее цинкование по ГОСТ 9.307-2021; толщина цинкового покрытия 85 мкм; УХЛ1; в комплекте: плоская крышка в комплекте с держателями; соединительные элементы лотков между собой (электропроводность обеспечивается без применения дополнительных проводников); метизы (термодиффузионное цинкование 40-50 мкм по ГОСТ Р 9.316-2006 или аналог)	4	компл.	
16	ETRDW00013	Переход лотка по ширине; левосторонний; тип: листовой неперфорированный; ширина перехода с 300 мм на 100 мм; высота 100 мм; сталь; мин. толщина металла 1,5 мм; безопасная рабочая нагрузка ≥1,25 кН/м; горячее цинкование по ГОСТ 9.307-2021; толщина цинкового покрытия 85 мкм; УХЛ1; в комплекте: плоская крышка в комплекте с держателями; соединительные элементы лотков между собой (электропроводность обеспечивается без применения дополнительных проводников); метизы (термодиффузионное цинкование 40-50 мкм по ГОСТ Р 9.316-2006 или аналог)	1	компл.	
17	ECBRT00037	Ответвление Т-образное горизонтальное; тип: листовой неперфорированный; ширина 300 мм; высота 100 мм; радиус поворота 150 мм; мин. толщина металла 1,5 мм; безопасная рабочая нагрузка ≥1,25 кН/м; горячее цинкование по ГОСТ 9.307-2021; толщина цинкового покрытия 85 мкм; УХЛ1; в комплекте: плоская крышка в комплекте с держателями; соединительные элементы лотков между собой (электропроводность обеспечивается без применения дополнительных проводников); метизы (термодиффузионное цинкование 40-50 мкм по ГОСТ Р 9.316-2006 или аналог)	1	компл.	
18	EANVE00284	Угол вертикальный внутренний 45 гр.; тип: листовой неперфорированный; ширина 300 мм; высота 100 мм; радиус поворота: 150 мм; сталь; мин. толщина металла 1,5 мм; безопасная рабочая нагрузка ≥1,25 кН/м; горячее цинкование по ГОСТ 9.307-2021; толщина цинкового покрытия 85 мкм; УХЛ1; в комплекте: плоская крышка в комплекте с держателями; соединительные элементы лотков между собой (электропроводность обеспечивается без применения дополнительных проводников); метизы (термодиффузионное цинкование 40-50 мкм по ГОСТ Р 9.316-2006 или аналог)	1	компл.	
19	EANVE00044	Угол вертикальный внешний 45 гр.; тип: листовой неперфорированный; ширина 300 мм; высота 100 мм; радиус поворота 150 мм; сталь; мин. толщина металла 1,5 мм; безопасная рабочая нагрузка ≥1,25 кН/м; горячее цинкование по ГОСТ 9.307-2021; толщина цинкового покрытия 85 мкм; УХЛ1; в комплекте: плоская крышка в комплекте с держателями; соединительные элементы лотков между собой (электропроводность обеспечивается без применения дополнительных проводников); метизы (термодиффузионное цинкование 40-50 мкм по ГОСТ Р 9.316-2006 или аналог)	1	компл.	
20	EWELF00009	Крепление приварное; для С-образного перфорированного профиля 41х41 мм (ШхВ); материал: сталь; толщина металла: 6 мм; горячее цинкование по ГОСТ 9.307-2021; толщина цинкового покрытия 85 мкм; УХЛ1; в комплекте: метизы для крепления профиля (термодиффузионное цинкование 40-50 мкм по ГОСТ Р 9.316-2006 или аналог)	8	компл.	
21	EPR2C00009	Профиль С-образный двойной; перфорированный; длина 3000 мм; ширина 41 мм; высота 82 мм; материал: сталь; мин. толщина металла: 2,5 мм; горячее цинкование по ГОСТ 9.307-2021; толщина цинкового покрытия 85 мкм; УХЛ1	2	шт.	
22	ECONH00005	Консоль с основанием; рабочая длина консоли 200 мм; высота полки не более 180 мм; материал: сталь; мин. толщина металла 2,5 мм; безопасная рабочая нагрузка ≥ 370 кг; горячее цинкование по ГОСТ 9.307-2021; толщина цинкового покрытия 85 мкм; климатическое исполнение и категория размещения У1 по ГОСТ 15150-69; в комплекте с креплением к С-образному профилю 41х41 (ШхВ) на горизонтальном участке (для метизов - термодиффузионное цинкование 40-50 мкм по ГОСТ Р 9.316-2006 или аналог)	20	компл.	
23	ECSTP00005	Скоба металлическая; двухлапковая (2-сторонняя); для крепления труб; DN25...26 мм; с отверстием под винт/шуруп; сталь оцинкованная; 1,5 мм; УХЛ1; -50...+80°С; 15 мин; ГОСТ Р 53316-2021 (в составе электропроводки согласно п. 6.5 СП 6.13130.2021)	20	шт/psc	
24	EPROZ00005	Профиль Z-образный; перфорированный; длина 3000 мм; ширина 50 мм; высота 50 мм; ширина отверстий -; материал: сталь; мин. толщина металла: 2,5 мм; горячее цинкование по ГОСТ 9.307-2021; толщина цинкового покрытия 85 мкм; УХЛ1	2	шт/psc	
-		Проходки / МСТ	1	компл.	
25	EFRMR00124	Рама прямоугольная металлическая для размещения уплотнительных модулей; из горячеоцинкованной стали по ГОСТ 9.307-2021 (толщина цинкового покрытия не менее 85 мкм); зона уплотнительной секции 60х60х60 мм (ШхВхГ); общее количество уплотнительных секций - 1; количество рядов уплотнительных секций - 1; в комплекте с фланцем; крепление - при помощи болтов; предел огнестойкости кабельной проходки в сборе не менее 120 EIT; климатическое исполнение и категория размещения У1 по ГОСТ 15150-69; стойкий к воздействию ультрафиолетового излучения; Степень защиты по ГОСТ 14254-2015 для кабельной проходки в сборе - не менее IP66; -; Срок службы не менее 25 лет.	1	шт/psc	
26	EFRRR00001	Рама прямоугольная металлическая ответная; из горячеоцинкованной стали по ГОСТ 9.307-2021 (толщина цинкового покрытия не менее 85 мкм); для рамы с зоной уплотнительной секции 60х60х60 мм (ШхВхГ); общее количество уплотнительных секций - 1; количество рядов уплотнительных секций - 1; в комплекте с фланцем; крепление - при помощи болтов; ; климатическое исполнение и категория размещения У1 по ГОСТ15150-69; стойкий к воздействию ультрафиолетового излучения; ; -; Срок службы не менее 25 лет.	1	шт/psc	
27	EUNCM00004	Компрессионный блок для прямоугольных секций рам; материал составных частей - нержавеющая сталь; Габаритные размеры: 60х60 мм (ШхГ); предел огнестойкости кабельной проходки в сборе не менее 120 EIT; климатическое исполнение и категория размещения У1 по ГОСТ 15150-69; стойкий к воздействию ультрафиолетового излучения; -; Степень защиты по ГОСТ 14254-2015 для кабельной проходки в сборе - не менее IP66; Срок службы не менее 25 лет.	1	шт/psc	
28	EMDLS00055	Модуль уплотнительный с сердечником; габаритные размеры 20х20х60 мм (ШхВхГ); диаметр вводимого кабеля - 5-13 мм; предел огнестойкости кабельной проходки в сборе не менее 120 EIT; климатическое исполнение и категория размещения У1 по ГОСТ 15150-69; стойкий к воздействию ультрафиолетового излучения; Степень защиты по ГОСТ 14254-2015 для кабельной проходки в сборе - не менее IP66; -; Срок службы не менее 25 лет.	3	шт/psc	
29	EMDLS00051	Модуль уплотнительный с сердечником; габаритные размеры 30х30х60 мм (ШхВхГ); диаметр вводимого кабеля - 13-23 мм; предел огнестойкости кабельной проходки в сборе не менее 120 EIT; климатическое исполнение и категория размещения У1 по ГОСТ 15150-69; стойкий к воздействию ультрафиолетового излучения; Степень защиты по ГОСТ 14254-2015 для кабельной проходки в сборе - не менее IP66; -; Срок службы не менее 25 лет.	2	шт/psc	
30	EMDLS00033	Модуль уплотнительный; компенсационный; габаритные размеры 60х10х60 мм (ШхВхГ); предел огнестойкости кабельной проходки в сборе не менее EIT 120; степень защиты по ГОСТ 14254-2015 для кабельной проходки в сборе - не менее IP 66; климатическое исполнение и категория размещения У1 по ГОСТ 15150-69; стойкий к воздействию ультрафиолетового излучения	1	шт/psc	
31	EPLSP00005	Разделительная пластина, для установки между рядами уплотнительных модулей; Материал - нержавеющая сталь; Габаритные размеры: ширина - 60 мм, глубина - под уплотнительные модули глубиной 60 мм; предел огнестойкости кабельной проходки в сборе не менее 120 EIT; климатическое исполнение и категория размещения У1 по ГОСТ 15150-69; стойкий к воздействию ультрафиолетового излучения; -; Степень защиты по ГОСТ 14254-2015 для кабельной проходки в сборе - не менее IP66; Срок службы не менее 25 лет.	2	шт/psc	
32	EPLSP00013	Разделительная пластина фиксирующая, для поддержания рядов модулей в предварительно сжатом состоянии; Материал - нержавеющая сталь; Габаритные размеры: ширина - 60 мм, глубина - под уплотнительные модули глубиной 60 мм; предел огнестойкости кабельной проходки в сборе не менее 120 EIT; климатическое исполнение и категория размещения У1 по ГОСТ 15150-69; стойкий к воздействию ультрафиолетового излучения; -; Степень защиты по ГОСТ 14254-2015 для кабельной проходки в сборе - не менее IP66; Срок службы не менее 25 лет.	1	шт/psc	
33	EGRSE00001	Смазка для монтажа уплотнительных модулей; объем 30 мл	1	шт/psc	
34	ETPHS00001	Лента высокой прочности; вспучивающаяся при воздействии высоких температур; для уплотнения стыка между фланцем рамы и стеной; длина рулона - 2 м	1	м/m	
35	QTCSM00001	Инструмент для прижима уплотнительных модулей; для секции 60 мм	1	шт/psc	

03

Согласовано

Взам. инв. №

Подп. и дата

Инв. № подл.

Статус Status	Рев. Rev.	Дата Date	Назначение выпуска / Reason for Issue	Разраб. Drawn	Провер. Checked	Утверд. Approved
IFC	03	04.12.25	Выпущено для строительства / Issued for Construction	Поминова	Тулба	Трофимов
IFC	02H	21.03.25	Выпущено для строительства / Issued for Construction	Шевцова	Охота	Подземельнов
IFR	01H	23.08.24	Выпущено для рассмотрения / Issued for Review	Гайсина	Гильманова	Трофимов

GAS PROCESSING COMPLEX WITHIN UST-LUGA ETHANE-RICH GAS PROCESSING CLUSTER. GAS PROCESSING PLANT AND UTILITIES, INFRASTRUCTURE AND OFFSITE PROCESS FACILITIES

GO-D8810BXO
Fire Water Pump Station

Stage	Sheet	Total Sheets
DDD	8	

List of Materials

РУСХИМАЛЬЯНС

Изм.	Кол.уч.	Лист	№док.	Подпись	Дата

Разраб.	Поминова		04.12.25
Проверил	Тулба		04.12.25
Нач. сект	Савчук		04.12.25
Н. контр.	Тулба		04.12.25
ГИП	Трофимов		04.12.25

GLE-(GO-D8810BXO)-IN-GDSS-001

ГАЗОПЕРЕРАБАТЫВАЮЩИЙ КОМПЛЕКС В СОСТАВЕ КОМПЛЕКСА ПЕРЕРАБОТКИ ЭТАНОСОДЕРЖАЩЕГО ГАЗА В РАЙОНЕ ПОСЕЛКА УСТЬ-ЛУГА. ГАЗОПЕРЕРАБАТЫВАЮЩИЙ ЗАВОД И ТЕХНОЛОГИЧЕСКИЕ ОБЪЕКТЫ ОБЩЕЗАВОДСКОГО ХОЗЯЙСТВА

GO-D8810BXO
Насосная станция противопожарного водоснабжения

Стадия	Лист	Листов
Р	8	

Перечень материалов

ГЛИнжиниринг
ПРОЕКТИРУЕМ БУДУЩЕЕ ОТРАСЛИ

GLE-(GO-D8810BXO)-IN-GDSS-001_03_AL.DWG

Формат А2х3

List of Materials

Item	Ident. no.	Description	Qty	Weight per item, kg	Note
1	EWIRE00055	Hook-up tinned copper core wire ПуГВнг (A)-LS 1x6, flexible, with PVC insulation, flame retardant if installed in bundles as per Category A, low smoke, UV resistant; ambient temperature: from −43.2 °C to +34.7° C during operation; minimum cable installation temperature without preheating: −15 °C; yellow-green; GOST 31947-2012; minimum service life: 25 years	110	m	
2	EWIRE00058	Hook-up tinned copper core wire ПуГВнг (A)-LS 1x25, flexible, with PVC insulation, flame retardant if installed in bundles as per Category A, low smoke, UV resistant; ambient temperature: from −43.2 °C to +34.7° C during operation; minimum cable installation temperature without preheating: −15 °C; yellow-green; GOST 31947-2012; minimum service life: 25 years	80	m	
3	ECHNN00078	Perforated channel; W=80mm; H=40mm; L=1800mm; steel; min. steel thickness: 4.5mm; hot dip galvanized acc. to GOST 9.307-2021; УХЛ 1 (zinc coating thickness: 85 µm)	4	pcs	for KM211-31
4	EEARL00001	Tinned copper earthing bar; for 3 connections (M6) for 6 mm2 wire; W=40mm; min. steel thickness: 4mm; climatic design and location category acc. to GOST 15150-69: У1, operating temperature: −43.2 °C to +34.7 °C; complete with metalware (thermal diffusion galvanizing 40-50 µm acc. to GOST R 9.316-2006 or equivalent): earthing bar fasteners (hexagon bolts M10x30, flat and spring washers M10, hexagon nuts M10), fasteners for connections (hexagon bolts M6x20, flat and spring washers M6, hexagon nuts M6)	2	pcs	
5	EPPRC00001	Stanchion DN50; L=1800mm; material: steel; min. steel thickness 3.5mm; hot dip galvanized acc. to GOST 9.307-2021; zinc coating thickness: 85 µm; У1; operating temperature: from −43.2 °C to +34.7 °C; complete with baseplate 210x210mm for floor mounting (4 holes Ø11mm), earthing plate (hole Ø11mm), protective cap	4	pcs	for KM112-22
6	EPROC00013	Perforated C-shape; L=1200mm; W=41mm; H=41mm, steel; min. steel thickness: 2.5mm; hot dip galvanized acc. to GOST 9.307-2021; УХЛ 1 (zinc coating thickness: 85 µm)	2	pcs	for KM211-31
7	EPROU00009	Perforated U-shape; W=50mm; H=29mm; L=800mm, steel; min. steel thickness: 2.5mm; hot dip galvanized acc. to GOST 9.307-2021; zinc coating thickness: 85 µm; УХЛ 1	4	pcs	for KM112-22
8	FSPFF00004	Support for floor mounting of perforated channel; shape/channel dimensions: W=80mm; H=40mm; L=1800mm; steel; min. steel thickness of support: 6mm; hot dip galvanized acc. to GOST 9.307-2021; zinc coating thickness: 85 µm; УХЛ 1	4	pcs	
9	ETRAY00028	Straight non-perforated cable tray; L=3000mm; W=100mm; H=100mm; steel; min. steel thickness: 1.5mm; SWL≥0.9 kN/m; support spacing: 1.5m; hot dip galvanized acc. to GOST 9.307-2021; zinc coating thickness: 85 µm; УХЛ 1; complete with flat cover with clamps; cable tray connectors (electrical conductivity is provided without additional conductors); metalware (thermal diffusion galvanizing 40-50 µm acc. to GOST R 9.316-2006 or equivalent)	34	set	
10	EPLGA00001	Galvanized flat bar W=50mm; min. steel thickness: 5mm; hot dip galvanized acc. to GOST 9.307-2021 (zinc coating thickness: 85 µm); climatic design and location category acc. to GOST 15150-69: У1, operating temperature: from −43.2 °C to +34.7 °C	0,5	m	
11	ECBRT00030	Horizontal non-perforated cable tray tee; W=100mm; H=100mm; bend radius: 150mm; min. steel thickness: 1.5mm; SWL≥0.9 kN/m; hot dip galvanized acc. to GOST 9.307-2021; zinc coating thickness: 85 µm; УХЛ 1; complete with flat cover with clamps; cable tray connectors (electrical conductivity is provided without additional conductors); metalware (thermal diffusion galvanizing 40-50 µm acc. to GOST R 9.316-2006 or equivalent)	2	set	
12	EANVE00158	Vertical outside non-perforated cable tray bend 90°; W=100mm; H=100mm; bend radius: 150mm; steel; min. steel thickness: 1.5mm; SWL≥0.9 kN/m; hot dip galvanized acc. to GOST 9.307-2021; zinc coating thickness: 85 µm; УХЛ 1; complete with flat cover with clamps; cable tray connectors (electrical conductivity is provided without additional conductors); metalware (thermal diffusion galvanizing 40-50 µm acc. to GOST R 9.316-2006 or equivalent)	12	set	
13	EANVE00398	Vertical inside non-perforated cable tray bend 90°; W=100mm; H=100mm; bend radius: 150mm; steel; min. steel thickness: 1.5mm; SWL≥0.9 kN/m; hot dip galvanized acc. to GOST 9.307-2021; zinc coating thickness: 85 µm; -; УХЛ 1; complete with flat cover with clamps; cable tray connectors (electrical conductivity is provided without additional conductors); metalware (thermal diffusion galvanizing 40-50 µm acc. to GOST R 9.316-2006 or equivalent); -	8	set	
14	EANHO00033	Horizontal non-perforated cable tray bend 90°; W=100mm; H=100mm; bend radius: 150mm; steel; min. steel thickness: 1.5mm; SWL≥0.9 kN/m; hot dip galvanized acc. to GOST 9.307-2021; zinc coating thickness: 85 µm; УХЛ 1; complete with flat cover with clamps; cable tray connectors (electrical conductivity is provided without additional conductors); metalware (thermal diffusion galvanizing 40-50 µm acc. to GOST R 9.316-2006 or equivalent)	11	set	
15	ETRAY00036	Straight non-perforated cable tray; L=3000mm; W=300mm; H=100mm; steel; min. steel thickness: 1.5mm; SWL≥1.25 kN/m; support spacing: 1.5m; hot dip galvanized acc. to GOST 9.307-2021; zinc coating thickness: 85 µm; УХЛ 1; complete with flat cover with clamps; cable tray connectors (electrical conductivity is provided without additional conductors); metalware (thermal diffusion galvanizing 40-50 µm acc. to GOST R 9.316-2006 or equivalent)	4	set	
16	ETRDW00013	Non-perforated cable tray reducer (left hand); W=300/100mm; H=100mm; steel; min. steel thickness: 1.5mm; SWL≥1.25 kN/m; hot dip galvanized acc. to GOST 9.307-2021; zinc coating thickness: 85 µm; УХЛ 1; complete with flat cover with clamps; cable tray connectors (electrical conductivity is provided without additional conductors); metalware (thermal diffusion galvanizing 40-50 µm acc. to GOST R 9.316-2006 or equivalent)	1	set	
17	ECBRT00037	Horizontal non-perforated cable tray tee; W=300mm; H=100mm; bend radius: 150mm; min. steel thickness: 1.5mm; SWL≥1.25 kN/m; hot dip galvanized acc. to GOST 9.307-2021; zinc coating thickness: 85 µm; УХЛ 1; complete with flat cover with clamps; cable tray connectors (electrical conductivity is provided without additional conductors); metalware (thermal diffusion galvanizing 40-50 µm acc. to GOST R 9.316-2006 or equivalent)	1	set	
18	EANVE00284	Vertical inside non-perforated cable tray bend 45°; W=300mm; H=100mm; bend radius: 150mm; steel; min. steel thickness: 1.5mm; SWL≥1.25 kN/m; hot dip galvanized acc. to GOST 9.307-2021; zinc coating thickness: 85 µm; УХЛ 1; complete with flat cover with clamps; cable tray connectors (electrical conductivity is provided without additional conductors); metalware (thermal diffusion galvanizing 40-50 µm acc. to GOST R 9.316-2006 or equivalent)	1	set	
19	EANVE00044	Vertical outside non-perforated cable tray bend 45°; W=300mm; H=100mm; bend radius: 150mm; steel; min. steel thickness: 1.5mm; SWL≥1.25 kN/m; hot dip galvanized acc. to GOST 9.307-2021; zinc coating thickness: 85 µm; УХЛ 1; complete with flat cover with clamps; cable tray connectors (electrical conductivity is provided without additional conductors); metalware (thermal diffusion galvanizing 40-50 µm acc. to GOST R 9.316-2006 or equivalent)	1	set	
20	EWELF00009	Welded fastener for perforated C-shape W=41mm, H=41mm; material: steel; steel thickness: 6mm, hot-dip galvanized acc. to GOST 9.307-2021; zinc coating thickness: 85 µm; УХЛ 1; complete with metalware for shape attachment (thermal diffusion galvanizing 40-50 µm acc. to GOST R 9.316-2006 or equivalent)	8	set	
21	EPR2C00009	Perforated double C-shape; L=3000mm; W=41mm; H=82mm, steel; min. steel thickness: 2.5mm; hot dip galvanized acc. to GOST 9.307-2021; zinc coating thickness: 85 µm; УХЛ 1	2	pcs	
22	ECONH00005	Cantilever bracket with baseplate; cantilever bracket effective length: 200mm; max. height: 180mm; material: steel; min. steel thickness: 2.5mm; SWL≥370kg; hot dip galvanized acc. to GOST 9.307-2021; zinc coating thickness: 85 µm; climatic design and location category acc. to GOST 15150-69: У1; complete with fasteners for attachment to C-shape W=41, H=41 on a horizontal section (for metalware: thermal diffusion galvanizing 40-50 µm acc. to GOST R 9.316-2006 or equivalent)	20	set	
23	ECSTP00005	Steel clamp; two-hole (2 sides); for attachment of conduits; DN25...26mm; screw hole; galvanized steel; 1.5mm; УХЛ 1; −50... +80 °C; 15 min; GOST R 53316-2021 (as part of wiring acc. to para. 6.5 of SP 6.13130.2021)	20	pcs	
24	EPROZ00005	Perforated Z-shape; L=3000mm; W=50mm; H=50mm; perforation width -; steel; min. steel thickness: 2.5mm; hot dip galvanized acc. to GOST 9.307-2021; zinc coating thickness: 85 µm; УХЛ 1	2	pcs	
-		Multi-cable transits (MCT)	1	set	
25	EFRMR00124	Steel rectangular frame for sealing module installation; hot-dip galvanized acc. to GOST 9.307.2021 (min. zinc coating thickness: 85 µm); packing section: 60x60x60mm (WxHxD); number of sections: 1; number of rows: 1; complete with flange; bolted connection; min. fire rating of assembled multi-cable transit: 120 EIT; climatic design and location category acc. to GOST 15150-69: У1; UV-resistant; IP rating of assembled multi-cable transit acc. to GOST 14254-2015: min. IP 66; -; minimum service life: 25 years.	1	pcs	
26	EFRRR00001	Steel rectangular mating frame; hot dip galvanized as per GOST 9.307-2021 (min. zinc coating thickness: 85 µm) for frame with packing section 60x60x60mm (WxHxD); number of sections: 1; number of rows: 1; complete with flange; bolted connection; ; climatic design and location category acc. to GOST 15150-69: У1; UV-resistant; ; -; minimum service life: 25 years.	1	pcs	
27	EUNCM00004	Compression unit for rectangular frame sections; material of components: stainless steel; overall dimensions: 60x60mm (WxD); min. fire rating of assembled multi-cable transit: 120 EIT; climatic design and location category acc. to GOST 15150-69: У1; UV-resistant; -; IP rating of assembled multi-cable transit acc. to GOST 14254-2015: min. IP66; minimum service life: 25 years.	1	pcs	
28	EMDLS00055	Sealing module with core; overall dimensions 20x20x60mm (WxHxD); input cable diameter: 5-13 mm; min. fire rating of assembled multi-cable transit: 120 EIT; climatic design and location category acc. to GOST 15150-69: У1; UV-resistant; IP rating of assembled multi-cable acc. to GOST 14254-2015: min. IP66; -; minimum service life: 25 years.	3	pcs	
29	EMDLS00051	Sealing module with core; overall dimensions 30x30x60mm (WxHxD); input cable diameter: 13-23 mm; min. fire rating of assembled multi-cable transit: 120 EIT; climatic design and location category acc. to GOST 15150-69: У1; UV-resistant; IP rating of assembled multi-cable acc. to GOST 14254-2015: min. IP66; -; minimum service life: 25 years.	2	pcs	
30	EMDLS00033	Expansion sealing module; overall dimensions: 60x10x60mm (WxHxD); min. fire rating of assembled multi-cable transit: EIT 120; IP rating of assembled multi-cable transit acc. to GOST 14254-2015: min. IP 66; climatic design and location category acc. to GOST 15150-69: У1; UV-resistant	1	pcs	
31	EPLSP00005	Separation plate for installation between the sealing module rows; material: stainless steel; overall dimensions: W=60 mm, depth: suitable for 60mm deep sealing modules; min. fire rating of assembled multi-cable transit: 120 EIT; climatic design and location category acc. to GOST 15150-69: У1; UV-resistant; -; IP rating of assembled multi-cable transit acc. to GOST 14254-2015: min. IP66; minimum service life: 25 years	2	pcs	
32	EPLSP00013	Fixing separation plate for maintaining the module rows in a pre-compressed state; material: stainless steel; overall dimensions: W=60mm, depth: suitable for 60mm deep sealing modules; min. fire rating of assembled multi-cable transit: 120 EIT; climatic design and location category acc. to GOST 15150-69: У1; UV-resistant; -; IP rating of assembled multi-cable transit acc. to GOST 14254-2015: min. IP66; minimum service life: 25 years	1	pcs	
33	EGRSE00001	Lubricant for installation of sealing modules; 30 mL	1	pcs	
34	ETPHS00001	High strength intumescent tape to seal the joint between the frame flange and the wall; roll length: 2 m	1	m	
35	QTCSM00001	Tools for holding down sealing modules; for 60mm section	1	pcs	

03

Согласовано

Взам. инв. №

Подп. и дата

Инв. № подл.

IFC	03	04.12.25	Выпущено для строительства / Issued for Construction	Поминова	Тулба	Трофимов
IFC	02H	21.03.25	Выпущено для строительства / Issued for Construction	Шевцова	Охота	Подземельнов
IFR	01H	23.08.24	Выпущено для рассмотрения / Issued for Review	Гайсина	Гильманова	Трофимов
Статус Status	Рев. Rev.	Дата Date	Назначение выпуска / Reason for Issue	Разраб. Drawn	Провер. Checked	Утверд. Approved

GAS PROCESSING COMPLEX WITHIN UST-LUGA ETHANE-RICH GAS PROCESSING CLUSTER. GAS PROCESSING PLANT AND UTILITIES, INFRASTRUCTURE AND OFFSITE PROCESS FACILITIES

GO-D8810BX0
Fire Water Pump Station

Stage	Sheet	Total Sheets
DDD	9	

List of Materials

РУСХИМАЛЬЯНС

GLE-(GO-D8810BX0)-IN-GDSS-001

ГАЗОПЕРЕРАБАТЫВАЮЩИЙ КОМПЛЕКС В СОСТАВЕ КОМПЛЕКСА ПЕРЕРАБОТКИ ЭТАНОСОДЕРЖАЩЕГО ГАЗА В РАЙОНЕ ПОСЕЛКА УСТЬ-ЛУГА. ГАЗОПЕРЕРАБАТЫВАЮЩИЙ ЗАВОД И ТЕХНОЛОГИЧЕСКИЕ ОБЪЕКТЫ ОБЩЕЗАВОДСКОГО ХОЗЯЙСТВА

Изм.	Кол.уч.	Лист	№док.	Подпись	Дата

Разраб.	Поминова		04.12.25
Проверил	Тулба		04.12.25
Нач. сект	Савчук		04.12.25
Н. контр.	Тулба		04.12.25
ГИП	Трофимов		04.12.25

GO-D8810BX0
Насосная станция противопожарного водоснабжения

Стадия	Лист	Листов
Р	9	

Перечень материалов

ГЛИнжиниринг
ПРОЕКТИРУЕМ БУДУЩЕЕ ОТРАСЛИ

GLE-(GO-D8810BX0)-IN-GDSS-001_03_AL.DWG

Формат А2х3

План расположения КИПиА и кабельных трасс на отм. 0,000; -3,000 (1:100)

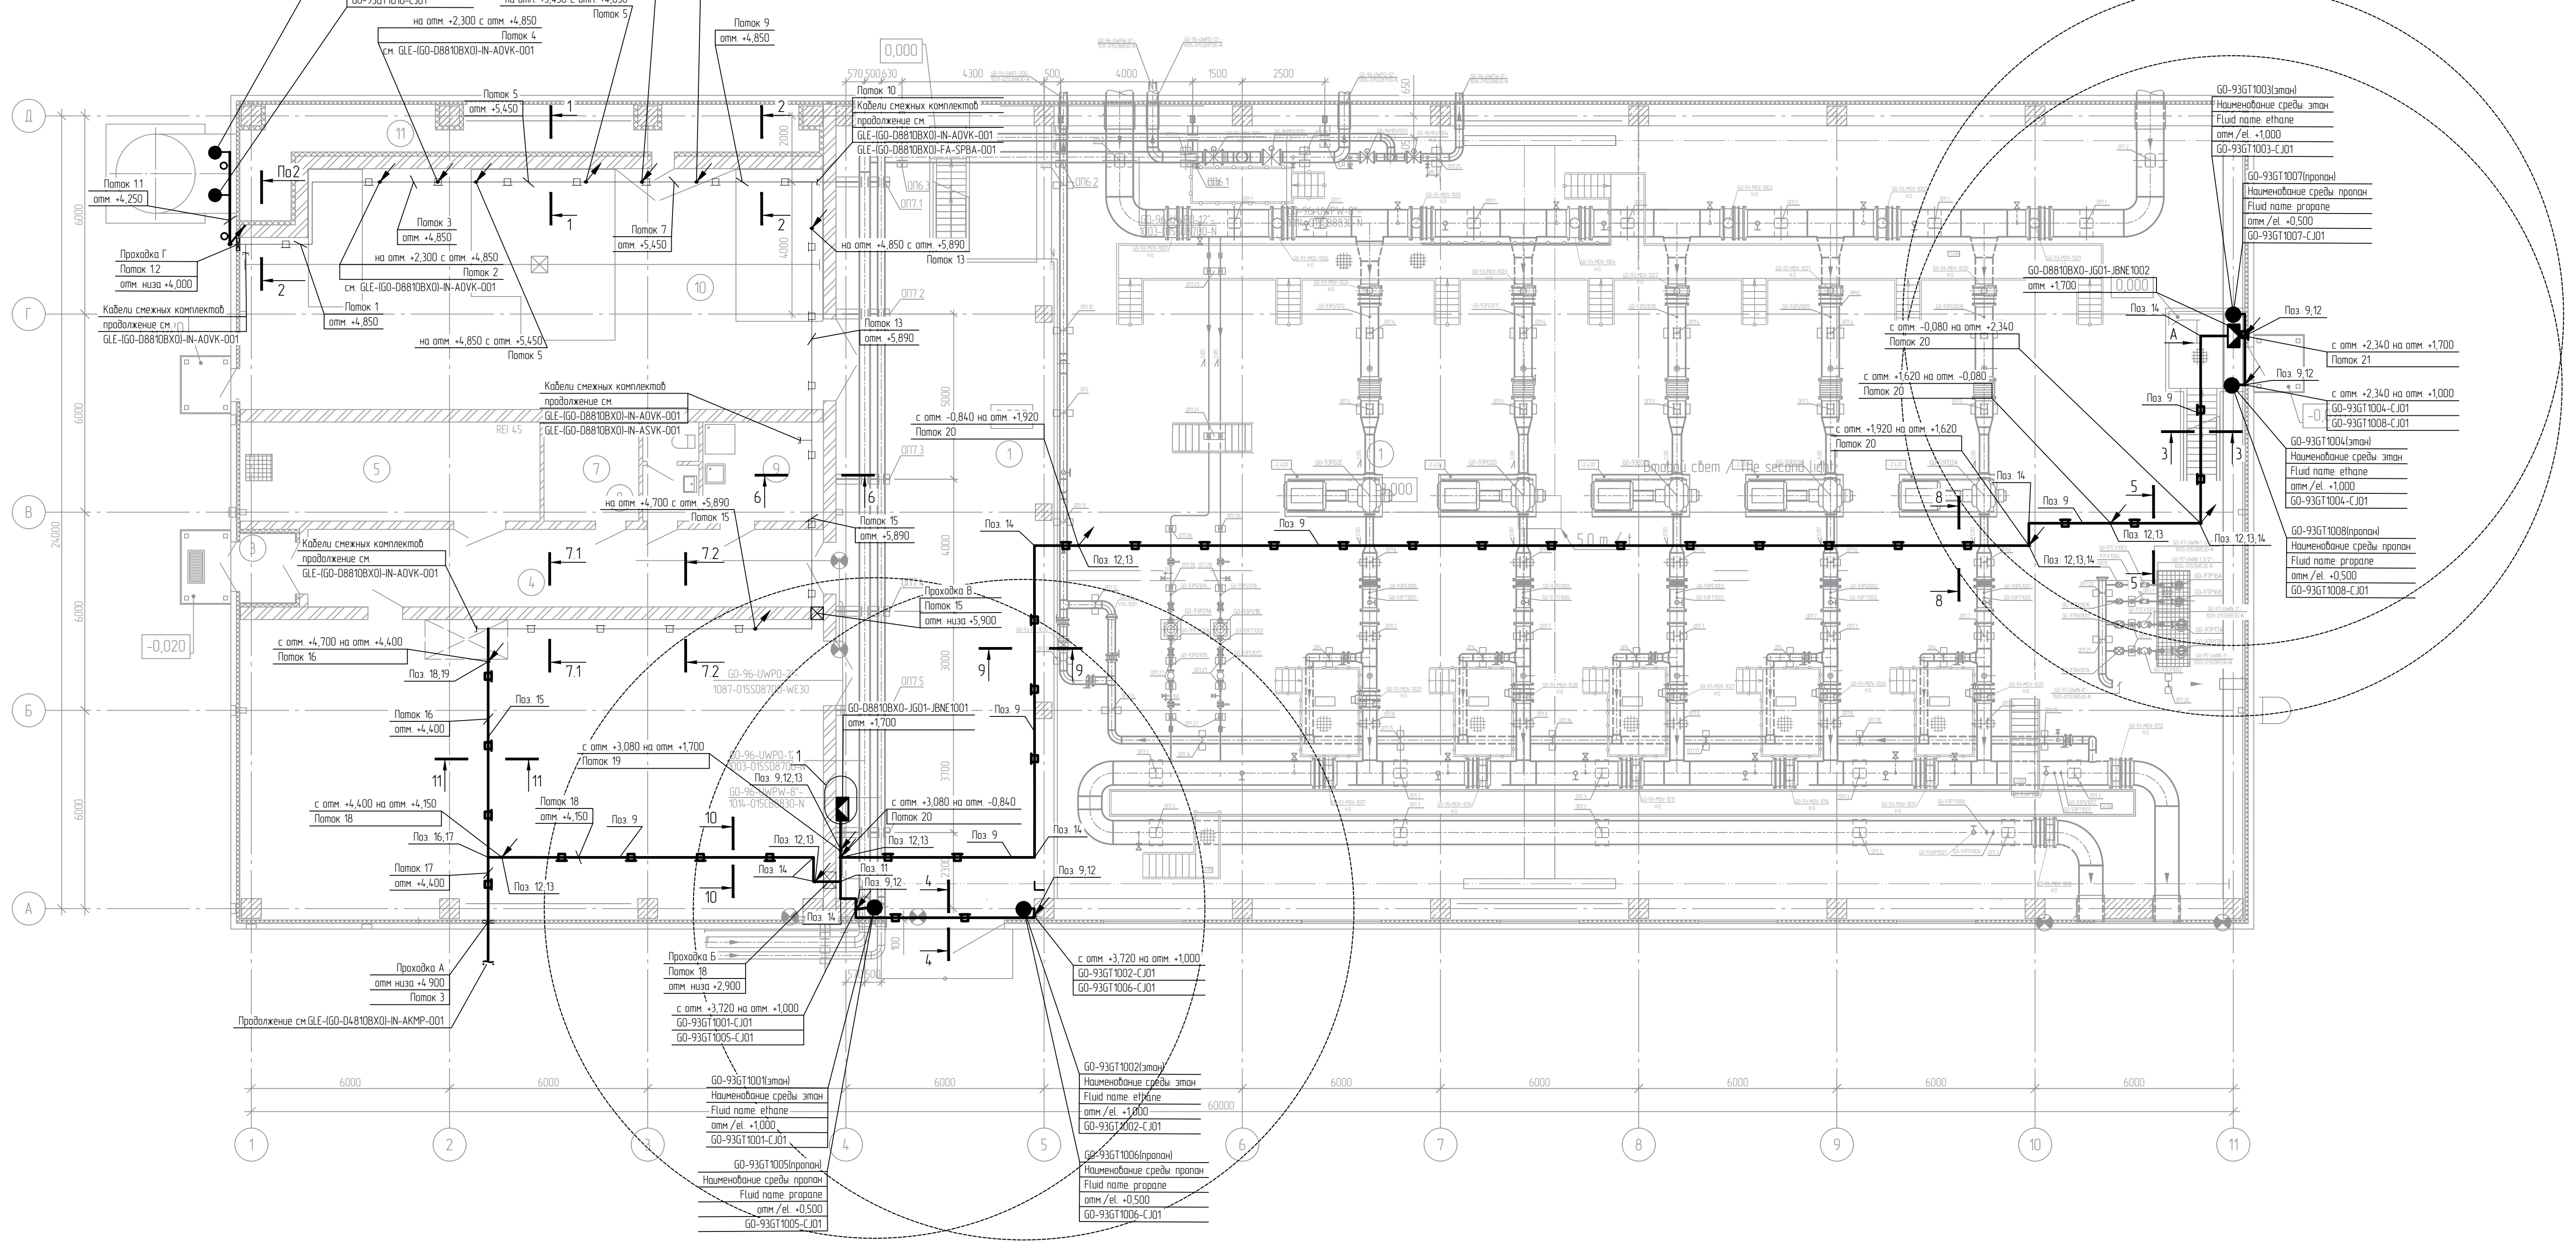

Поток 1.1

Металлорукав DN25
GO-93GT1009-CJ01
Металлорукав DN25
GO-93GT1010-CJ01

Поток 1.2

Проходка Г
GO-93GT1009-CJ01
GO-93GT1010-CJ01
GO-D88LS1001-CJ01
GO-D88LS1001-CJ02

Кабели учтены в комплекте GLE-(GO-D8810BX0)-IN-ASVK-001

Поток 1

Лоток 300 x 100 JN
GO-D88TE1021A-CJ01
GO-D88TE1021B-CJ01
GO-D88TV1216A-CJ01
GO-D88PS1217A-CJ01
GO-D88TV1216B-CJ01
GO-D88PS1217B-CJ01
GO-D88TE1206A-CJ01
GO-D88TE1206B-CJ01
GO-D88LS1001-CJ01
GO-D88LS1001-CJ02
GO-93GT1009-CJ01
GO-93GT1010-CJ01

Кабели учтены в комплекте GLE-(GO-D8810BX0)-IN-ASVK-001

Кабели учтены в комплекте GLE-(GO-D8810BX0)-IN-AOVK-001

Поток 2

не используется

Поток 3

Лоток 300 x 100 JN
GO-D88TE1220A-CJ01
GO-D88TE1220B-CJ01
GO-D88TE1230A-CJ01
GO-D88TE1230B-CJ01
GO-D88TE1021A-CJ01
GO-D88TE1021B-CJ01
GO-D88LS1001-CJ01
GO-D88LS1001-CJ02
GO-93GT1009-CJ01
GO-93GT1010-CJ01

Кабели учтены в комплекте GLE-(GO-D8810BX0)-IN-ASVK-001

Кабели учтены в комплекте GLE-(GO-D8810BX0)-IN-AOVK-001

Поток 4

не используется

Поток 5

Лоток 300 x 100 JN
GO-D88TE1220A-CJ01
GO-D88TE1220B-CJ01
GO-D88TE1230A-CJ01
GO-D88TE1230B-CJ01
GO-D88TE1430-CJ01
GO-D88TE1021A-CJ01
GO-D88TE1021B-CJ01
GO-D88LS1001-CJ01
GO-D88LS1001-CJ02
GO-93GT1009-CJ01
GO-93GT1010-CJ01

Кабели учтены в комплекте GLE-(GO-D8810BX0)-IN-ASVK-001

Кабели учтены в комплекте GLE-(GO-D8810BX0)-IN-AOVK-001

Поток 6

не используется

Поток 7

Лоток 300 x 100 JN
GO-D88TE1220A-CJ01
GO-D88TE1220B-CJ01
GO-D88TE1230A-CJ01
GO-D88TE1230B-CJ01
GO-D88TE1430-CJ01
GO-D88TE1021B-CJ01
GO-D88TE1030A-CJ01
GO-D88TV1116A-CJ01
GO-D88PS1117A-CJ01
GO-D88TE1106A-CJ01
GO-D88TE1221A-CJ01
GO-D8810BX0-JP01-JBNE1003A-CJ01
GO-D88LS1001-CJ01
GO-D88LS1001-CJ02
GO-93GT1009-CJ01
GO-93GT1010-CJ01

Кабели учтены в комплекте GLE-(GO-D8810BX0)-IN-ASVK-001

Кабели учтены в комплекте GLE-(GO-D8810BX0)-IN-AOVK-001

Поток 8

не используется

Поток 9

Лоток 300 x 100 JN
GO-D88TE1220A-CJ01
GO-D88TE1220B-CJ01
GO-D88TE1230A-CJ01
GO-D88TE1230B-CJ01
GO-D88TE1430-CJ01
GO-D88TE1030A-CJ01
GO-D88TE1022A-CJ01
GO-D88TV1116A-CJ01
GO-D88PS1117A-CJ01
GO-D88TE1106A-CJ01
GO-D88TE1030B-CJ01
GO-D88TE1022B-CJ01
GO-D88TV1116B-CJ01
GO-D88PS1117B-CJ01
GO-D88TE1106B-CJ01
GO-D88TE1221A-CJ01
GO-D88TE1221B-CJ01
GO-D8810BX0-JP01-JBNE1003A-CJ01
GO-D8810BX0-JP01-JBNE1003B-CJ01
GO-D88LS1001-CJ01
GO-D88LS1001-CJ02
GO-93GT1009-CJ01
GO-93GT1010-CJ01

Кабели учтены в комплекте GLE-(GO-D8810BX0)-IN-AOVK-001

Кабели учтены в комплекте GLE-(GO-D8810BX0)-IN-ASVK-001

Поток 10

не используется

Поток 11

не используется

Поток 12

не используется

Поток 13

Лоток 300 x 100 JN
GO-D88TE1220A-CJ01
GO-D88TE1220B-CJ01
GO-D88TV1116A-CJ01
GO-D88PS1117A-CJ01
GO-D88TE1106A-CJ01
GO-D88TV1116B-CJ01
GO-D88PS1117B-CJ01
GO-D88TE1106B-CJ01
GO-D8810BX0-JP01-JBNE1003A-CJ01
GO-D8810BX0-JP01-JBNE1003B-CJ01
GO-D88LS1001-CJ01
GO-D88LS1001-CJ02
GO-D8801FX0-JU01-JBNE1002-CJ01
GO-D8801FX0-JU01-JBNE1003-CJ01
GO-93GT1009-CJ01
GO-93GT1010-CJ01

Кабели учтены в комплекте GLE-(GO-D8810BX0)-IN-AOVK-001

Кабели учтены в комплекте GLE-(GO-D8810BX0)-IN-ASVK-001

Кабели учтены в комплекте GLE-(GO-D8810BX0)-FA-SPBA-001

Поток 14

не используется

Поток 15

Лоток 300 x 100 JN
GO-D88TE1220A-CJ01
GO-D88TE1220B-CJ01
GO-D8801FX0-JU01-JBNE1002-CJ01
GO-D8801FX0-JU01-JBNE1003-CJ01
GO-93GT1009-CJ01
GO-93GT1010-CJ01

Кабели учтены в комплекте GLE-(GO-D8810BX0)-IN-AOVK-001

Кабели учтены в комплекте GLE-(GO-D8810BX0)-FA-SPBA-001

Поток 16

Лоток 300 x 100 JN
GO-D8801FX0-JU01-JBNE1002-CJ01
GO-D8801FX0-JU01-JBNE1003-CJ01
GO-93GT1009-CJ01
GO-93GT1010-CJ01

Кабели учтены в комплекте GLE-(GO-D8810BX0)-FA-SPBA-001

Поток 17

Лоток 300 x 100 JN
GO-D8801FX0-JU01-JBNE1002-CJ01
GO-D8801FX0-JU01-JBNE1003-CJ01
GO-D8810BX0-JG01-JBNE1001-CJ01
GO-D8810BX0-JG01-JBNE1002-CJ01

Кабели учтены в комплекте GLE-(GO-D8810BX0)-FA-SPBA-001

Stream 18

Лоток 100 x 100 JN
GO-D8810BX0-JG01-JBNE1001-CJ01
GO-D8810BX0-JG01-JBNE1002-CJ01
GO-93GT1009-CJ01
GO-93GT1010-CJ01

Поток 19

Лоток 100 x 100 JN
GO-D8810BX0-JG01-JBNE1001-CJ01
GO-93GT1009-CJ01
GO-93GT1010-CJ01
GO-93GT1001-CJ01
GO-93GT1002-CJ01
GO-93GT1005-CJ01
GO-93GT1006-CJ01

Поток 20

Лоток 100 x 100 JN
GO-D8810BX0-JG01-JBNE1002-CJ01

Поток 21

Лоток 100 x 100 JN
GO-D8810BX0-JG01-JBNE1002-CJ01
GO-93GT1004-CJ01
GO-93GT1008-CJ01

Условные графические изображения / Graphic symbols

Обозначение Symbol	Наименование Description
—□——□—	Кабельная трасса, прокладываемая в лотке либо/коробе в комплекте GLE-(GO-D8810BX0)-IN-AOVK-001\ Cable route laid in a tray or box in another set GLE-(GO-D8810BX0)-IN-AOVK-001
━■━━■━	Кабельная трасса, прокладываемая в лотке либо/коробе в комплекте GLE-(GO-D8810BX0)-IN-GDSS-001\ Cable route laid in a tray or box in another set GLE-(GO-D8810BX0)-IN-GDSS-001
—o——o—	Кабельная трасса, прокладываемая в трубе
■	Клеммная коробка/Junction box
↗ ↙	Трасса уходит на (приходит с) более высокую отметку/The route goes to (comes from) a higher elevation
↙ ↗	Трасса уходит на (приходит с) более низкую отметку/The route goes to (comes from) a lower elevation
⊙	Датчик загазованности, радиус действия 10 м/The route goes to (comes from) a lower elevation
GO-93GT1001-CJ01	Обозначение кабеля / Cable designation
Лоток 100 x 100 JN	Кабельный лоток 100х100 для КИПиА /Cableway 100x100 for instrumentation

Принятые сокращения/Accepted abbreviations

СС – кабели сетей связи (в данном документе не рассматривается)
ЭС – кабели электроснабжения (в данном документе не рассматривается)
АСПСиПТ – кабели пожарной сигнализации (в данном документе не рассматривается)
КИП – кабели контрольно-измерительных приборов (в данном документе не рассматривается)
JS – кабели контрольно-измерительных приборов (искробезопасные, в данном документе не рассматривается)
JN – кабели контрольно-измерительных приборов (неискробезопасные)

1. За относительную отметку –3,000 помещения машзала принята верхняя точка бетонного покрытия. За относительную отметку 0.000 принята абсолютная отметка + 27,000 м в единицах Балтийской системы высот.
2. Чертеж выполнен в масштабе 1:100.
3. Подключение кабелей к КИП и клеммным коробкам, защиту кабелей металлорукавом, монтаж кабельных вводов и заземление вышеуказанного оборудования и материалов выполнить с соответствии с электромонтажными схемами КИПиА GLE-(GO-Z00000X0)-IN-ZX-001.
4. Монтаж КИП, соединительных коробок выполнить в соответствии с механическими схемами монтажа КИПиА GLE-(GO-Z00000X0)-IN-ZX-002. Монтаж GO-D8810BX0-JG01-JBNE1001, GO-D8810BX0-JG01-JBNE1002 выполнить по схеме КМ211-31 "Клеммная коробка на стойке с установкой на бетонном полу". Монтаж датчиков загазованности на отм. –3,000 выполнить по схеме КМ112-22.
5. Для защиты персонала от поражения электрическим током, уравнивания потенциала, защиты от статического электричества и вторичных проявлений молнии все металлические нетоковедущие части электрооборудования, стальные конструкции должны быть присоединены к заземляющему устройству. Заземление оборудования КИП и материалов выполнить в соответствии с требованиями GLE-(GO-Z00000X0)-IN-SQ-004 Концепция заземления КИПиА.
6. Кабельные короба соединить с контуром заземления проводом в начале и конце трассы, в т. ч. в конце каждого ответвления. Секции коробов и их ответвления должны образовывать непрерывную электрическую цепь по всей длине трассы. Заземление выполнить проводом защитного заземления сечением 25 мм2 в желто-зеленой изоляции с термоусадочной трубкой черного цвета у наконечника. Заземление КИП, соединительных коробок, стоек выполнить проводом защитного заземления сечением 6 мм2 в желто-зеленой изоляции с термоусадочной трубкой черного цвета у наконечника.
7. Строительные конструкции показаны условно.
8. Нумерация строительных осей дана для справки.
9. Прокладку кабелей выполнить в соответствии с ПУЭ с учетом вида передаваемых сигналов и напряжений.
10. Установку кабельных конструкций, монтаж средств КИП выполнить после монтажа технологического оборудования.
11. Клеммные коробки устанавливаются на обслуживаемой высоте +1,700 от уровня пола или площадки обслуживания.
12. Высотные отметки кабельных лотков оборудования КИП уточнить по месту при монтаже.
13. Кабельные проходки А,Б и В учтены в GLE-(GO-D8810BX0)-FA-SPBA-001, кабельная проходка Г учтена в данном проекте.
14. Для дополнительных креплений кабеля в металлорукаве использовать Z-образный профиль Поз.24 и двухлапковые скобы Поз.23.
15. Монтаж датчиков загазованности на воздухозаборных трубах осуществить согласно 170323-(GO-Z00000X0)-IN-ZA-212.101

1-1
(1:10)

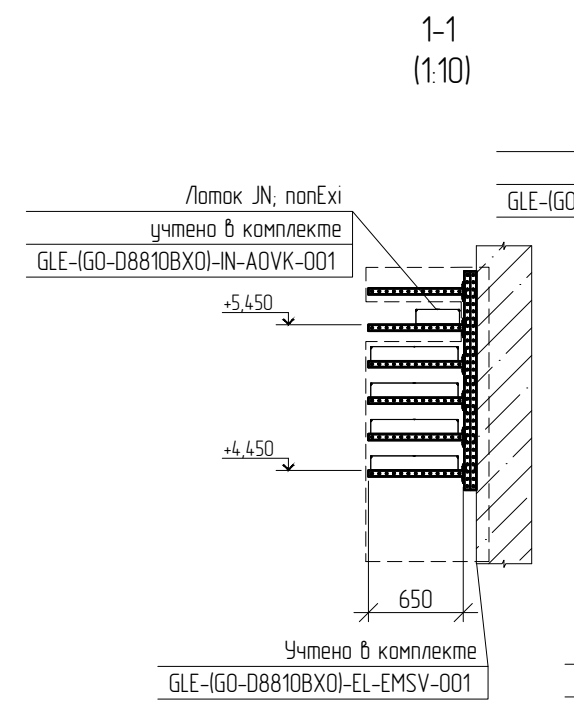

2-2
(1:10)

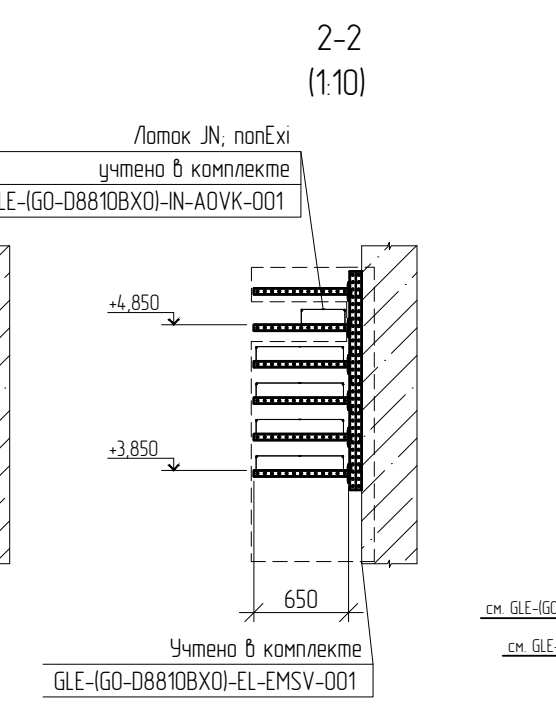

3-3
(1:10)

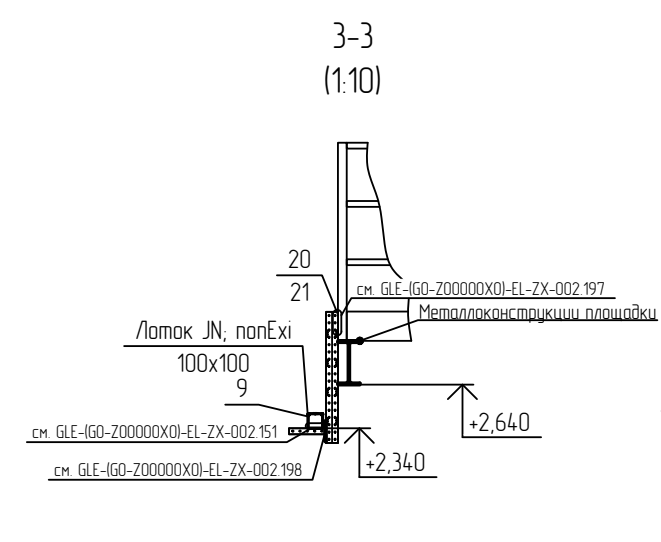

4-4
(1:10)

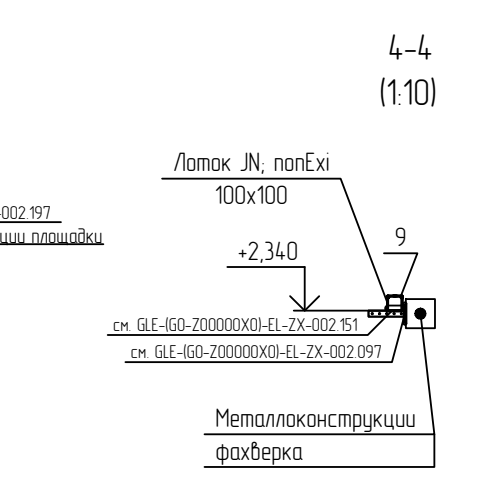

5-5
(1:10)

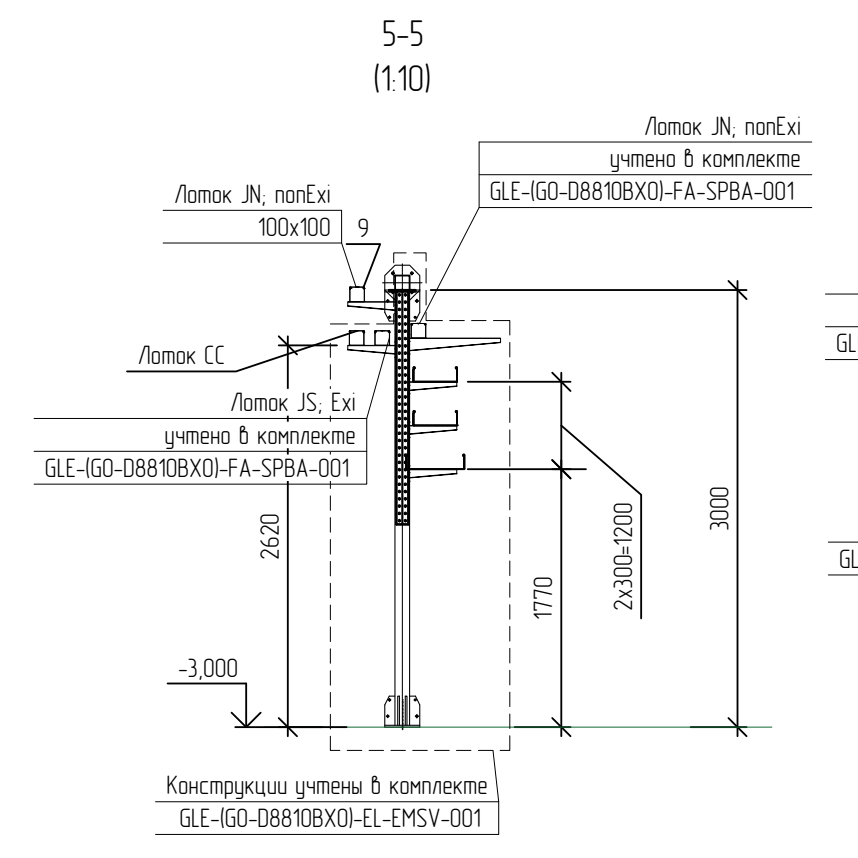

6-6
(1:10)

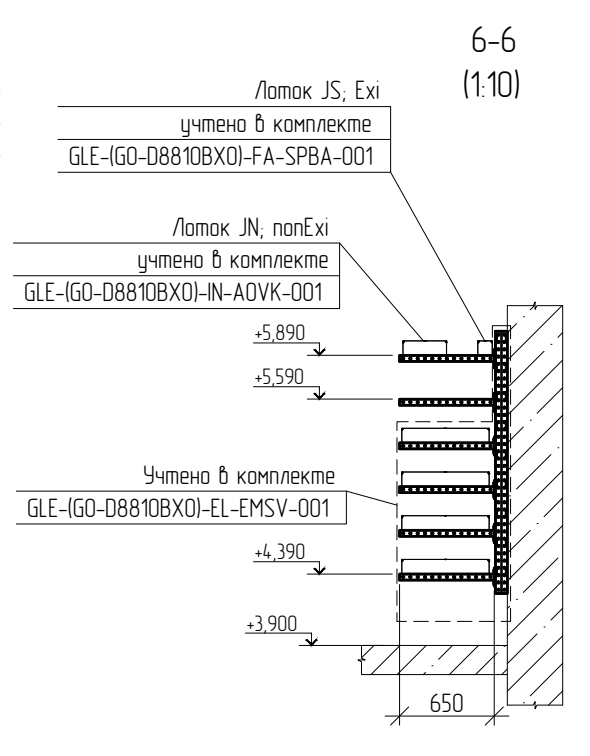

А

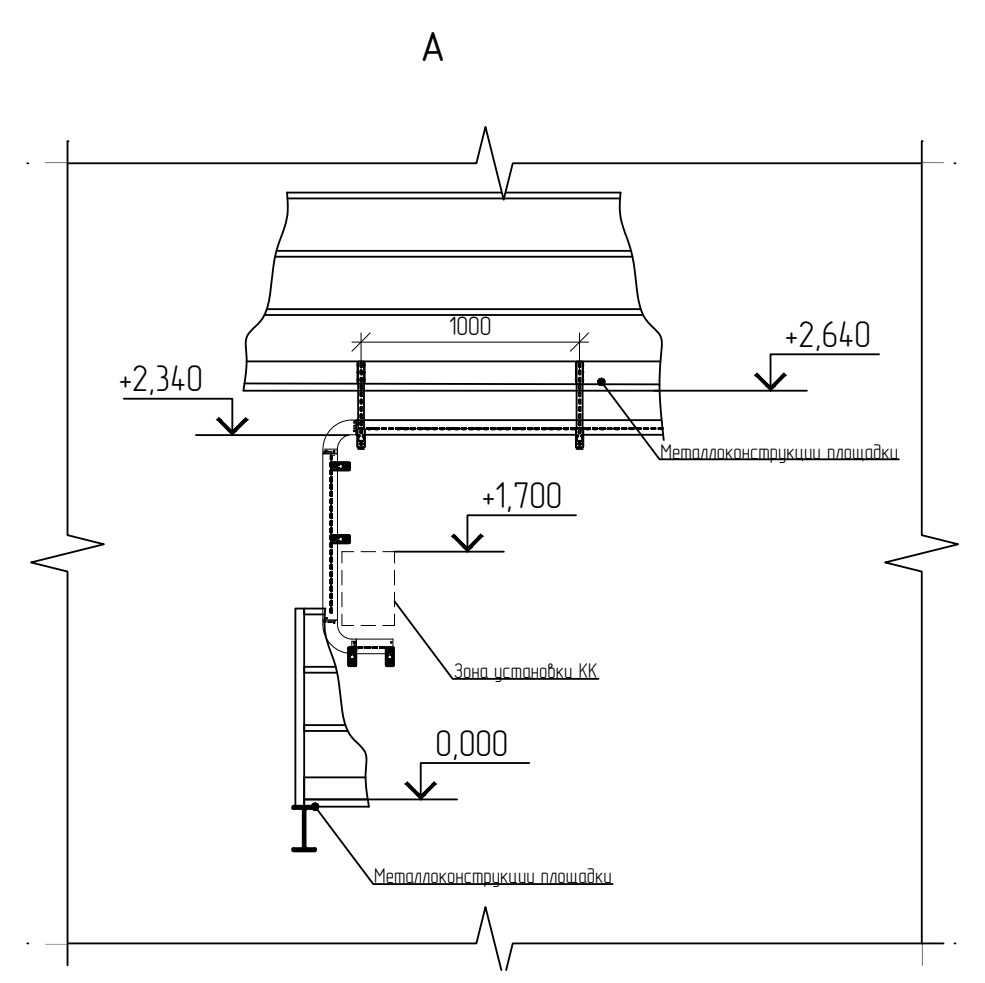

Проходка Г
тип 1

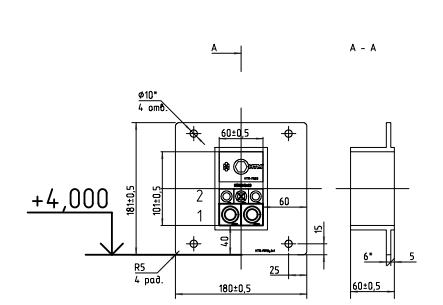

1
GO-93GT1009-CJ01
GO-93GT1010-CJ01
2
GO-D88LS1001-CJ01
Резерв
GO-D88LS1001-CJ02

Кабели учтены в комплекте GLE-(GO-D8810BX0)-IN-ASVK-001

Проходка В тип 2
Учтена в комплекте
GLE-(GO-D8810BX0)-FA-SPBA-001

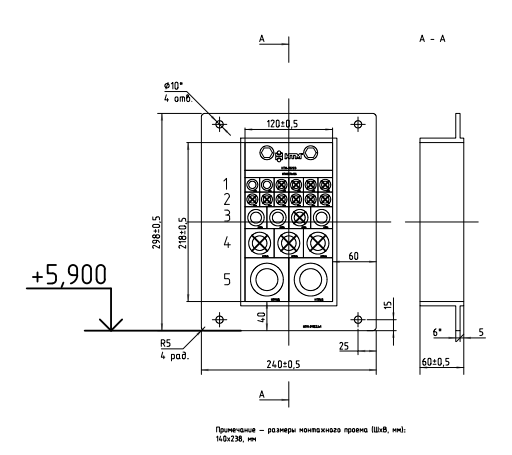

1
GO-D88TE1220A-CJ01
GO-D88TE1220B-CJ01
Резерв
Резерв
Резерв
Резерв
2
Резерв
Резерв
Резерв
Резерв
Резерв
Резерв
3
GO-93GT1009-CJ01
GO-93GT1010-CJ01
Резерв
GO-D8880FX0-JU01-JBZE1005-CM01
4
Резерв
Резерв
Резерв
5
GO-D8801FX0-JU01-JBNE1002-CJ01
GO-D8801FX0-JU01-JBNE1003-CJ01

Кабели учтены в комплекте GLE-(GO-D8810BX0)-IN-AOVK-001

Кабели учтены в комплекте GLE-(GO-D8810BX0)-FA-SPBA-001

7.1-7.1
(1:10)

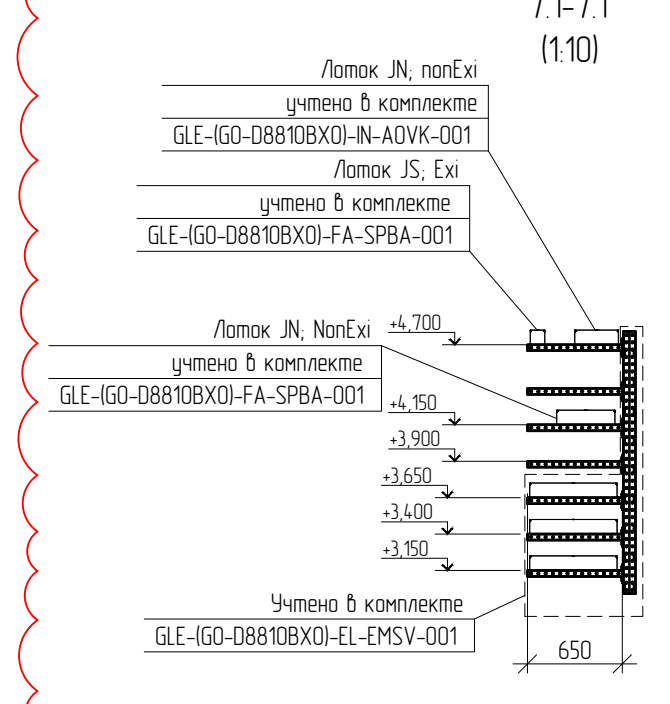

7.2-7.2
(1:10)

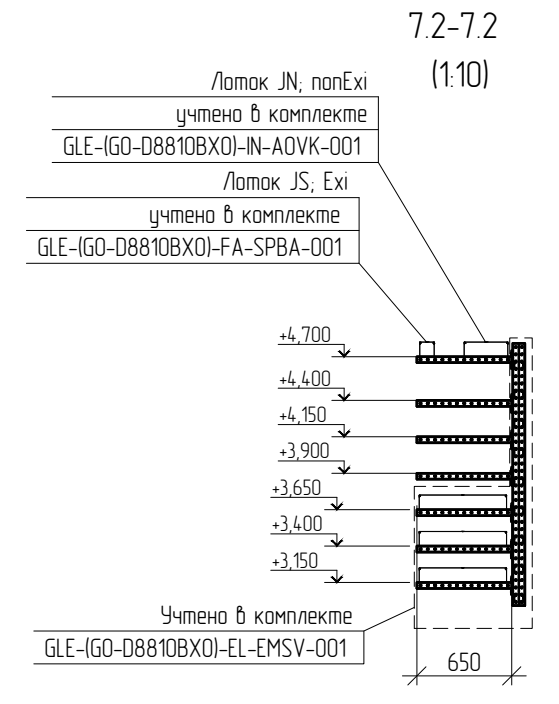

8-8
(1:10)

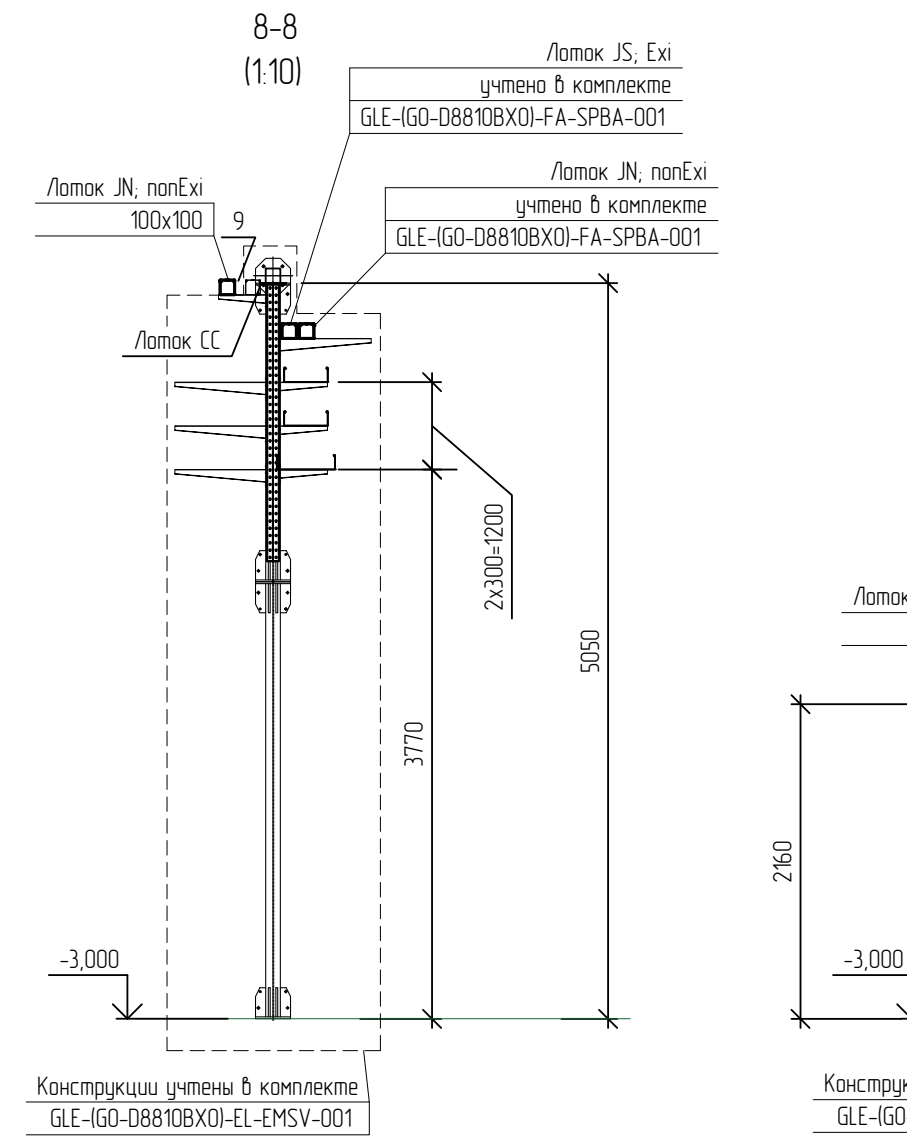

9-9
(1:10)

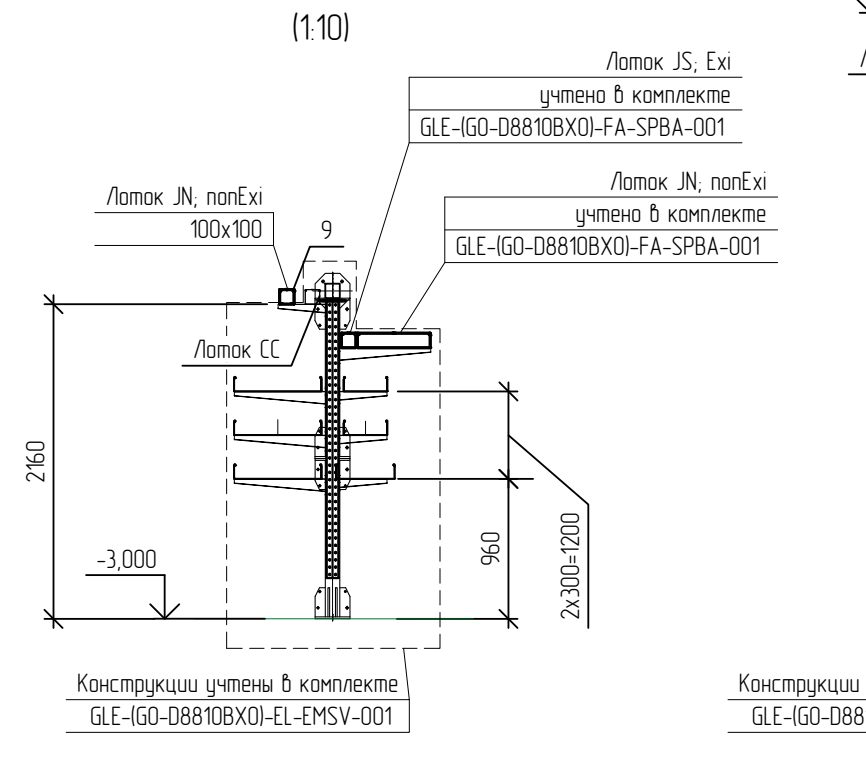

10-10
(1:10)

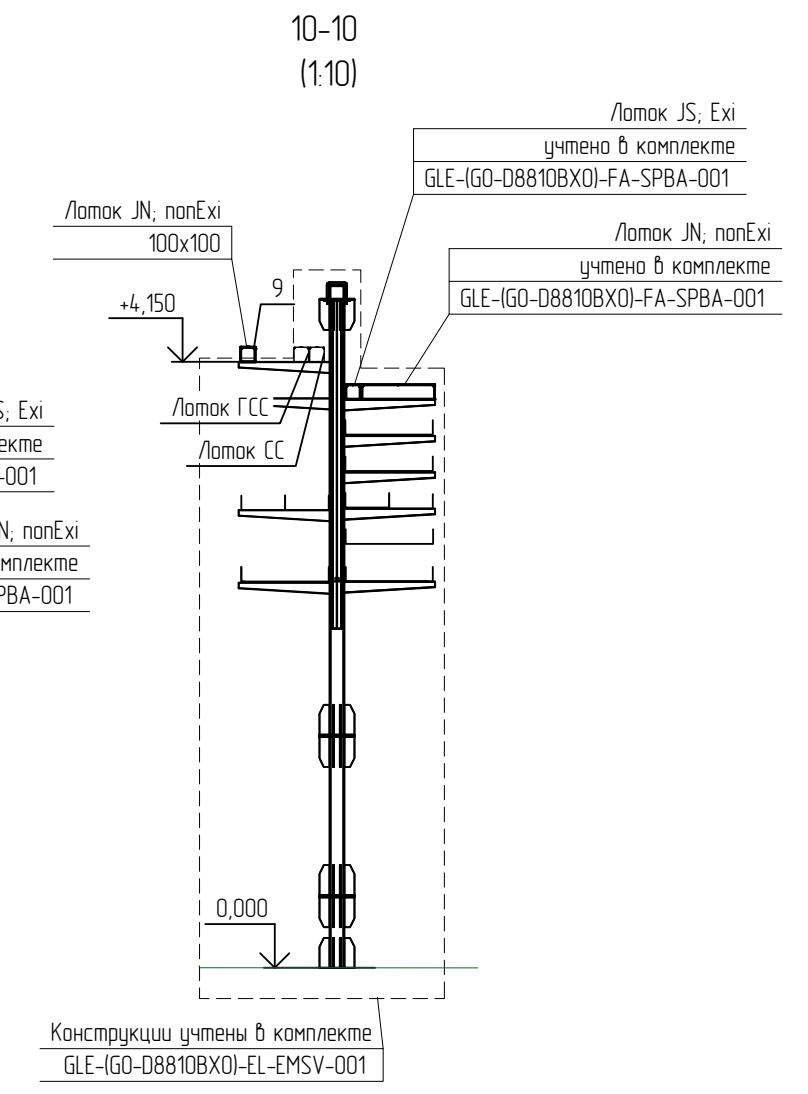

11-11
(1:10)

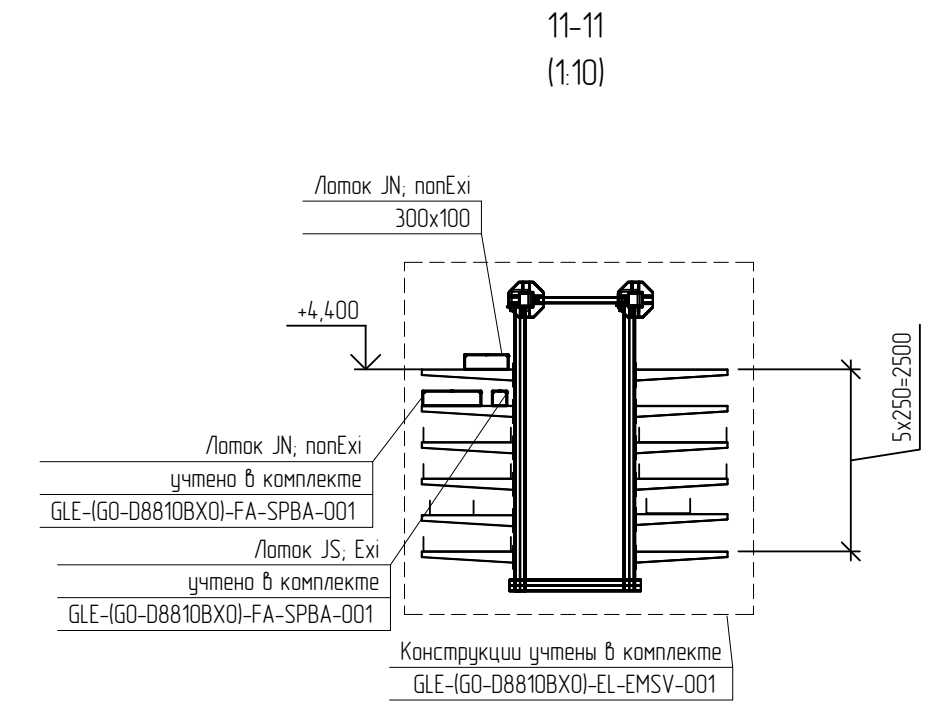

Проходка А тип 3
(учтено в GLE-(GO-D8810BX0)-FA-SPBA-001)

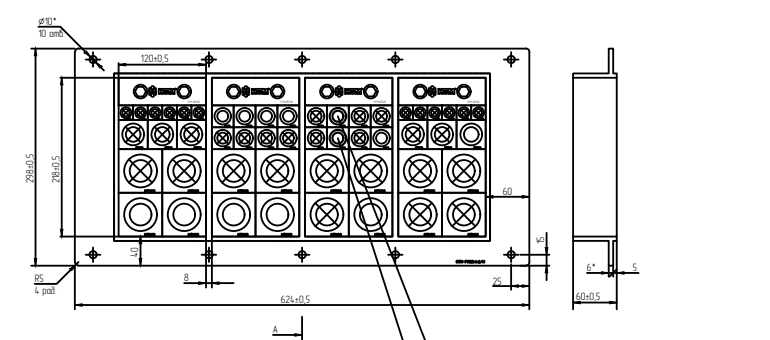

GO-D8810BX0-JG01-JBNE1001-CJ01
GO-D8810BX0-JG01-JBNE1002-CJ01

Проходка Б тип 3
(учтено в GLE-(GO-D8810BX0)-FA-SPBA-001)

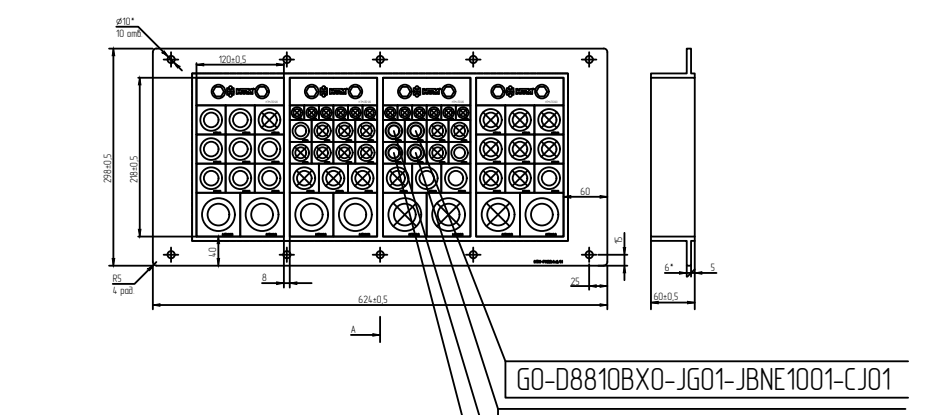

GO-D8810BX0-JG01-JBNE1001-CJ01
GO-D8810BX0-JG01-JBNE1002-CJ01
GO-93GT1009-CJ01
GO-93GT1010-CJ01

СИТУАЦИОННЫЙ ПЛАН

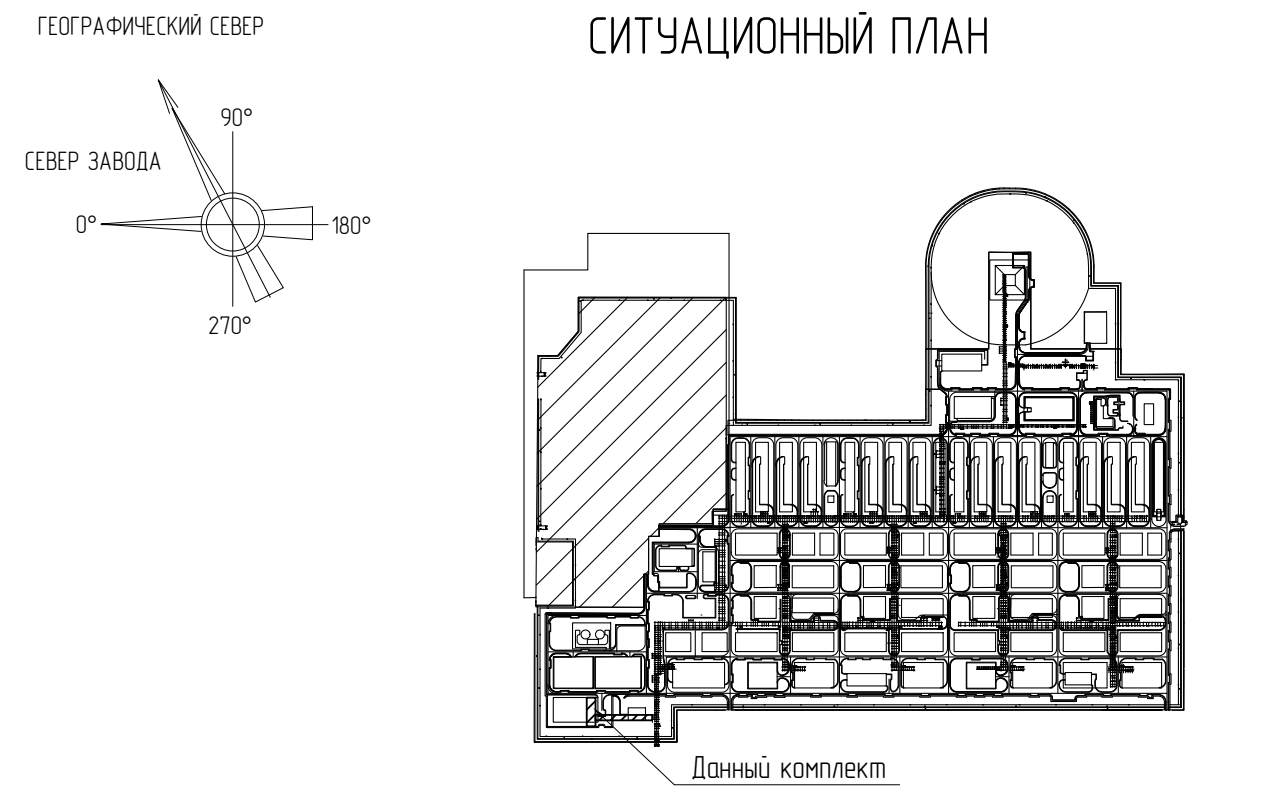

				Поминова	Тулба	Трофимов
IFC	03	04.12.25	Выпущено для строительства / Issued for Construction	Поминова	Тулба	Трофимов
IFC	02H	21.03.25	Выпущено для строительства / Issued for Construction	Шевцова	Охота	Подземельнов
IFR	01H	23.08.24	Выпущено для рассмотрения / Issued for Review	Гайсина	Гильманова	Трофимов
Статус Status	Рев. Rev.	Дата Date	Назначение выпуска / Reason for Issue	Разраб. Drawn	Провер. Checked	Утверд. Approved

GAS PROCESSING COMPLEX WITHIN UST-LUGA ETHANE-RICH GAS PROCESSING CLUSTER. GAS PROCESSING PLANT AND UTILITIES, INFRASTRUCTURE AND OFFSITE PROCESS FACILITIES

GO-D8810BX0
Fire Water Pump Station

Stage	Sheet	Total Sheets
DDD	10	

Instrument and Cable Routing Plans
at el. 0,000; -3,000

РУСХИМАЛЬЯНС

GLE-(GO-D8810BX0)-IN-GDSS-001

ГАЗОПЕРЕРАБАТЫВАЮЩИЙ КОМПЛЕКС В СОСТАВЕ КОМПЛЕКСА ПЕРЕРАБОТКИ ЭТАНОСОДЕРЖАЩЕГО ГАЗА В РАЙОНЕ ПОСЕЛКА УСТЬ-ЛУГА. ГАЗОПЕРЕРАБАТЫВАЮЩИЙ ЗАВОД И ТЕХНОЛОГИЧЕСКИЕ ОБЪЕКТЫ ОБЩЕЗАВОДСКОГО ХОЗЯЙСТВА

Изм.	Кол.уч.	Лист	№док.	Подпись	Дата
Разраб.		Поминова			04.12.25
Проверил		Тулба			04.12.25
Нач. сект		Савчук			04.12.25
Н. контр.		Тулба			04.12.25
ГИП		Трофимов			04.12.25

GO-D8810BX0
Насосная станция противопожарного водоснабжения

Стадия	Лист	Листов
Р	10	

План расположения КИПиА и прокладки кабельных трасс на отм. 0,000; -3,000

ГЛИнжиниринг
ПРОЕКТИРУЕМ БУДУЩЕЕ ОТРАСЛИ

GLE-(GO-D8810BX0)-IN-GDSS-001_03_AL.dwg

Формат А1х3

Instrument and Cable Routing Plan at el. 0,000, -3,000 (1:100)

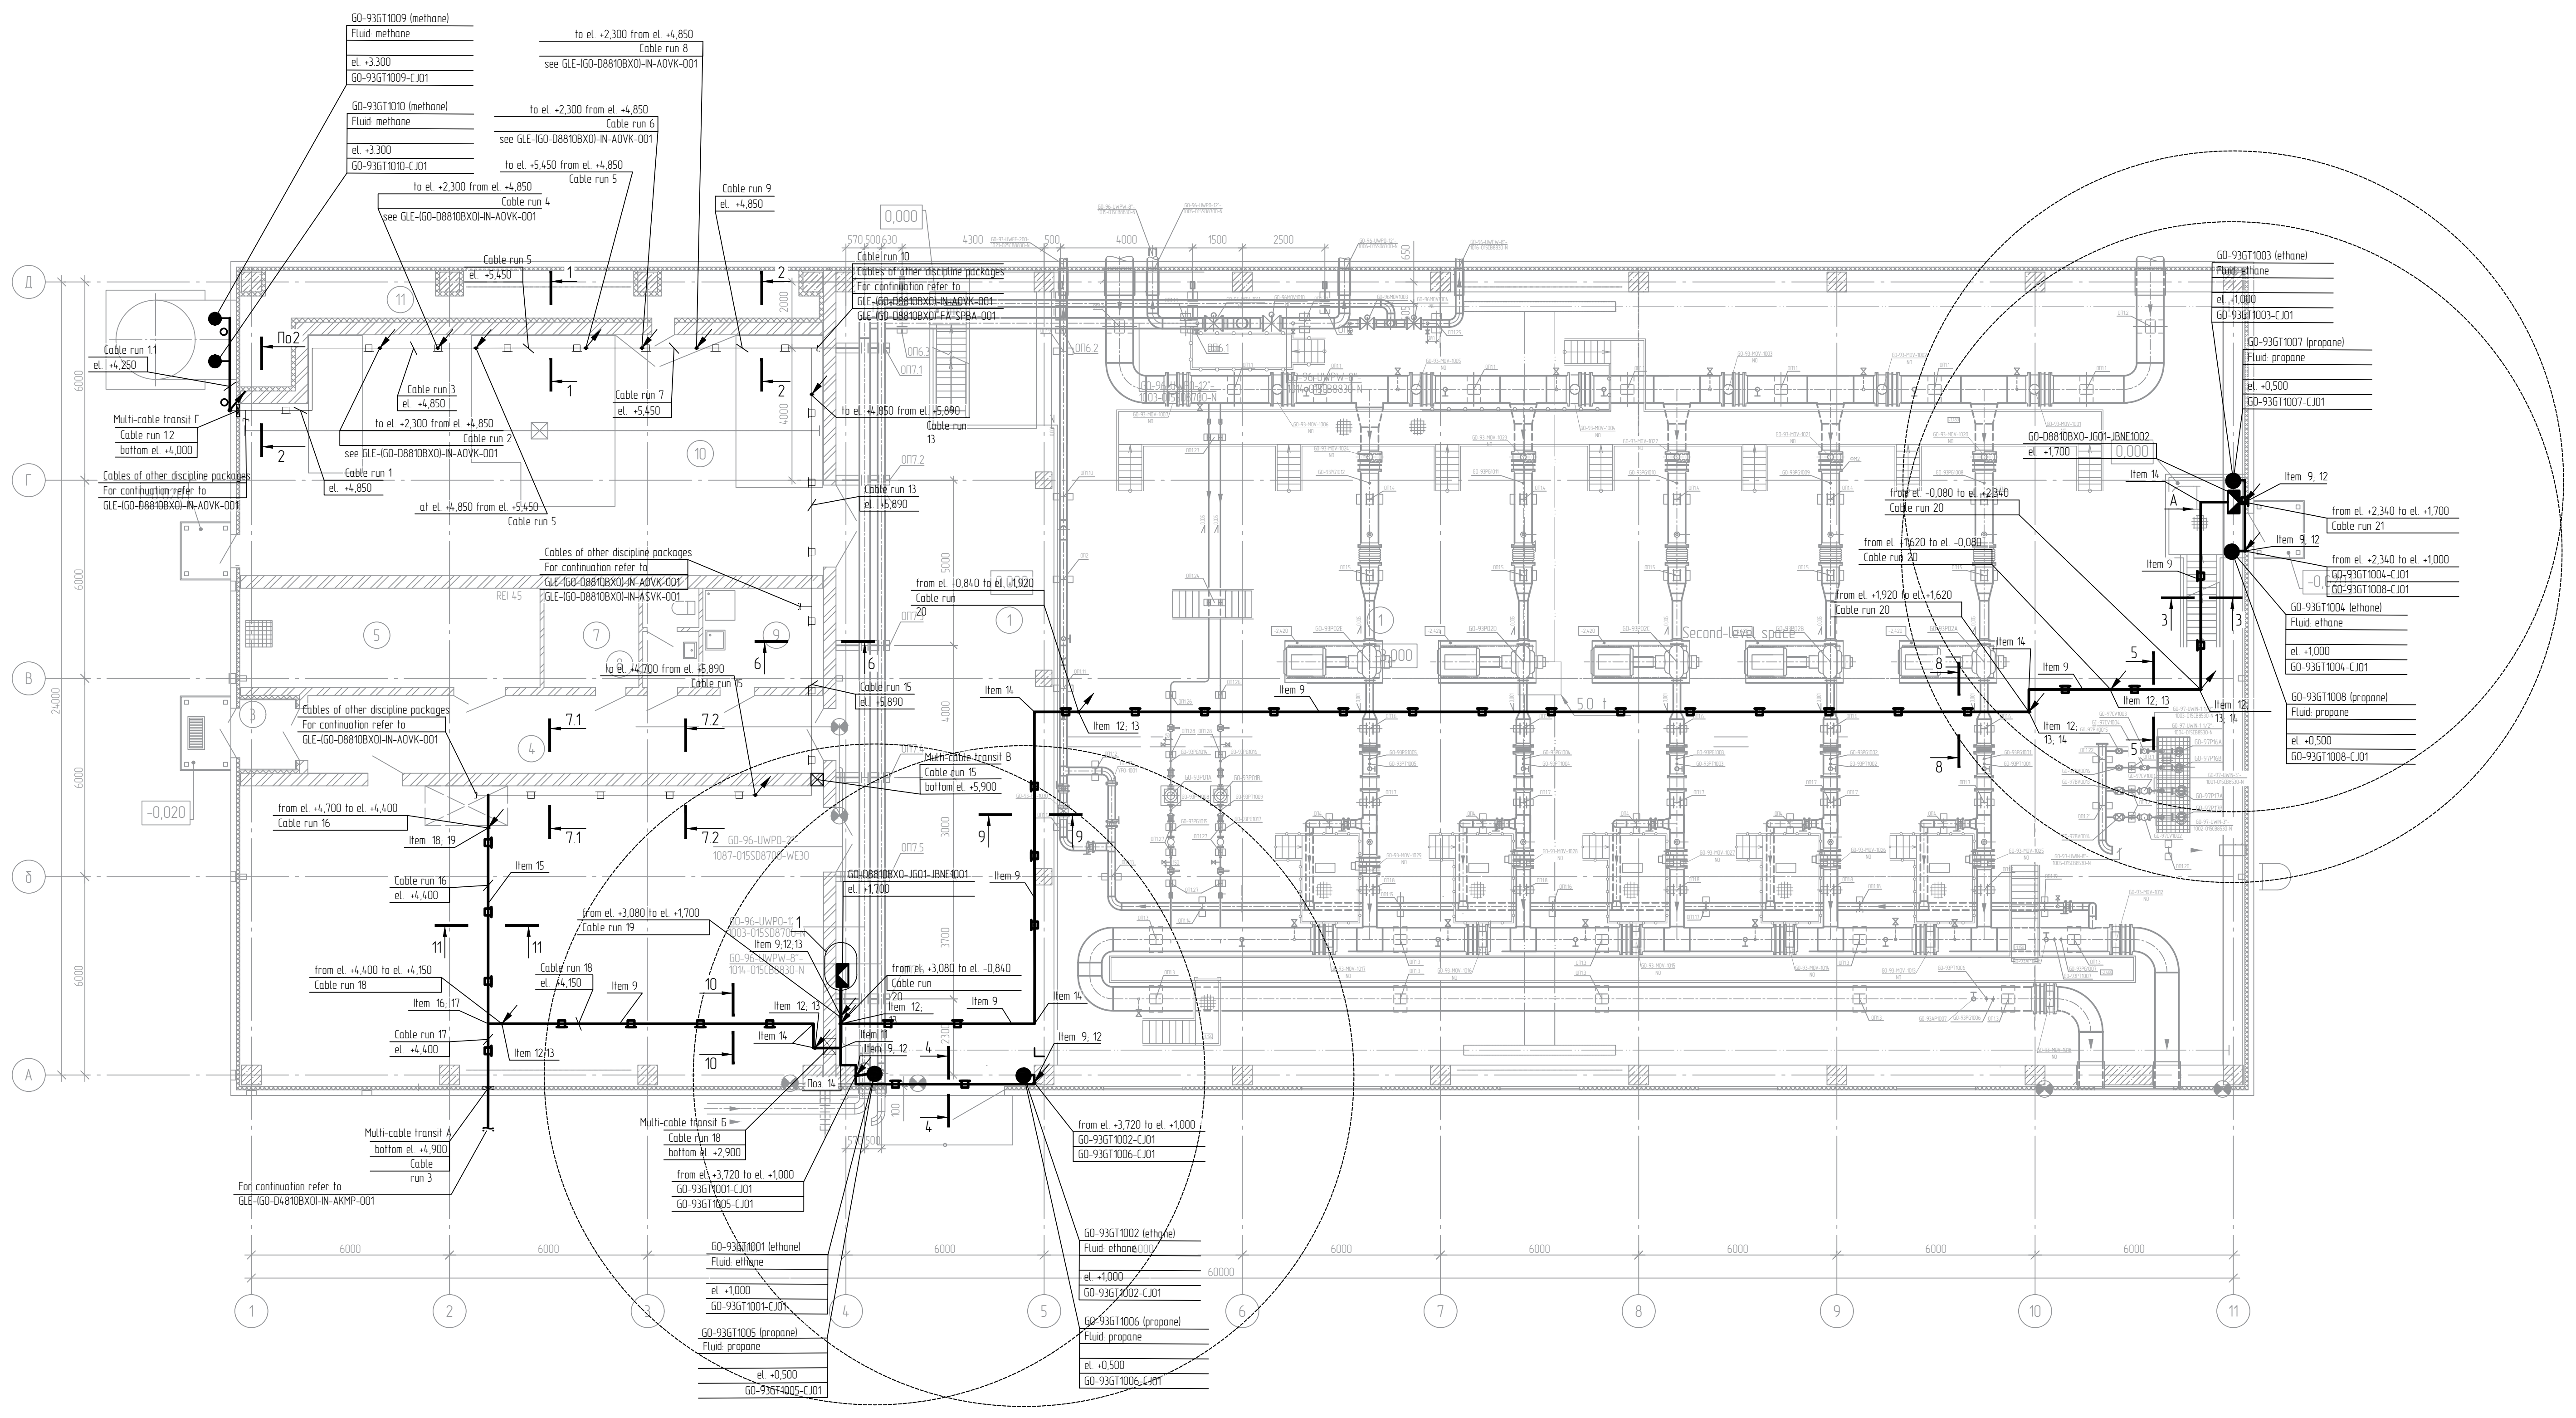

Cable run 1.1

Flexible conduit DN25
GO-93GT1009-CJ01
Flexible conduit DN25
GO-93GT1010-CJ01

Cable run 1.2

Multi-cable transit Г
GO-93GT1009-CJ01
GO-93GT1010-CJ01
GO-D88LS1001-CJ01
GO-D88LS1001-CJ02

Cables are included in package GLE-(GO-D8810BX0)-IN-ASVK-001

Cable run 1

Cable tray 300 x 100 JN
GO-D88TE1021A-CJ01
GO-D88TE1021B-CJ01
GO-D88TV1216A-CJ01
GO-D88PS1217A-CJ01
GO-D88TV1216B-CJ01
GO-D88PS1217B-CJ01
GO-D88TE1206A-CJ01
GO-D88TE1206B-CJ01
GO-D88LS1001-CJ01
GO-D88LS1001-CJ02
GO-93GT1009-CJ01
GO-93GT1010-CJ01

Cables are included in package GLE-(GO-D8810BX0)-IN-ASVK-001

Cables are included in package GLE-(GO-D8810BX0)-IN-AOVK-001

Cable run 2

Not applicable

Cable run 3

Cable tray 300 x 100 JN
GO-D88TE1220A-CJ01
GO-D88TE1220B-CJ01
GO-D88TE1230A-CJ01
GO-D88TE1230B-CJ01
GO-D88TE1021A-CJ01
GO-D88TE1021B-CJ01
GO-D88LS1001-CJ01
GO-D88LS1001-CJ02
GO-93GT1009-CJ01
GO-93GT1010-CJ01

Cables are included in package GLE-(GO-D8810BX0)-IN-ASVK-001

Cables are included in package GLE-(GO-D8810BX0)-IN-AOVK-001

Cable run 4

Not applicable

Cable run 5

Cable tray 300 x 100 JN
GO-D88TE1220A-CJ01
GO-D88TE1220B-CJ01
GO-D88TE1230A-CJ01
GO-D88TE1230B-CJ01
GO-D88TE1430-CJ01
GO-D88TE1021A-CJ01
GO-D88TE1021B-CJ01
GO-D88LS1001-CJ01
GO-D88LS1001-CJ02
GO-93GT1009-CJ01
GO-93GT1010-CJ01

Cables are included in package GLE-(GO-D8810BX0)-IN-ASVK-001

Cables are included in package GLE-(GO-D8810BX0)-IN-AOVK-001

Cable run 6

Not applicable

Cable run 7

Cable tray 300 x 100 JN
GO-D88TE1220A-CJ01
GO-D88TE1220B-CJ01
GO-D88TE1230A-CJ01
GO-D88TE1230B-CJ01
GO-D88TE1430-CJ01
GO-D88TE1021B-CJ01
GO-D88TE1030A-CJ01
GO-D88TV1116A-CJ01
GO-D88PS1117A-CJ01
GO-D88TE1106A-CJ01
GO-D88TE1221A-CJ01
GO-D8810BX0-JP01-JBNE1003A-CJ01
GO-D88LS1001-CJ01
GO-D88LS1001-CJ02
GO-93GT1009-CJ01
GO-93GT1010-CJ01

Cables are included in package GLE-(GO-D8810BX0)-IN-AOVK-001

Cables are included in package GLE-(GO-D8810BX0)-IN-ASVK-001

Cable run 8

Not applicable

Cable run 9

Cable tray 300 x 100 JN
GO-D88TE1220A-CJ01
GO-D88TE1220B-CJ01
GO-D88TE1230A-CJ01
GO-D88TE1230B-CJ01
GO-D88TE1430-CJ01
GO-D88TE1030A-CJ01
GO-D88TE1022A-CJ01
GO-D88TV1116A-CJ01
GO-D88PS1117A-CJ01
GO-D88TE1106A-CJ01
GO-D88TE1030B-CJ01
GO-D88TE1022B-CJ01
GO-D88TV1116B-CJ01
GO-D88PS1117B-CJ01
GO-D88TE1106B-CJ01
GO-D88TE1221A-CJ01
GO-D88TE1221B-CJ01
GO-D8810BX0-JP01-JBNE1003A-CJ01
GO-D8810BX0-JP01-JBNE1003B-CJ01
GO-D88LS1001-CJ01
GO-D88LS1001-CJ02
GO-93GT1009-CJ01
GO-93GT1010-CJ01

Cables are included in package GLE-(GO-D8810BX0)-IN-AOVK-001

Cables are included in package GLE-(GO-D8810BX0)-IN-ASVK-001

Cable run 10

Not applicable

Cable run 11

Not applicable

Cable run 12

Not applicable

Cable run 13

Cable tray 300 x 100 JN
GO-D88TE1220A-CJ01
GO-D88TE1220B-CJ01
GO-D88TV1116A-CJ01
GO-D88PS1117A-CJ01
GO-D88TE1106A-CJ01
GO-D88TV1116B-CJ01
GO-D88PS1117B-CJ01
GO-D88TE1106B-CJ01
GO-D8810BX0-JP01-JBNE1003A-CJ01
GO-D8810BX0-JP01-JBNE1003B-CJ01
GO-D88LS1001-CJ01
GO-D88LS1001-CJ02
GO-D8801FX0-JU01-JBNE1002-CJ01
GO-D8801FX0-JU01-JBNE1003-CJ01
GO-93GT1009-CJ01
GO-93GT1010-CJ01

Cables are included in package GLE-(GO-D8810BX0)-IN-ASVK-001

Cables are included in package GLE-(GO-D8810BX0)-IN-AOVK-001

Cables are included in package GLE-(GO-D8810BX0)-FA-SPBA-001

Cable run 14

Not applicable

Cable run 15

Cable tray 300 x 100 JN
GO-D88TE1220A-CJ01
GO-D88TE1220B-CJ01
GO-D8801FX0-JU01-JBNE1002-CJ01
GO-D8801FX0-JU01-JBNE1003-CJ01
GO-93GT1009-CJ01
GO-93GT1010-CJ01

Cables are included in package GLE-(GO-D8810BX0)-IN-AOVK-001

Cables are included in package GLE-(GO-D8810BX0)-FA-SPBA-001

Cable run 16

Cable tray 300 x 100 JN
GO-D8801FX0-JU01-JBNE1002-CJ01
GO-D8801FX0-JU01-JBNE1003-CJ01
GO-93GT1009-CJ01
GO-93GT1010-CJ01

Cables are included in package GLE-(GO-D8810BX0)-FA-SPBA-001

Cable run 17

Cable tray 300 x 100 JN
GO-D8801FX0-JU01-JBNE1002-CJ01
GO-D8801FX0-JU01-JBNE1003-CJ01
GO-D8810BX0-JG01-JBNE1001-CJ01
GO-D8810BX0-JG01-JBNE1002-CJ01

Cables are included in package GLE-(GO-D8810BX0)-FA-SPBA-001

Cable run 18

Cable tray 100 x 100 JN
GO-D8810BX0-JG01-JBNE1001-CJ01
GO-D8810BX0-JG01-JBNE1002-CJ01
GO-93GT1009-CJ01
GO-93GT1010-CJ01

Cable run 19

Cable tray 100 x 100 JN
GO-D8810BX0-JG01-JBNE1001-CJ01
GO-93GT1009-CJ01
GO-93GT1010-CJ01
GO-93GT1001-CJ01
GO-93GT1002-CJ01
GO-93GT1005-CJ01
GO-93GT1006-CJ01

Cable run 20

Cable tray 100 x 100 JN
GO-D8810BX0-JG01-JBNE1002-CJ01

Cable run 21

Cable tray 100 x 100 JN
GO-D8810BX0-JG01-JBNE1002-CJ01
GO-93GT1004-CJ01
GO-93GT1008-CJ01

Symbols

Symbol	Description
─□─□─	Cable routed in cable tray / cable duct included in the scope of supply GLE-(GO-D8810BX0)-IN-AOVK-001
━■━■━	Cable routed in cable tray / cable duct included in the scope of supply GLE-(GO-D8810BX0)-IN-GDSS-001
─○─○─	Cables routed in conduit
✉	Junction box
↗ ↙	Cable rise/cable drop
↙ ↗	Cable drop/cable rise
⊙	Gas detector, sensing radius 10m
GO-93GT1001-CJ01	Cable tag
Cable tray 100 x 100 JN	Cable tray 100x100 for instrumentation

Abbreviations

TE – telecom cables (not covered in this document)
EL – electrical cables (not covered in this document)
AFA&FFS – fire alarm cables (not covered in this document)
I&C – instrument cables (not covered in this document)
JS – instrument cables (intrinsically safe, not covered in this document)
JN – instrument cables (non-intrinsically safe)

1. Relative elevation –3,000 for machine room corresponds to the high concrete paving point. Base datum level (BDL) 0,000 corresponds to absolute elevation +27,000 (Baltic System).

2. Scale 1:100.

3. Cable connection to instruments and junction boxes, cable protection with flexible conduit, cable entry installation and earthing of the above equipment and materials shall be provided in accordance with electrical wiring diagrams for instrumentation GLE-(GO-Z00000X0)-IN-ZX-001.

4. Instruments, junction boxes shall be installed in accordance with GLE-(GO-Z00000X0)-IN-ZX-002 Mechanical Instrumentation Hook-Up Drawings. GO-D8810BX0-JG01-JBNE1001, GO-D8810BX0-JG01-JBNE1002 shall be installed as per typical detail KM211-31 Junction Box Mounted on Stanchion Embedded in Concrete Floor. Gas detectors at el.. –3,000 shall be installed as per typical detail KM112-22.

5. To protect personnel against electric shock and ensure equipotential bonding, electrostatic discharge protection and protection against secondary lightning effects, all non-current-carrying metal parts of electrical equipment, as well as steel structures shall be connected to an earthing arrangement. Instrumentation equipment and materials shall be earthed in accordance with the requirements of GLE-(GO-Z00000X0)-IN-SQ-004 I&C Earthing Concept.

6. Cable ducts shall be connected to the earthing loop by wire at the beginning and at the end of the cable route, as well as at the end of each branch connection.. Sections and branch connections of cable ducts shall provide a continuous electrical circuit along the entire length of the route. Earthing shall be provided by means of a 25 mm2 protective earthing wire with a yellow-green insulation and black heat shrinkable tube near the lug. Instruments, junction boxes, and supports shall be earthed with a 6 mm2 protective earthing wire with a yellow-green insulation and black heat shrinkable tube near the lug.

7. Civil structures are shown indicative.

8. Grid line numbering is shown indicative.

9. Cables shall be routed as per PUE requirements taking into account the type of transmitted signals and voltage.

10. Installation of cable supports and instruments shall be performed after installation of process equipment.

11. Junction boxes shall be installed at elevation of +1,700 from the floor level or access platform.

12. Instrument cable tray elevations shall be confirmed on site during installation.

13. Multi-cable transits A, Б and B are included in GLE-(GO-D8810BX0)-FA-SPBA-001, multi-cable transit Г is included herein.

14. Z-shape (item 24) and two-hole clamps (item 23) shall be used for additional fasteners for cable fastening in flexible conduit. .

15. Gas detectors on air intake ducts shall be installed in accordance with 170323-(GO-Z00000X0)-IN-ZA-212.101

1-1 (1:10)

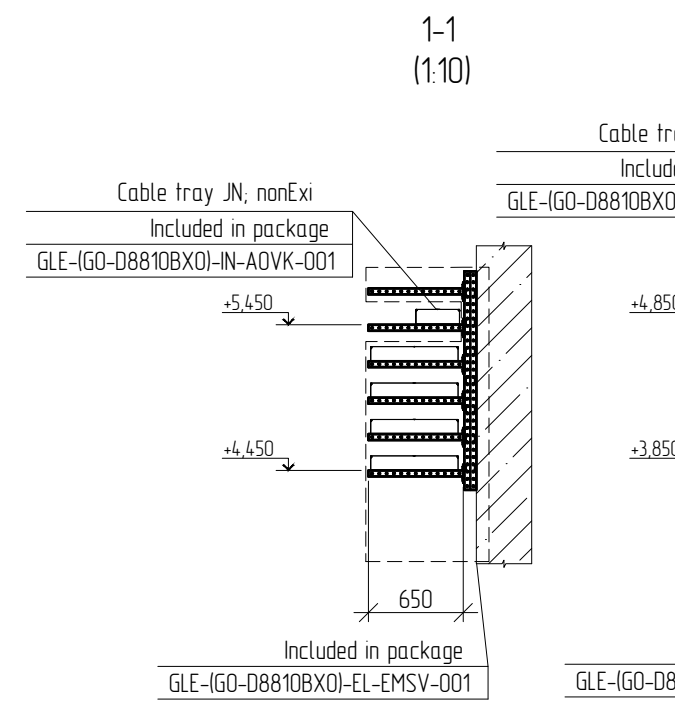

2-2 (1:10)

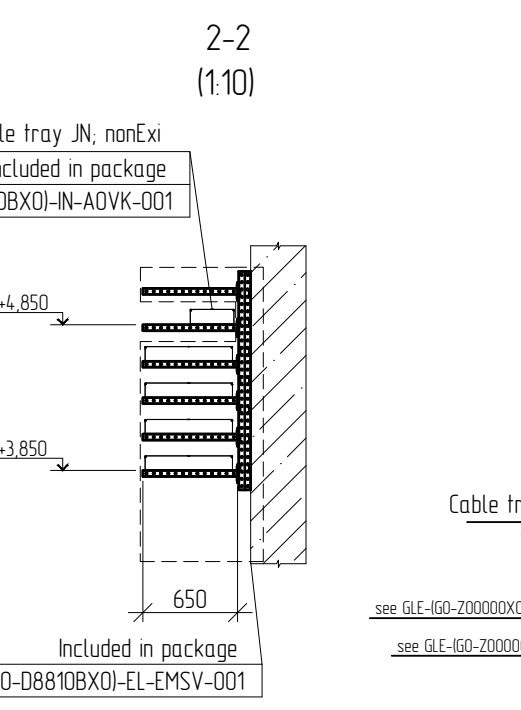

3-3 (1:10)

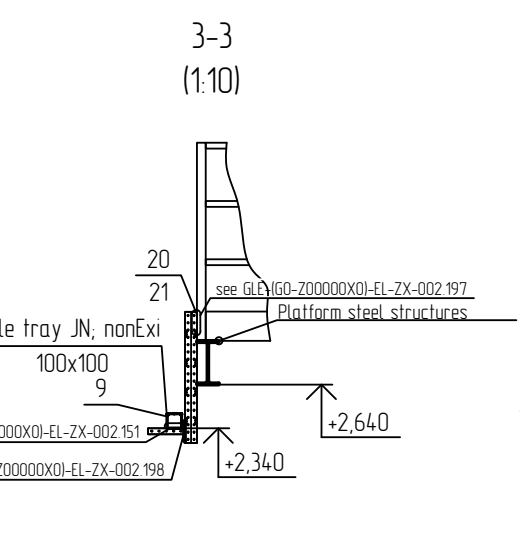

4-4 (1:10)

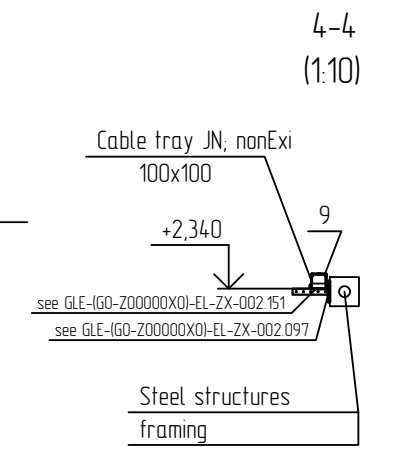

5-5 (1:10)

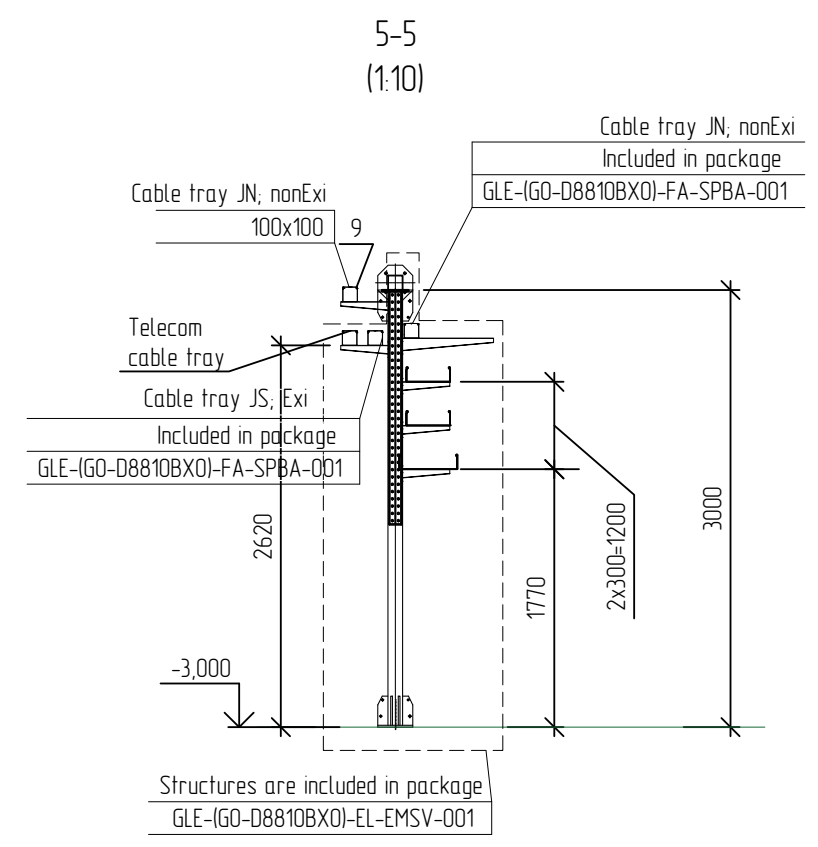

6-6 (1:10)

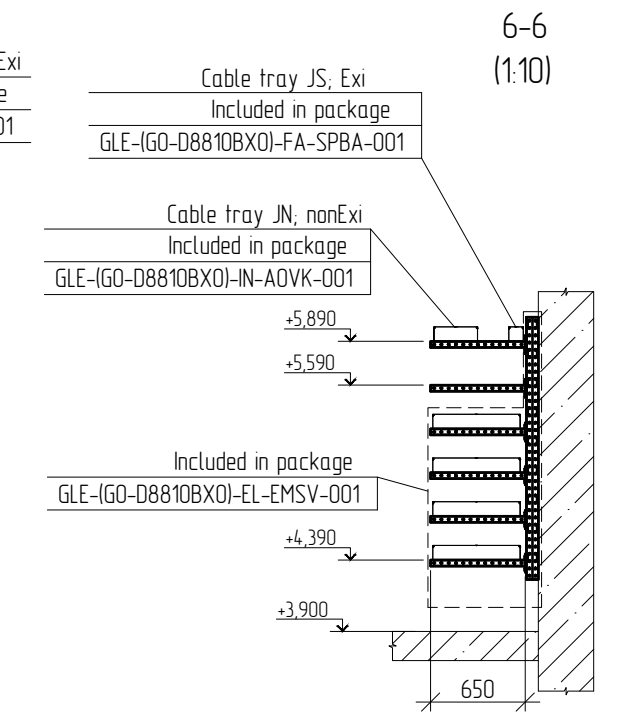

A

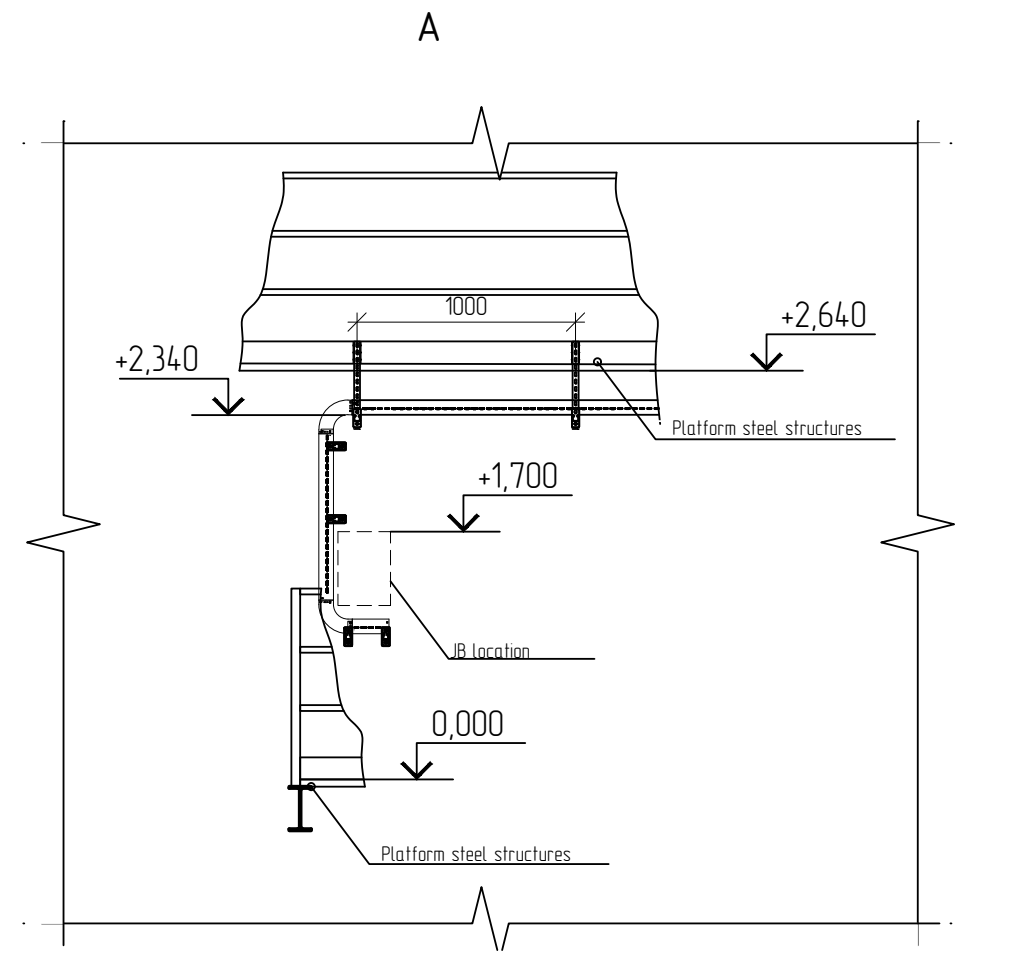

Multi-cable transit Г type 1

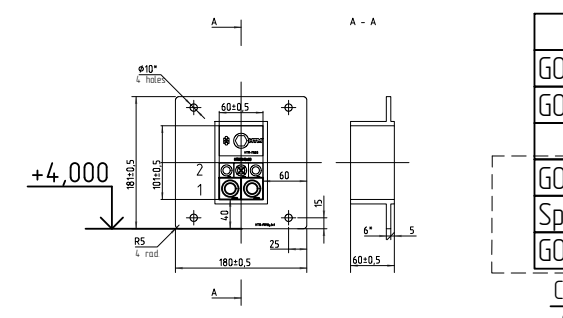

1
GO-93GT1009-CJ01
GO-93GT1010-CJ01
2
GO-D88LS1001-CJ01
Spare
GO-D88LS1001-CJ02

Cables are included in package GLE-(GO-D8810BX0)-IN-ASVK-001

Multi-cable transit B, type 2 Included in package GLE-(GO-D8810BX0)-FA-SPBA-001

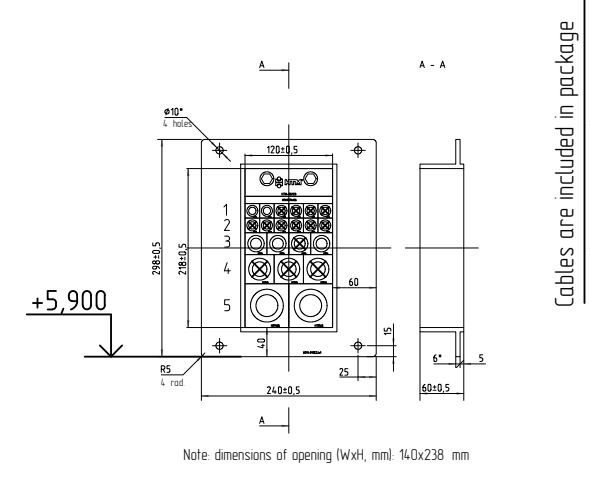

1
GO-D88TE1220A-CJ01
GO-D88TE1220B-CJ01
Spare
Spare
Spare
Spare
2
Spare
Spare
Spare
Spare
Spare
Spare
3
GO-93GT1009-CJ01
GO-93GT1010-CJ01
Spare
GO-D8880FX0-JU01-JBZE1005-CM01
4
Spare
Spare
Spare
5
GO-D8801FX0-JU01-JBNE1002-CJ01
GO-D8801FX0-JU01-JBNE1003-CJ01

Cables are included in package GLE-(GO-D8810BX0)-IN-AOVK-001

Cables are included in package GLE-(GO-D8810BX0)-FA-SPBA-001

7.1-7.1 (1:10)

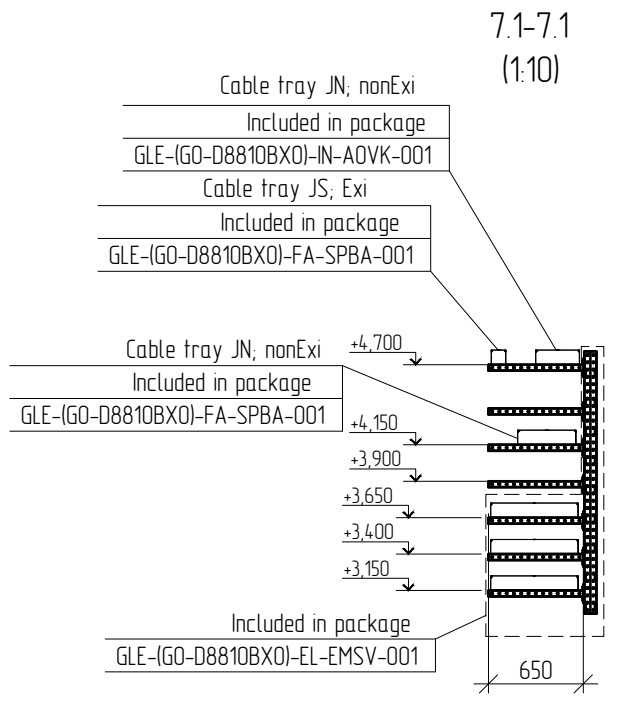

7.2-7.2 (1:10)

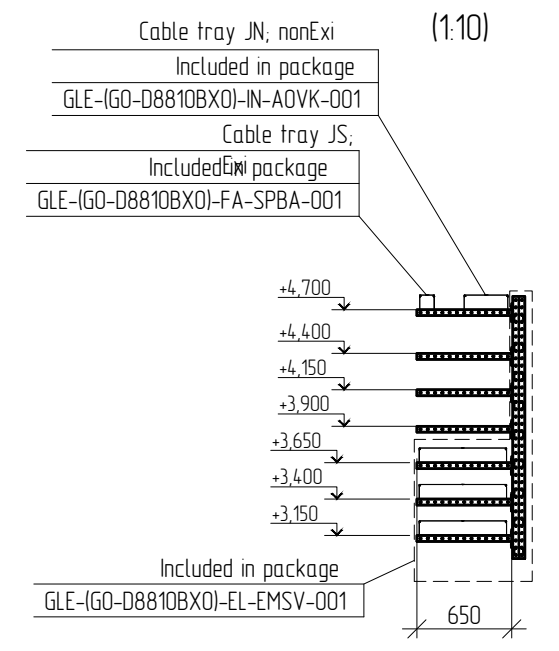

8-8 (1:10)

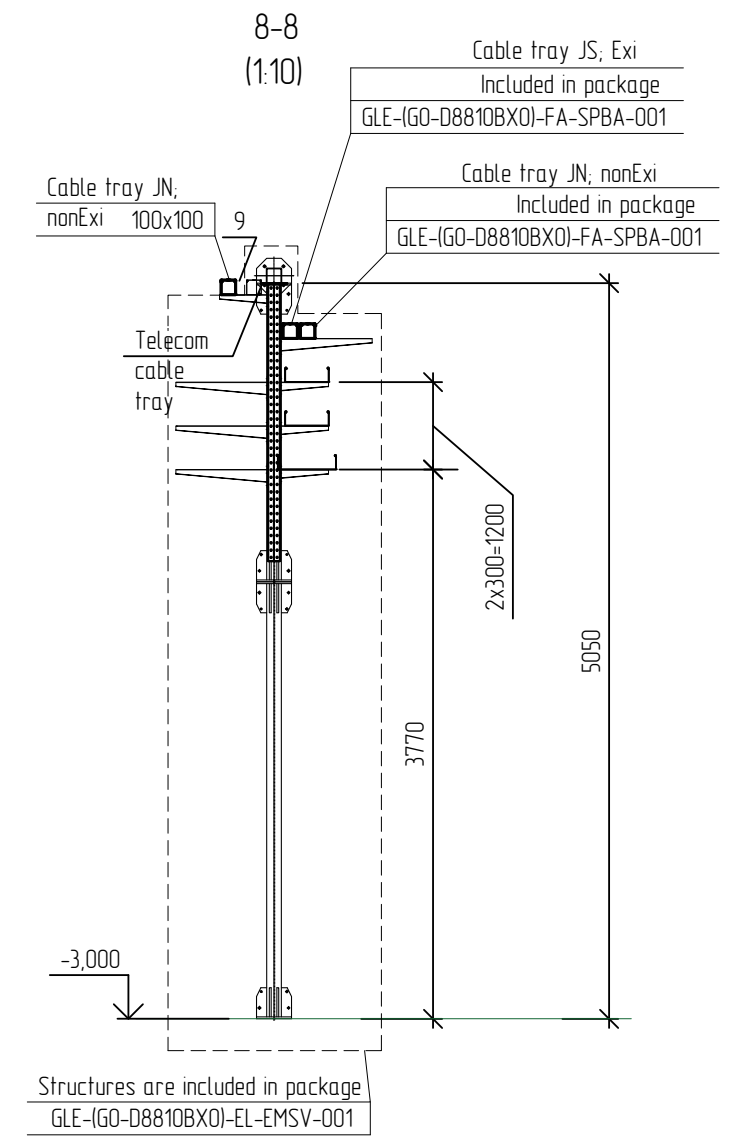

9-9 (1:10)

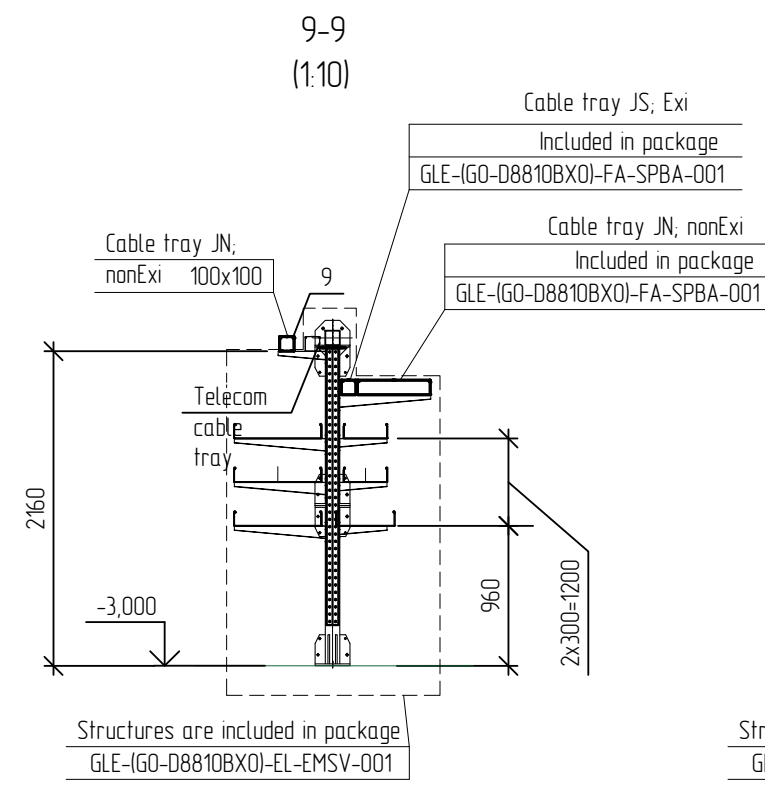

10-10 (1:10)

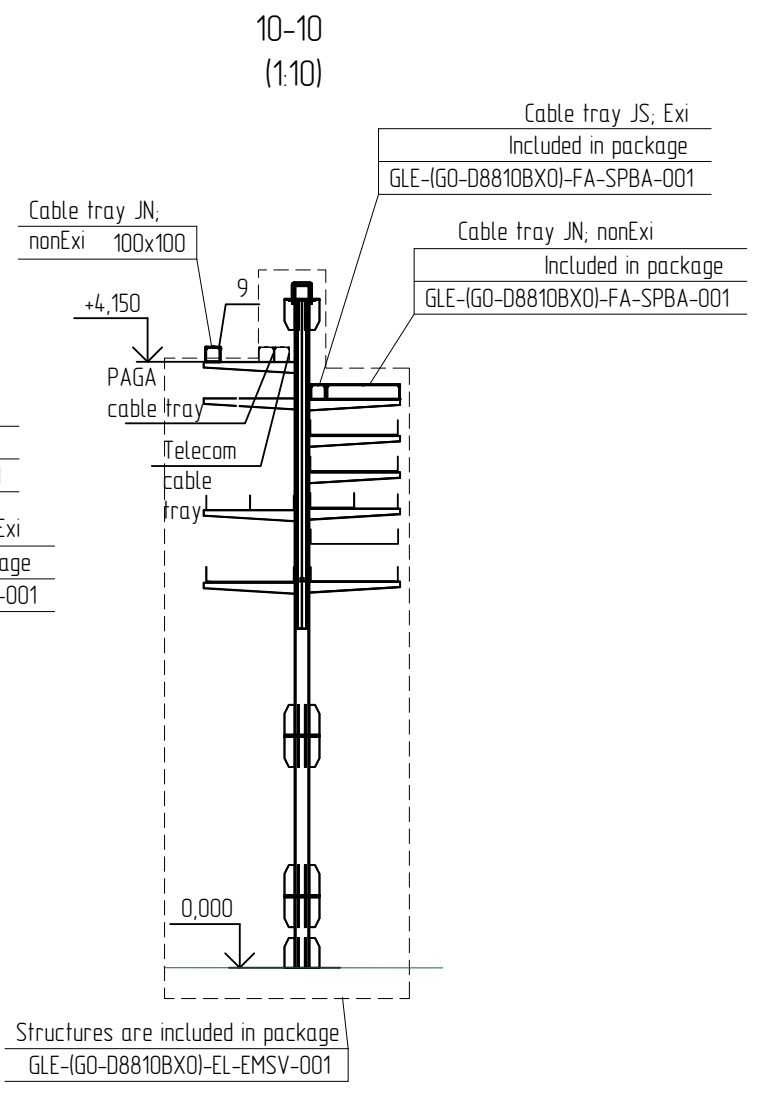

11-11 (1:10)

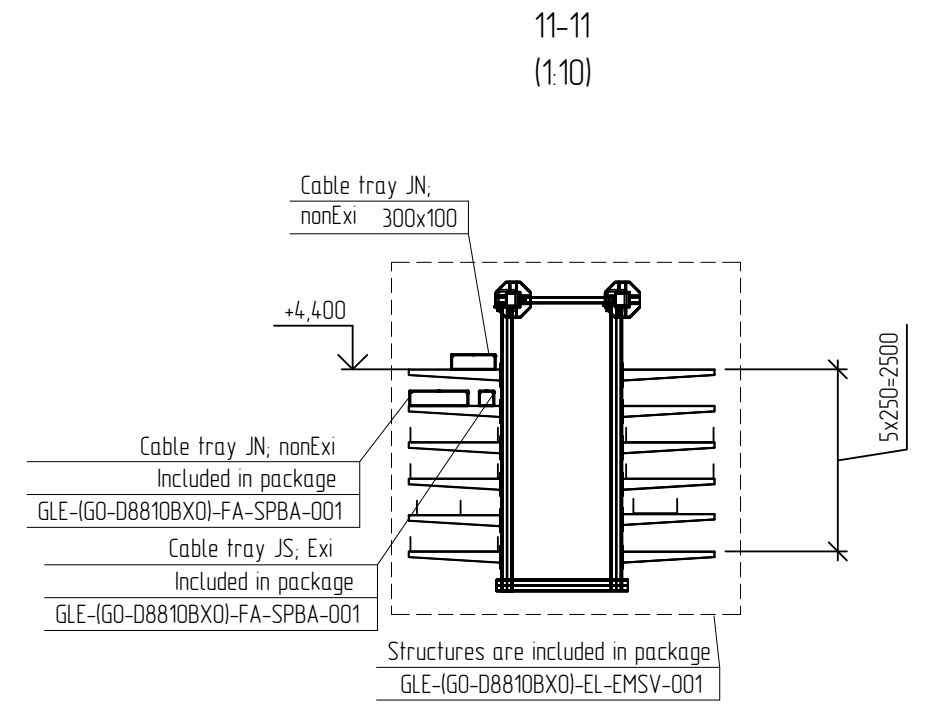

Multi-cable transit A, type 3 (Included in GLE-(GO-D8810BX0)-FA-SPBA-001)

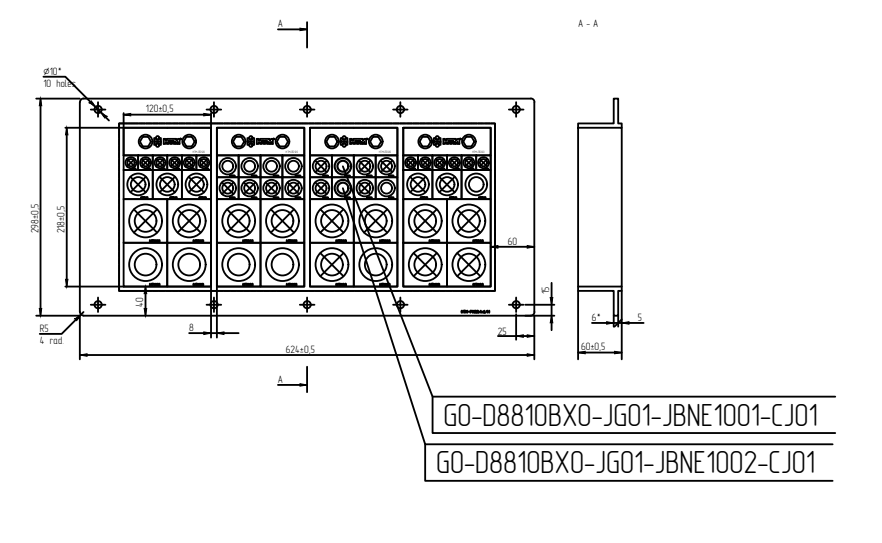

GO-D8810BX0-JG01-JBNE1001-CJ01
GO-D8810BX0-JG01-JBNE1002-CJ01

Multi-cable transit Б, type 3 (Included in GLE-(GO-D8810BX0)-FA-SPBA-001)

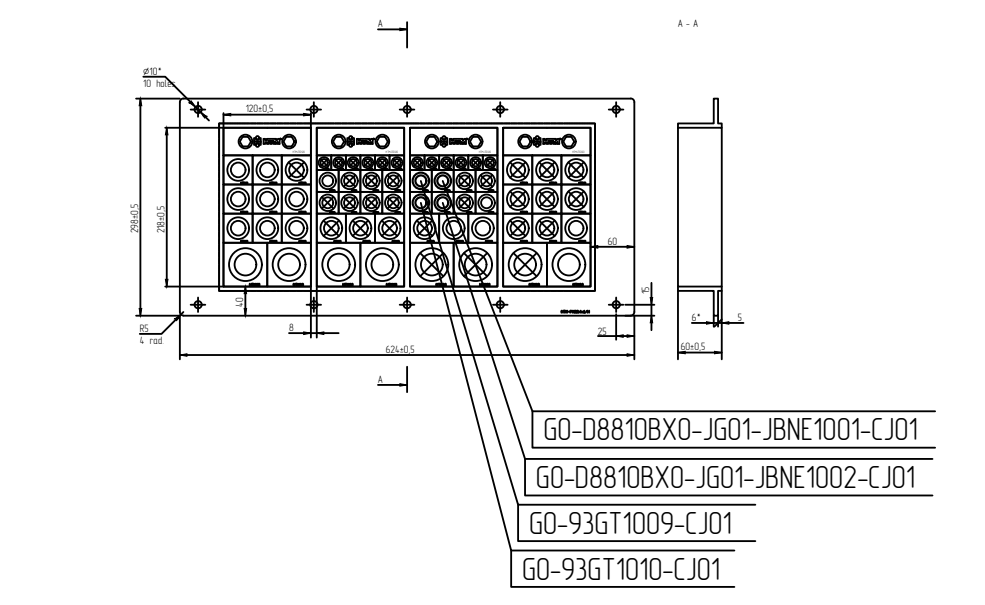

GO-D8810BX0-JG01-JBNE1001-CJ01
GO-D8810BX0-JG01-JBNE1002-CJ01
GO-93GT1009-CJ01
GO-93GT1010-CJ01

KEY PLAN

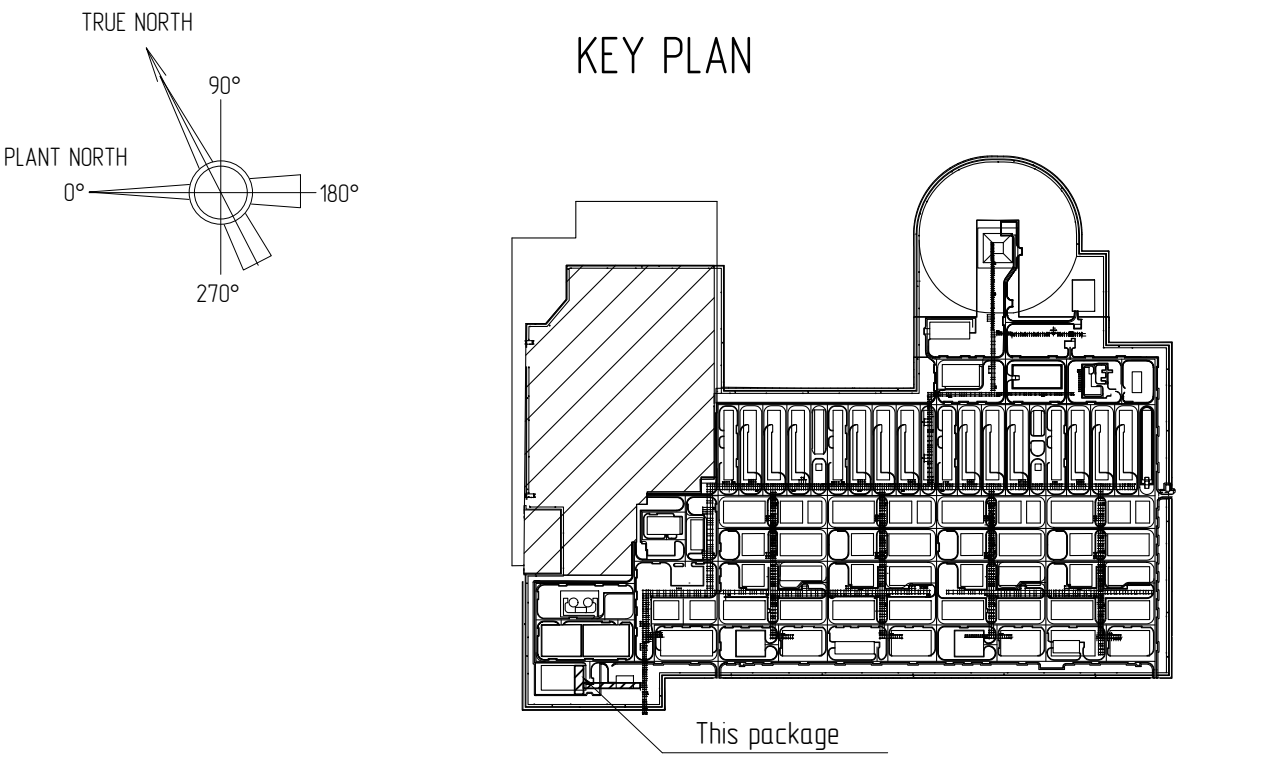

Статус Status	Рев. Rev.	Дата Date	Назначение выпуска / Reason for Issue	Разраб. Drawn	Провер. Checked	Утверд. Approved
IFC	03	04.12.25	Выпущено для строительства / Issued for Construction	Поминова	Тулба	Трофимов
IFC	02H	21.03.25	Выпущено для строительства / Issued for Construction	Шевцова	Охота	Подземельнов
IFR	01H	23.08.24	Выпущено для рассмотрения / Issued for Review	Гайсина	Гильманова	Трофимов

GAS PROCESSING COMPLEX WITHIN
UST-LUGA ETHANE-RICH GAS PROCESSING
CLUSTER. GAS PROCESSING PLANT AND
UTILITIES, INFRASTRUCTURE AND OFFSITE
PROCESS FACILITIES

GO-D8810BX0
Fire Water Pump Station

Stage	Sheet	Total Sheets
DDD	11	

Instrument and Cable Routing Plans
at el. 0,000; -3,000

РУСХИМАЛЬЯНС

GLE-(GO-D8810BX0)-IN-GDSS-001

ГАЗОПЕРЕРАБАТЫВАЮЩИЙ КОМПЛЕКС В СОСТАВЕ КОМПЛЕКСА ПЕРЕРАБОТКИ
ЭТАНОСОДЕРЖАЩЕГО ГАЗА В РАЙОНЕ ПОСЕЛКА УСТЬ-ЛУГА. ГАЗОПЕРЕРАБАТЫВАЮЩИЙ
ЗАВОД И ТЕХНОЛОГИЧЕСКИЕ ОБЪЕКТЫ ОБЩЕЗАВОДСКОГО ХОЗЯЙСТВА

Изм.	Кол.уч.	Лист	№док.	Подпись	Дата
Разраб.		Поминова			04.12.25
Проверил		Тулба			04.12.25
Нач. сект		Савчук			04.12.25
Н. контр.		Тулба			04.12.25
ГИП		Трофимов			04.12.25

GO-D8810BX0
Насосная станция противопожарного
водоснабжения

Стадия	Лист	Листов
Р	11	

План расположения КИПиА и прокладки
кабельных трасс на отм. 0,000; -3,000

ГЛИнжиниринг
ПРОЕКТИРУЕМ БУДУЩЕЕ ОТРАСЛИ

GLE-(GO-D8810BX0)-IN-GDSS-001_03_AL.dwg

Формат А1х3

Перечень элементов

Поз.	Наименование	Кол-во	Ед. Изм.	Примечание
1	Коробка клеммная взрывозащищенная; 722х363х167 мм (ШхВхГ), габаритные размеры даны предварительно и уточняются поставщиком; 2ExeIIBT3Gb; -; номинальное напряжение: ~400 В/V; номинальный ток: 24 А; материал корпуса: ударопрочный полиэстер; степень защиты по ГОСТ 14254-2015: не ниже IP66; климатическое исполнение и категория размещения У1 по ГОСТ 15150-69, температура эксплуатации от минус 43,2 до плюс 34,7 °С; -; пронумерованные подпружиненные винтовые клеммы: 33 шт. с возможностью подсоединения проводника сечением до 2,5 мм2, смонтированные на монтажную рейку в один ряд; на нижней стороне коробки: 8 отверстий под кабельный ввод М25х1,5; 2 отверстия под кабельный ввод М50х1,5; в комплекте: фланцевая пластина для монтажа и заземления кабельных вводов, дренажно-вентиляционное устройство (сертифицированное для применения во взрывоопасных зонах), внешний и внутренний заземляющий зажим, сертифицированные взрывозащищенные металлические заглушки с выгравированной маркировкой ЕАС для всех отверстий под кабельные вводы	2	шт.	GO-D8810BXO-JG01-JBNE1001 GO-D8810BXO-JG01-JBNE1002
2	Кабельный ввод М25х1,5; взрывозащищенный 2ExdIIBT3Gb; для небронированного кабеля круглого сечения с наружным диаметром от 12 до 18 мм; материал: никелированная латунь; степень защиты по ГОСТ 14254-2015 не менее IP66; с возможностью крепления герметичного металлорукава в ПВХ оболочке DN 25; в комплекте: адаптер М20х1,5, кольцо заземления, стопорная гайка, шайба, защитный кожух из ПВХ и др. необходимые аксессуары	26	шт.	
3	Кабельный ввод М50х1,5; взрывозащищенный 2ExdIIBT3Gb; для небронированного кабеля круглого сечения с наружным диаметром от 31 до 39 мм; материал: никелированная латунь; степень защиты по ГОСТ 14254-2015 не менее IP66; с возможностью крепления герметичного металлорукава в ПВХ оболочке DN 50; в комплекте: кольцо заземления, стопорная гайка, шайба, защитный кожух из ПВХ	4	шт.	

List of Elements

Item	Description	Qty	Unit	Note
1	Ex-proof junction box; 722x363x167mm (WxHxD), dimensions are preliminary and to be confirmed by Supplier; 2ExeIIBT3Gb; -; rated voltage: 400VAC; rated current: 24 A; casing material: shock-resistant polyester; IP rating acc. to GOST 14254-2015: min. IP66; climatic design and location category acc. to GOST 15150-69: У1, operating temperature: −43.2 to +34.7 °C; -; numbered spring-loaded screw terminals: 33 pcs suitable for connecting a conductor of up to 2.5 mm2 and installed on the mounting rack in one row; bottom side: 8 holes for cable entries M25x1.5; 2 holes for cable entries M50x1.5; complete with flange plate for installation and earthing of cable entries, drain and vent valves (certified for use in explosion hazardous areas), external and internal earthing clamp, certified ex-proof steel plugs with engraved EAC marking for all cable entries	2	pcs	GO-D8810BXO-JG01-JBNE1001 GO-D8810BXO-JG01-JBNE1002
2	Cable entry M25x1.5; explosion protection type: 2ExdIIBT3Gb; for non-armored cable with round cross-section and outside diameter from 12 to 18 mm; material: nickel plated brass; IP rating acc. to GOST 14254-2015: min. IP66; suitable for connection of PVC-sheathed sealed conduit DN25; complete with adapter M20x1,5, earthing ring, lock nut, washer, PVC jacket, and other accessories	26	pcs	
3	Cable entry M50x1.5; explosion protection type: 2ExdIIBT3Gb; for non-armored cable with round cross-section and outside diameter from 31 to 39 mm; material: nickel plated brass; IP rating acc. to GOST 14254-2015: min. IP66; suitable for connection of PVC-sheathed sealed conduit DN50; complete with earthing ring, lock nut, washer, PVC jacket	4	pcs	

1 Экран кабеля со стороны полевых датчиков (за исключением искробезопасных цепей) заизолировать, но оставить доступным. Для искробезопасных цепей подключение и/или изолирование экранов кабелей, корпусов и т.д. выполнить в строгом соответствии с требованиями инструкций заводов-изготовителей КИП. Резервные жилы кабеля со стороны полевых датчиков заизолировать.

2 Оборудование должно соответствовать требованиям GLE-(GO-Z00000XO)-IN-SD-025 "Технические требования на клеммные коробки КИПиА"

3 Монтаж защитного заземления выполнить в соответствии с требованиями ПУЭ, ГОСТ 12.1.030-81,

СП 76.13330.2016 (п 6.12.19), GLE-(GO-Z00000XO)-IN-SQ-004.

4 Длина кабелей и способ прокладки приведены в кабельном журнале GLE-(G1-D3201FXO)-IN-GDSS-001.

5 Нумерация кабелей, жил кабелей выполнена в соответствии с требованиями GSP-(GO-Z00000XO)-DC-PR-004, GLE-(GO-Z00000XO)-IN-LN-001.

1 Cable shield from field transmitters (except for intrinsically safe circuits) shall be insulated and accessible. Cable shields, enclosures etc. of intrinsically safe circuits shall be connected and/or isolated in strict accordance with the requirements of instrumentation manufacturer's instructions. The spare cable cores on the side of the field sensors shall be insulated.

2 Equipment should meet requirements of GLE-(GO-Z00000XO)-IN-SD-025 *Specification I&C Junction Boxes*

3 The protective earthing shall be in accordance with the requirements of PUE, GOST 12.1.030-81, SP 76.13330.2016 (para. 6.12.19), GLE-(GO-Z00000XO)-IN-SQ-004.

4 Cable length and cable routing are shown in cable schedule GLE-(G1-D3201FXO)-IN-GDSS-001..

5 Cable and cable core numbering is provided according to GSP-(GO-Z00000XO)-DC-PR-004, GLE-(GO-Z00000XO)-IN-LN-001.

Согласовано

Взам. инв. №

Подп. и дата

Инв. № подл.

Статус Status	Рев. Rev.	Дата Date	Назначение выпуска / Reason for Issue	Разраб. Drawn	Провер. Checked	Утверд. Approved
IFC	03	04.12.25	Выпущено для строительства / Issued for Construction	Поминова	Тулба	Трофимов
IFC	02H	21.03.25	Выпущено для строительства / Issued for Construction	Шевцова	Охота	Подземельнов
IFR	01H	23.08.24	Выпущено для рассмотрения / Issued for Review	Гайсина	Гильманова	Трофимов

GAS PROCESSING COMPLEX WITHIN UST-LUGA ETHANE-RICH GAS PROCESSING CLUSTER. GAS PROCESSING PLANT AND UTILITIES, INFRASTRUCTURE AND OFFSITE PROCESS FACILITIES

GO-D8810BXO
Fire Water Pump Station

Stage	Sheet	Total Sheets
DDD	12	

External Wiring Diagrams

РУСХИМАЛЬЯНС

GLE-(GO-D8810XO)-IN-GDSS-001

ГАЗОПЕРЕРАБАТЫВАЮЩИЙ КОМПЛЕКС В СОСТАВЕ КОМПЛЕКСА ПЕРЕРАБОТКИ ЭТАНОСОДЕРЖАЩЕГО ГАЗА В РАЙОНЕ ПОСЕЛКА УСТЬ-ЛУГА. ГАЗОПЕРЕРАБАТЫВАЮЩИЙ ЗАВОД И ТЕХНОЛОГИЧЕСКИЕ ОБЪЕКТЫ ОБЩЕЗАВОДСКОГО ХОЗЯЙСТВА

Изм.	Кол.уч.	Лист	№док.	Подпись	Дата
Разраб.		Поминова			04.12.25
Проверил		Тулба			04.12.25
Нач. сект		Савчук			04.12.25
Н. контр.		Тулба			04.12.25
ГИП		Трофимов			04.12.25

GO-D8810FXO
Насосная станция противопожарного водоснабжения

Стадия	Лист	Листов
Р	12	

Схемы внешних соединений

ГЛИнжиниринг
ПРОЕКТИРУЕМ БУДУЩЕЕ ОТРАСЛИ

Контроль загазованности в машинном зале на отм. +1.000 (этан)
Gas detection in the engine room at el. +1.000 (ethane)

Контроль загазованности в машинном зале на отм. +1.000 (этан)
Gas detection in the engine room at el. +1.000 (ethane)

Контроль загазованности в машинном зале на отм. +0.500 (пропан)
Gas detection in the engine room at el. +0.500 (propane)

Контроль загазованности в машинном зале на отм. +0.500 (пропан)
Gas detection in the engine room at el. +0.500 (propane)

~~Контроль загазованности в~~ воздухозаборе на отм. +3.300 (метан)
Gas detection contamination in the air intake at el. +3.300 (methane)

Контроль загазованности в воздухозаборе на отм. +3.300 (метан)
Gas detection contamination in the air intake at el. +3.300 (methane)

03.1

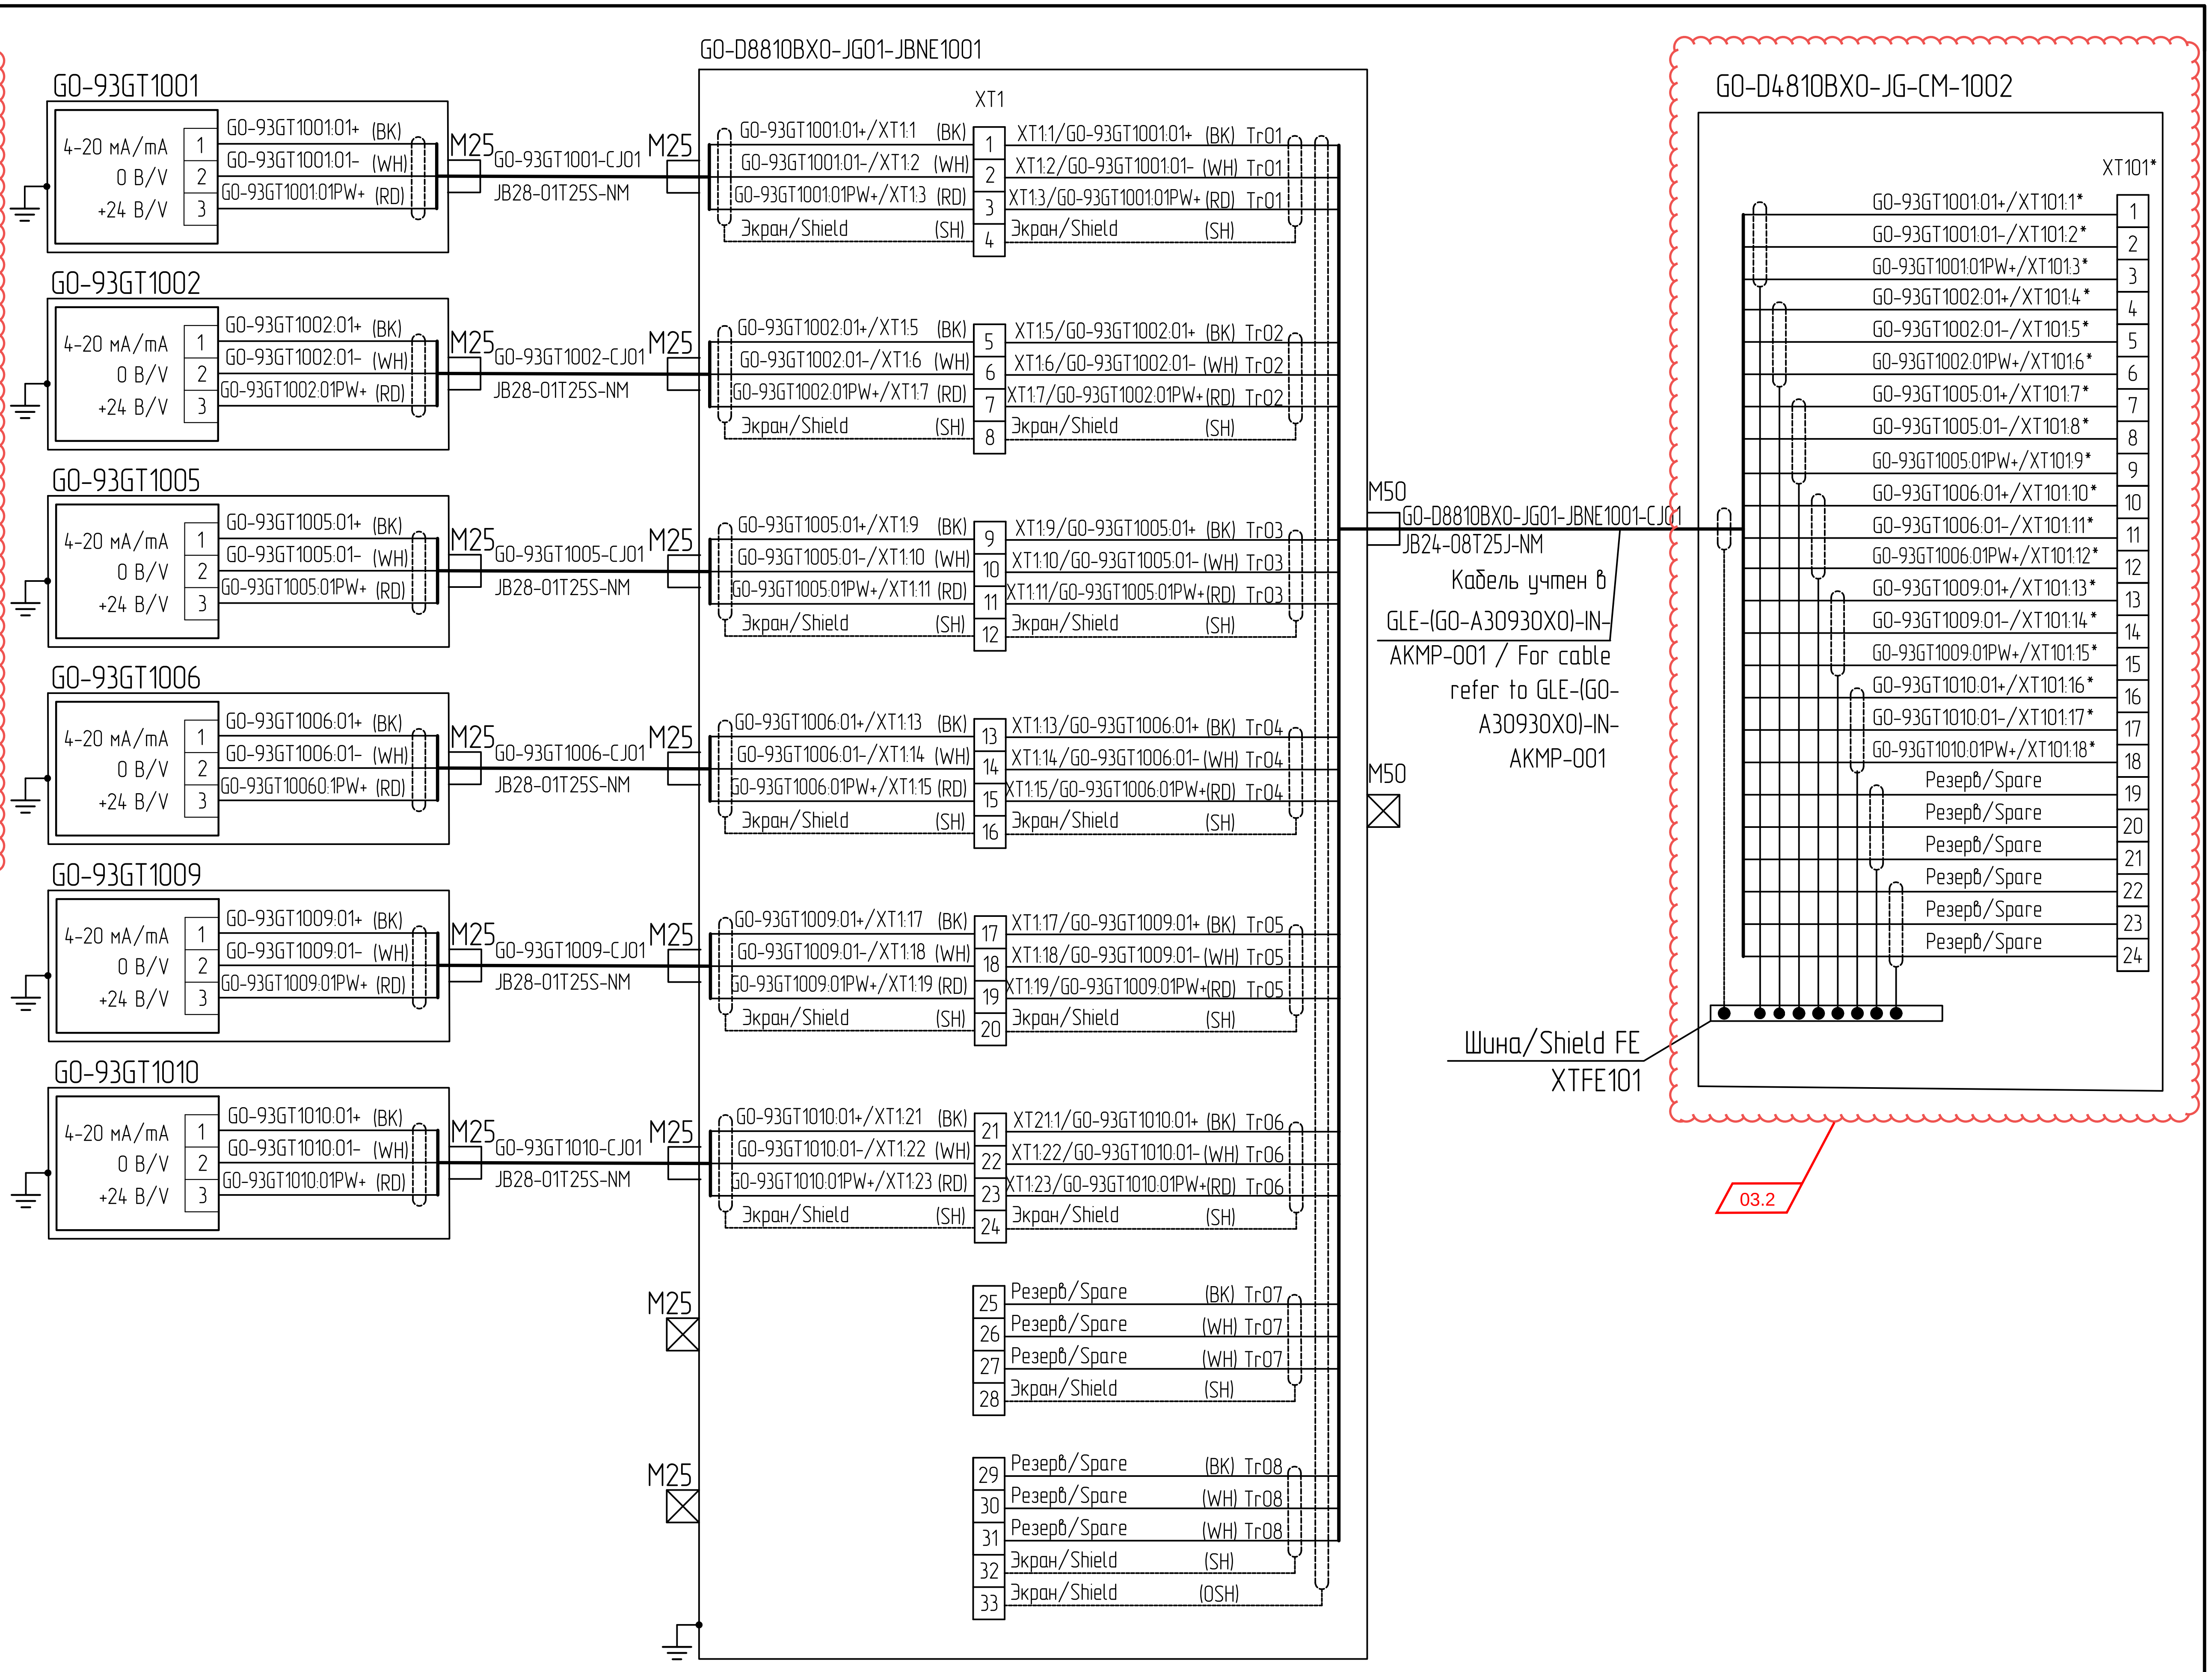
GO-93GT1001
GO-93GT1002
GO-93GT1005
GO-93GT1006
GO-93GT1009
GO-93GT1010
4-20 mA/mA
0 B/V
+24 B/V
1
2
3
GO-93GT1001.01+ (BK)
GO-93GT1001.01- (WH)
GO-93GT1001.01PW+ (RD)
GO-93GT1002.01+ (BK)
GO-93GT1002.01- (WH)
GO-93GT1002.01PW+ (RD)
GO-93GT1005.01+ (BK)
GO-93GT1005.01- (WH)
GO-93GT1005.01PW+ (RD)
GO-93GT1006.01+ (BK)
GO-93GT1006.01- (WH)
GO-93GT10060.1PW+ (RD)
GO-93GT1009.01+ (BK)
GO-93GT1009.01- (WH)
GO-93GT1009.01PW+ (RD)
GO-93GT1010.01+ (BK)
GO-93GT1010.01- (WH)
GO-93GT1010.01PW+ (RD)
M25
GO-93GT1001-CJ01
GO-93GT1002-CJ01
GO-93GT1005-CJ01
GO-93GT1006-CJ01
GO-93GT1009-CJ01
GO-93GT1010-CJ01
JB28-01T25S-NM
GO-D8810BXO-JG01-JBNE1001
XT1
GO-93GT1001.01+/XT1.1 (BK)
GO-93GT1001.01-/XT1.2 (WH)
GO-93GT1001.01PW+/XT1.3 (RD)
Экран/Shield (SH)
XT1.1/GO-93GT1001.01+ (BK) Tr01
XT1.2/GO-93GT1001.01- (WH) Tr01
XT1.3/GO-93GT1001.01PW+ (RD) Tr01
GO-93GT1002.01+/XT1.5 (BK)
GO-93GT1002.01-/XT1.6 (WH)
GO-93GT1002.01PW+/XT1.7 (RD)
XT1.5/GO-93GT1002.01+ (BK) Tr02
XT1.6/GO-93GT1002.01- (WH) Tr02
XT1.7/GO-93GT1002.01PW+ (RD) Tr02
GO-93GT1005.01+/XT1.9 (BK)
GO-93GT1005.01-/XT1.10 (WH)
GO-93GT1005.01PW+/XT1.11 (RD)
XT1.9/GO-93GT1005.01+ (BK) Tr03
XT1.10/GO-93GT1005.01- (WH) Tr03
XT1.11/GO-93GT1005.01PW+ (RD) Tr03
GO-93GT1006.01+/XT1.13 (BK)
GO-93GT1006.01-/XT1.14 (WH)
GO-93GT1006.01PW+/XT1.15 (RD)
XT1.13/GO-93GT1006.01+ (BK) Tr04
XT1.14/GO-93GT1006.01- (WH) Tr04
XT1.15/GO-93GT1006.01PW+ (RD) Tr04
GO-93GT1009.01+/XT1.17 (BK)
GO-93GT1009.01-/XT1.18 (WH)
GO-93GT1009.01PW+/XT1.19 (RD)
XT1.17/GO-93GT1009.01+ (BK) Tr05
XT1.18/GO-93GT1009.01- (WH) Tr05
XT1.19/GO-93GT1009.01PW+ (RD) Tr05
GO-93GT1010.01+/XT1.21 (BK)
GO-93GT1010.01-/XT1.22 (WH)
GO-93GT1010.01PW+/XT1.23 (RD)
XT21.1/GO-93GT1010.01+ (BK) Tr06
XT1.22/GO-93GT1010.01- (WH) Tr06
XT1.23/GO-93GT1010.01PW+ (RD) Tr06
Резерв/Spare (BK) Tr07
Резерв/Spare (WH) Tr07
Резерв/Spare (WH) Tr07
Экран/Shield (SH)
Резерв/Spare (BK) Tr08
Резерв/Spare (WH) Tr08
Резерв/Spare (WH) Tr08
Экран/Shield (SH)
Экран/Shield (OSH)
1 2 3 4 5 6 7 8 9 10 11 12 13 14 15 16 17 18 19 20 21 22 23 24 25 26 27 28 29 30 31 32 33
M50
GO-D8810BXO-JG01-JBNE1001-CJ01
JB24-08T25J-NM
Кабель учтен в GLE-(GO-A30930XO)-IN-AKMP-001 / For cable refer to GLE-(GO-A30930XO)-IN-AKMP-001
M50
GO-D4810BXO-JG-CM-1002
XT101*
GO-93GT1001.01+/XT101.1*
GO-93GT1001.01-/XT101.2*
GO-93GT1001.01PW+/XT101.3*
GO-93GT1002.01+/XT101.4*
GO-93GT1002.01-/XT101.5*
GO-93GT1002.01PW+/XT101.6*
GO-93GT1005.01+/XT101.7*
GO-93GT1005.01-/XT101.8*
GO-93GT1005.01PW+/XT101.9*
GO-93GT1006.01+/XT101.10*
GO-93GT1006.01-/XT101.11*
GO-93GT1006.01PW+/XT101.12*
GO-93GT1009.01+/XT101.13*
GO-93GT1009.01-/XT101.14*
GO-93GT1009.01PW+/XT101.15*
GO-93GT1010.01+/XT101.16*
GO-93GT1010.01-/XT101.17*
GO-93GT1010.01PW+/XT101.18*
Резерв/Spare
Резерв/Spare
Резерв/Spare
Резерв/Spare
Резерв/Spare
Резерв/Spare
1 2 3 4 5 6 7 8 9 10 11 12 13 14 15 16 17 18 19 20 21 22 23 24
Шина/Shield FE
XTFE101
03.2

*- Подключение клемм со стороны шкафа смотри документ GLE-(GO-D4810BXO)-IN-ESD-LR-001
Refer to document GLE-(GO-D4810BXO)-IN-ESD-LR-001 for connection of terminals on the cabinet side

Изм.	Кол.уч.	Лист	№док.	Подп.	Дата	GLE-(GO-D8810BXO)-IN-GDSS-001	Лист 13

Взам. инв. №
Подп. и дата
Инв. № подл.

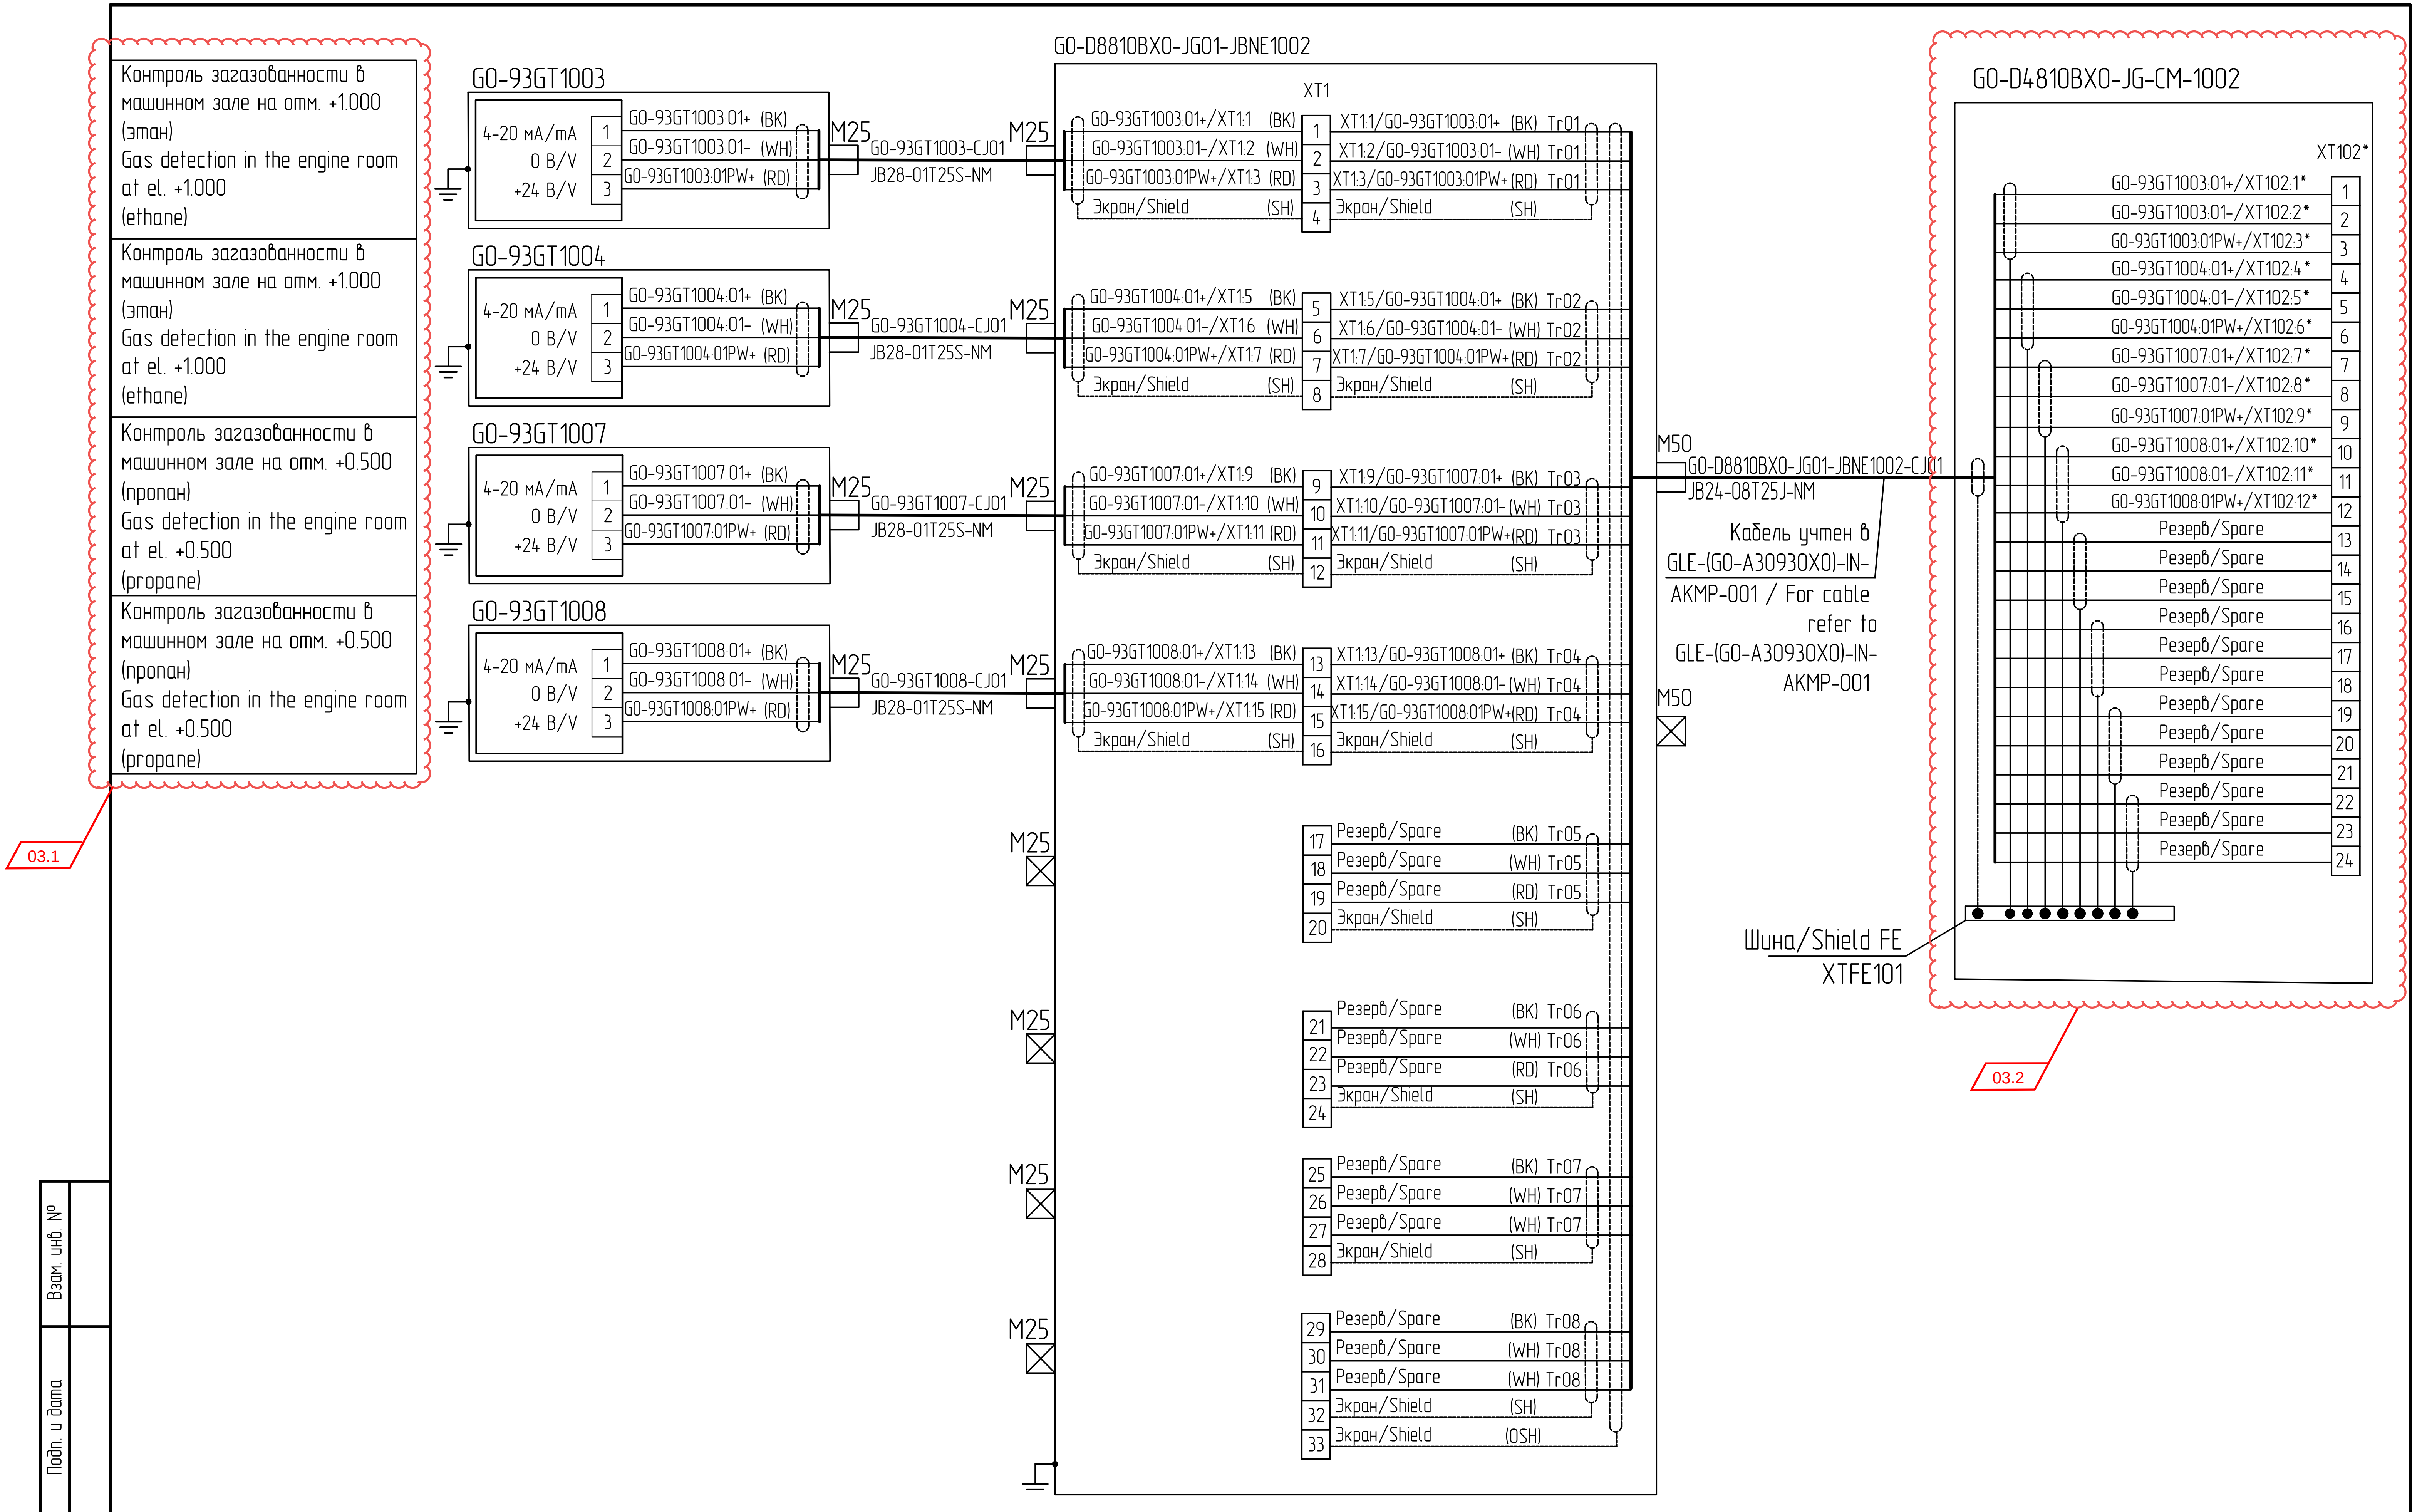
Контроль загазованности в машинном зале на отм. +1.000 (этан)
Gas detection in the engine room at el. +1.000 (ethane)
Контроль загазованности в машинном зале на отм. +1.000 (этан)
Gas detection in the engine room at el. +1.000 (ethane)
Контроль загазованности в машинном зале на отм. +0.500 (пропан)
Gas detection in the engine room at el. +0.500 (propane)
Контроль загазованности в машинном зале на отм. +0.500 (пропан)
Gas detection in the engine room at el. +0.500 (propane)
03.1
GO-93GT1003
4-20 мА/mA
0 В/V
+24 В/V
1
2
3
GO-93GT1003.01+ (BK)
GO-93GT1003.01- (WH)
GO-93GT1003.01PW+ (RD)
M25
GO-93GT1003-CJ01
JB28-01T25S-NM
GO-93GT1004
GO-93GT1004.01+ (BK)
GO-93GT1004.01- (WH)
GO-93GT1004.01PW+ (RD)
GO-93GT1004-CJ01
JB28-01T25S-NM
GO-93GT1007
GO-93GT1007.01+ (BK)
GO-93GT1007.01- (WH)
GO-93GT1007.01PW+ (RD)
GO-93GT1007-CJ01
JB28-01T25S-NM
GO-93GT1008
GO-93GT1008.01+ (BK)
GO-93GT1008.01- (WH)
GO-93GT1008.01PW+ (RD)
GO-93GT1008-CJ01
JB28-01T25S-NM
GO-D8810BXO-JG01-JBNE1002
XT1
GO-93GT1003.01+/XT1.1 (BK) 1 XT1.1/GO-93GT1003.01+ (BK) Tr01
GO-93GT1003.01-/XT1.2 (WH) 2 XT1.2/GO-93GT1003.01- (WH) Tr01
GO-93GT1003.01PW+/XT1.3 (RD) 3 XT1.3/GO-93GT1003.01PW+ (RD) Tr01
Экран/Shield (SH) 4 Экран/Shield (SH)
GO-93GT1004.01+/XT1.5 (BK) 5 XT1.5/GO-93GT1004.01+ (BK) Tr02
GO-93GT1004.01-/XT1.6 (WH) 6 XT1.6/GO-93GT1004.01- (WH) Tr02
GO-93GT1004.01PW+/XT1.7 (RD) 7 XT1.7/GO-93GT1004.01PW+ (RD) Tr02
Экран/Shield (SH) 8 Экран/Shield (SH)
GO-93GT1007.01+/XT1.9 (BK) 9 XT1.9/GO-93GT1007.01+ (BK) Tr03
GO-93GT1007.01-/XT1.10 (WH) 10 XT1.10/GO-93GT1007.01- (WH) Tr03
GO-93GT1007.01PW+/XT1.11 (RD) 11 XT1.11/GO-93GT1007.01PW+ (RD) Tr03
Экран/Shield (SH) 12 Экран/Shield (SH)
GO-93GT1008.01+/XT1.13 (BK) 13 XT1.13/GO-93GT1008.01+ (BK) Tr04
GO-93GT1008.01-/XT1.14 (WH) 14 XT1.14/GO-93GT1008.01- (WH) Tr04
GO-93GT1008.01PW+/XT1.15 (RD) 15 XT1.15/GO-93GT1008.01PW+ (RD) Tr04
Экран/Shield (SH) 16 Экран/Shield (SH)
17 Резерв/Spare (BK) Tr05
18 Резерв/Spare (WH) Tr05
19 Резерв/Spare (RD) Tr05
20 Экран/Shield (SH)
21 Резерв/Spare (BK) Tr06
22 Резерв/Spare (WH) Tr06
23 Резерв/Spare (RD) Tr06
24 Экран/Shield (SH)
25 Резерв/Spare (BK) Tr07
26 Резерв/Spare (WH) Tr07
27 Резерв/Spare (WH) Tr07
28 Экран/Shield (SH)
29 Резерв/Spare (BK) Tr08
30 Резерв/Spare (WH) Tr08
31 Резерв/Spare (WH) Tr08
32 Экран/Shield (SH)
33 Экран/Shield (OSH)
M25
M25
M25
M25
M50
GO-D8810BXO-JG01-JBNE1002-CJ01
JB24-08T25J-NM
Кабель учтен в GLE-(GO-A30930XO)-IN-AKMP-001 / For cable refer to GLE-(GO-A30930XO)-IN-AKMP-001
M50
GO-D4810BXO-JG-CM-1002
XT102*
GO-93GT1003.01+/XT102.1* 1
GO-93GT1003.01-/XT102.2* 2
GO-93GT1003.01PW+/XT102.3* 3
GO-93GT1004.01+/XT102.4* 4
GO-93GT1004.01-/XT102.5* 5
GO-93GT1004.01PW+/XT102.6* 6
GO-93GT1007.01+/XT102.7* 7
GO-93GT1007.01-/XT102.8* 8
GO-93GT1007.01PW+/XT102.9* 9
GO-93GT1008.01+/XT102.10* 10
GO-93GT1008.01-/XT102.11* 11
GO-93GT1008.01PW+/XT102.12* 12
Резерв/Spare 13
Резерв/Spare 14
Резерв/Spare 15
Резерв/Spare 16
Резерв/Spare 17
Резерв/Spare 18
Резерв/Spare 19
Резерв/Spare 20
Резерв/Spare 21
Резерв/Spare 22
Резерв/Spare 23
Резерв/Spare 24
Шина/Shield FE
XTFE101
03.2

*- Подключение клемм со стороны шкафа смотри документ GLE-(GO-D4810BXO)-IN-ESD-LR-001

Refer to document GLE-(GO-D4810BXO)-IN-ESD-LR-001 for connection of terminals on the cabinet side

Взам. инв. №

Подп. и дата

Инв. № подл.

Изм.	Кол.уч	Лист	№док.	Подп.	Дата

Сводка кабелей, трубы и металлорукава
Cable, pipe and flexible conduits summary

Наименование Title	Число жил, сечение, диаметр Quantity and cross-section of cores	Длина, м Length, m
1x3x2,5	1x3x2,5	238
Металлорукав / Flexible conduit	DN 25	33

1. Расшифровку идентификаторов кабеля см. документ GLE-(G0-Z00000X0)-IN-LN-001 (Матрица кабелей).
2. Длины кабелей, трубы и металлорукава необходимо уточнить перед нарезкой по месту.
3. * - данные будут уточнены после получения полного комплекта РКД.

1. For cable identifier description refer to document GLE-(G0-Z00000X0)-IN-LN-001 (Cable Matrix).
2. Length of cables, pipes and flexible conduits shall be confirmed before cutting on site.
3. * - the data will be clarified after receiving the complete set of RCD.

IFC	03	04.12.25	Выпущено для строительства / Issued for Construction	Поминова	Тулба	Трофимов
IFC	02H	21.03.25	Выпущено для строительства / Issued for Construction	Шевцова	Охота	Подземельнов
Статус Status	Рев. Rev.	Дата Date	Назначение выпуска / Reason for Issue	Разработал Prepared	Проверил Reviewed	Утвердил Approved

GAS PROCESSING COMPLEX WITHIN UST-LUGA ETHANE-RICH GAS PROCESSING CLUSTER. GAS PROCESSING PLANT AND UTILITIES, INFRASTRUCTURE AND OFFSITE PROCESS FACILITIES

G0-D8810BX0
Fire Water Pump Station

Stage	Sheet No.	Total sheets
DDD	15	

Cable Schedule

РУСХИМАЛЬЯНС

GLE-(G0-D8810BX0)-IN-GDSS-001

Газоперерабатывающий комплекс в составе Комплекса переработки этансодержащего газа в районе поселка Усть-Луга.
Газоперерабатывающий завод и Технологические объекты общезаводского хозяйства

Изм.	Кол.уч.	Лист	№ док.	Подп.	Дата

Разработал	Поминова		04.12.25
Проверил	Тулба		04.12.25
Нач. сект.	Савчук		04.12.25
Н. контр.	Тулба		04.12.25
ГИП	Трофимов		04.12.25

G0-D8810BX0 Насосная станция противопожарного водоснабжения

Стадия	Лист	Листов
Р	15	

Кабельный журнал

ГЛИнжиниринг
ПРОЕКТИРУЕМ БУДУЩЕЕ ОТРАСЛИ

Взам. инв. №

Подпись и дата

Инв. № подл.

Наименование кабеля Cable Title	Трасса Tray		Кабель, провод Cable, conductor			Проход через / Passage through				Примечание Note
						лоток / траншея tray / trench		металлорукав flexible conduits		
	Начало Start	Конец End	Идентификатор кабеля Cable ID	Кол., число и сечение жил Quantity and cross-section of cores	Длина, м Length, m	Лоток, м Tray, m	Траншея, м Trench, m	Диаметр мм Diameter, mm	Длина, м Length, m	
1	2	3	4	5	6	7	8	9	10	11
G0-93GT1001-CJ01	Газоанализатор ДВК Gas detector G0-93GT1001	Клеммная коробка Junction box G0-D8810BX0-JG01-JBNE1001	JB28-01T25S-NM	1x3x2,5	6	4	-	DN25	2	
G0-93GT1002-CJ01	Газоанализатор ДВК Gas detector G0-93GT1002	Клеммная коробка Junction box G0-D8810BX0-JG01-JBNE1001	JB28-01T25S-NM	1x3x2,5	14	12	-	DN25	2	
G0-93GT1005-CJ01	Газоанализатор ДВК Gas detector G0-93GT1005	Клеммная коробка Junction box G0-D8810BX0-JG01-JBNE1001	JB28-01T25S-NM	1x3x2,5	6	4	-	DN25	2	
G0-93GT1006-CJ01	Газоанализатор ДВК Gas detector G0-93GT1006	Клеммная коробка Junction box G0-D8810BX0-JG01-JBNE1001	JB28-01T25S-NM	1x3x2,5	14	12	-	DN25	2	
G0-93GT1009-CJ01	Газоанализатор ДВК Gas detector G0-93GT1009	Клеммная коробка Junction box G0-D8810BX0-JG01-JBNE1001	JB28-01T25S-NM	1x3x2,5	75	66	-	DN25	9	
G0-93GT1010-CJ01	Газоанализатор ДВК Gas detector G0-93GT1010	Клеммная коробка Junction box G0-D8810BX0-JG01-JBNE1001	JB28-01T25S-NM	1x3x2,5	75	77	-	DN25	8	
G0-93GT1003-CJ01	Газоанализатор ДВК Gas detector G0-93GT1003	Клеммная коробка Junction box G0-D8810BX0-JG01-JBNE1002	JB28-01T25S-NM	1x3x2,5	13	11	-	DN25	2	
G0-93GT1004-CJ01	Газоанализатор ДВК Gas detector G0-93GT1004	Клеммная коробка Junction box G0-D8810BX0-JG01-JBNE1002	JB28-01T25S-NM	1x3x2,5	11	9	-	DN25	2	
G0-93GT1007-CJ01	Газоанализатор ДВК Gas detector G0-93GT1007	Клеммная коробка Junction box G0-D8810BX0-JG01-JBNE1002	JB28-01T25S-NM	1x3x2,5	13	11	-	DN25	2	
G0-93GT1008-CJ01	Газоанализатор ДВК Gas detector G0-93GT1008	Клеммная коробка Junction box G0-D8810BX0-JG01-JBNE1002	JB28-01T25S-NM	1x3x2,5	11	9	-	DN25	2	

Взам. инв. №

Подпись и дата

Инв. № подп.

Изм.	Кол.уч.	Лист	№ док.	Подп.	Дата	GLE-(G0-D8810BX0)-IN-GDSS-001	Лист
							16

Лист регистрации изменений

Статус	Рев.	Место изменения	Краткое описание
IFC	02H	Весь документ	Внесены изменения на основании замечаний Заказчика GLE-(G0-D8810BX0)-IN-GDSS-001_01H_RU_CRS
IFC	03	Листы 1, 2, 4, 8-11, 13-16	Внесены изменения согласноTQS-GPP-RHI-GSP-IN-03129_R00
IFC	03	Весь документ	Добавлен перевод

Revision Change Details

Status	Rev.	Location of Changes	Brief Description of Changes
IFC	02H	All document	Updated according to the Owner's comments GLE-(G0-D8810BX0)-IN-GDSS-001_01H_RU_CRS
IFC	03	Pages 1, 2, 4, 8-11, 13-16	Updated according to TQS-GPP-RHI-GSP-IN-03129_R00
IFC	03	All document	Translation added